

FRONT ELEVATION WORKING


PLOT NO. 24 SIZE - 19'-2"x35'-0"

ALI HOUSING SCHEME



SALMAN AMJAD AND ASSOCIATES:

ARCHITECT, INTERIOR DESIGN, CONSTRUCTION.
APPROVED AS CATEGORY-A ARCHITECT LDA.
REGISTERED PCATP-06011 AND LDA TPRA-298.
OFFICE NO. 35 GROUND FLOOR, MIAN PLAZA.
JOHAR TOWN, LAHORE Mobile no. : 0306-4706139.

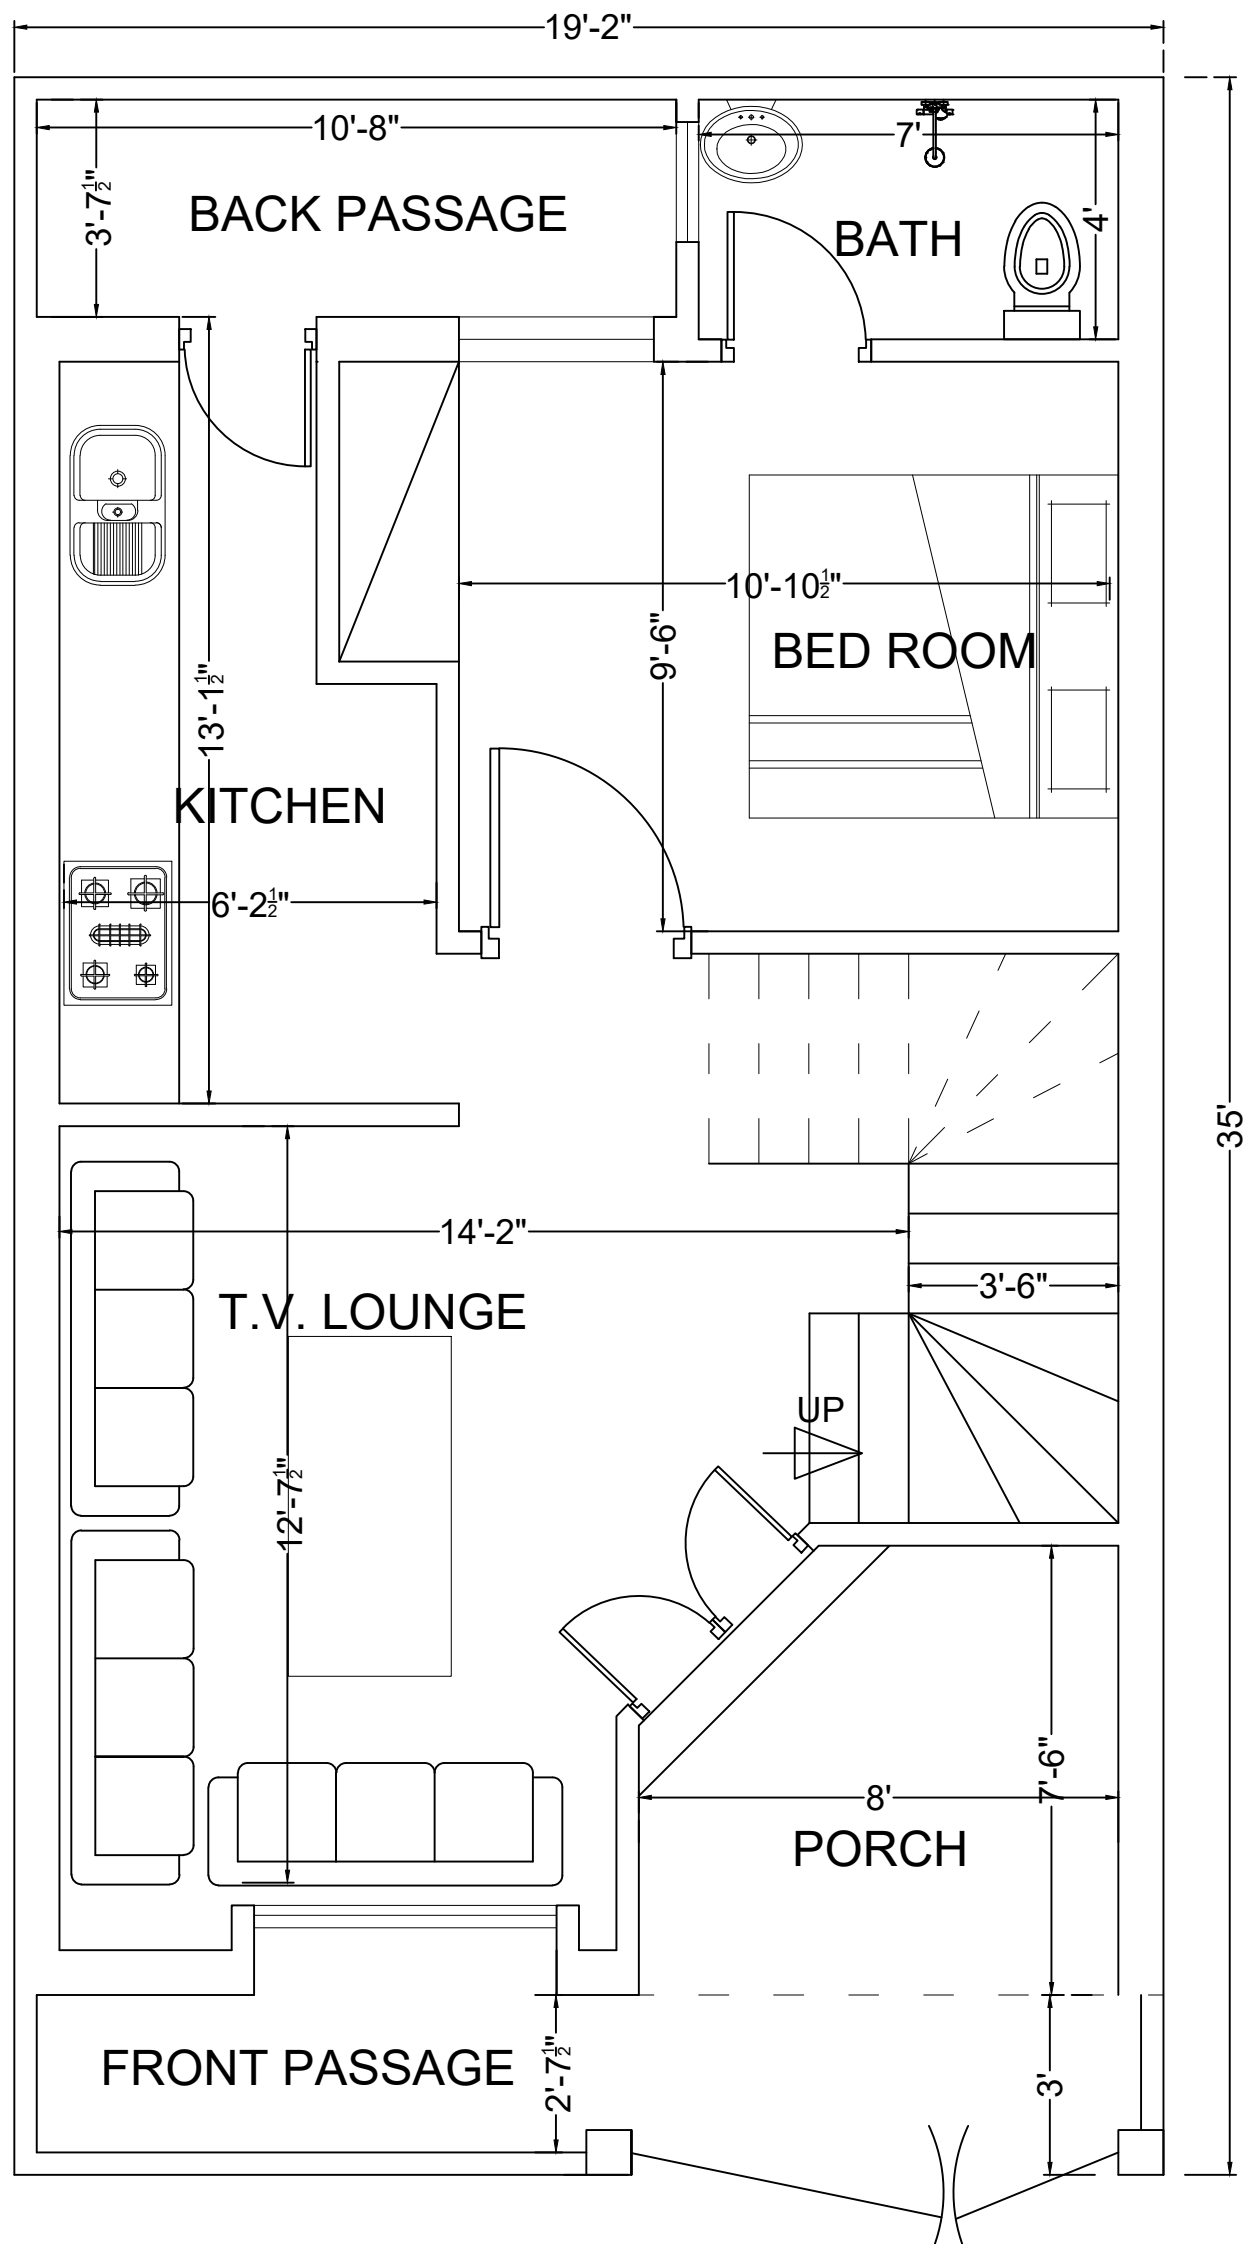


GROUND FLOOR PLAN

PLOT NO. 16 SIZE - 19'-2"x35'-0"-ABU BAKAR BLOCK
ALI HOUSING SCHEME



SALMAN AMJAD AND ASSOCIATES:

ARCHITECT, INTERIOR DESIGN, CONSTRUCTION.
APPROVED AS CATEGORY-A ARCHITECT LDA.
REGISTERED PCATP-06011 AND LDA TPRA-298.
OFFICE NO. 35 GROUND FLOOR, MIAN PLAZA.
JOHAR TOWN, LAHORE Mobile no. : 0306-4706139.

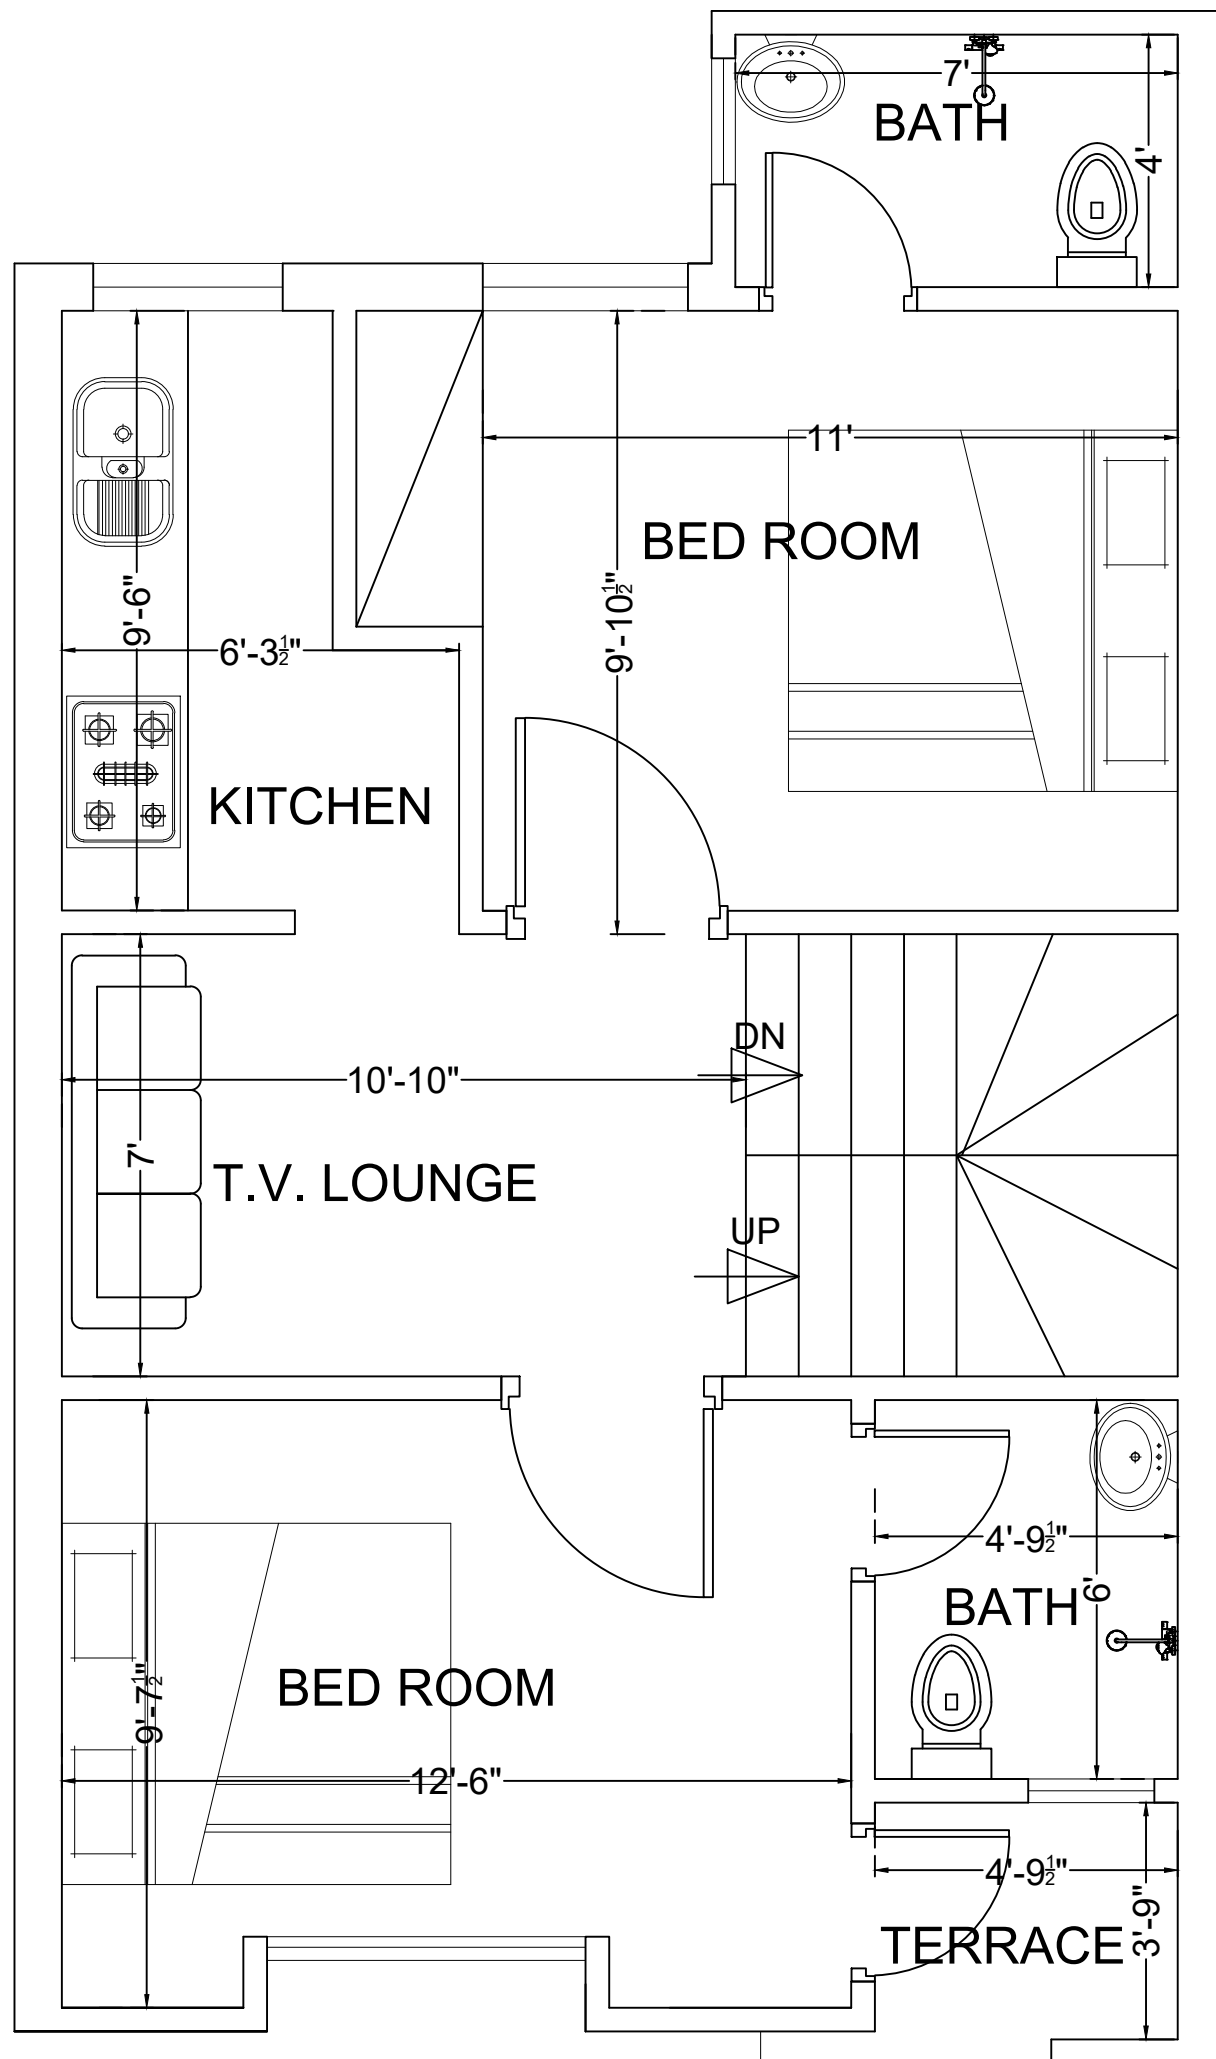

FIRST FLOOR PLAN


PLOT NO. 16 SIZE - 19'-2"x35'-0"-ABU BAKAR BLOCK

ALI HOUSING SCHEME



SALMAN AMJAD AND ASSOCIATES:

ARCHITECT, INTERIOR DESIGN, CONSTRUCTION.
 APPROVED AS CATEGORY-A ARCHITECT LDA.
 REGISTERED PCATP-06011 AND LDA TPRA-298.
 OFFICE NO. 35 GROUND FLOOR, MIAN PLAZA.
 JOHAR TOWN, LAHORE Mobile no. : 0306-4706139.

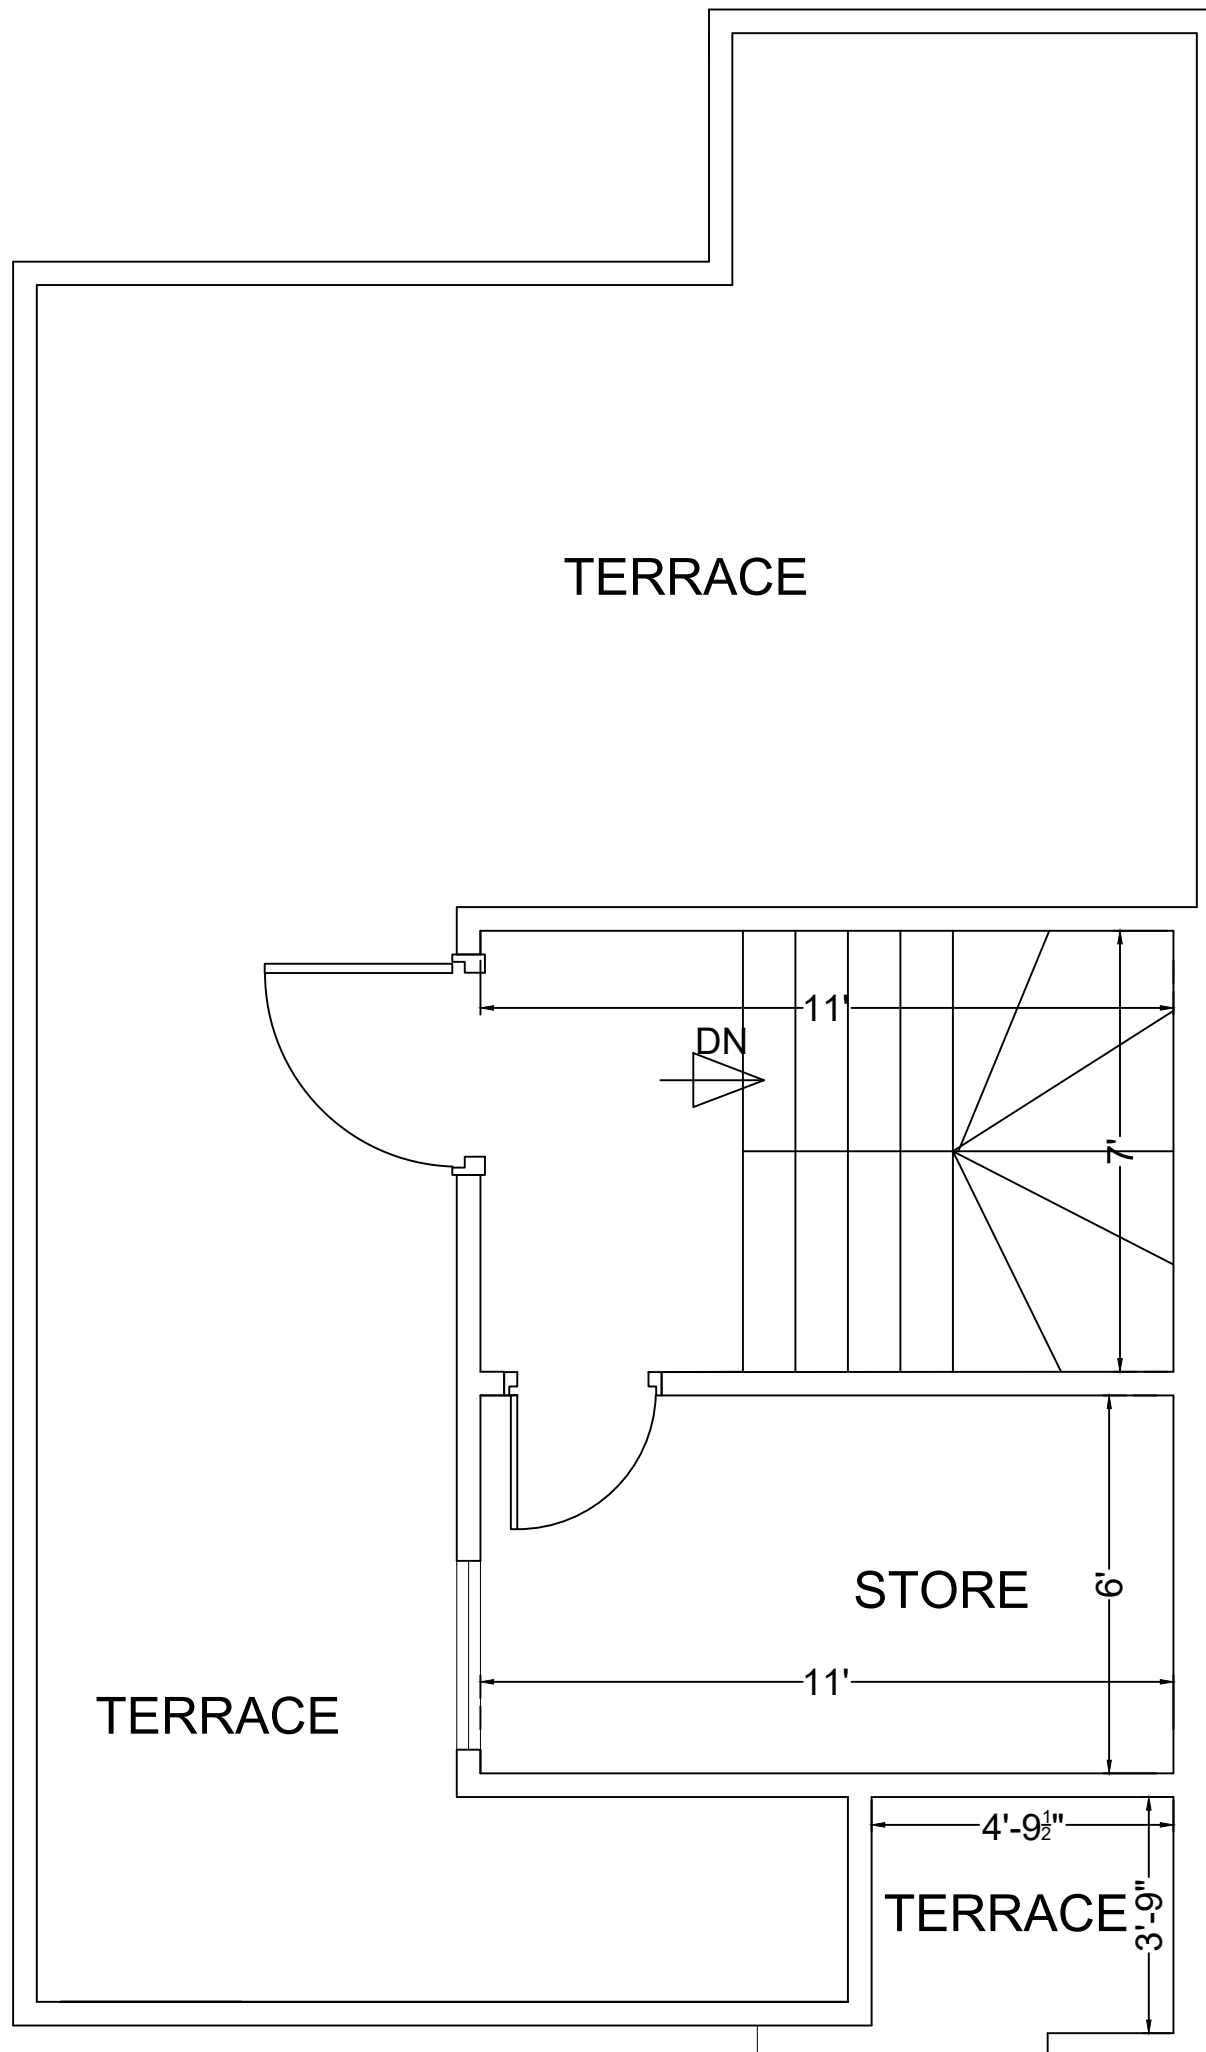

SECOND FLOOR PLAN


PLOT NO. 16 SIZE - 19'-2"x35'-0"-ABU BAKAR BLOCK

ALI HOUSING SCHEME



SALMAN AMJAD AND ASSOCIATES:

ARCHITECT, INTERIOR DESIGN, CONSTRUCTION.
APPROVED AS CATEGORY-A ARCHITECT LDA.
REGISTERED PCATP-06011 AND LDA TPRA-298.
OFFICE NO. 35 GROUND FLOOR, MIAN PLAZA.
JOHAR TOWN, LAHORE Mobile no. : 0306-4706139.

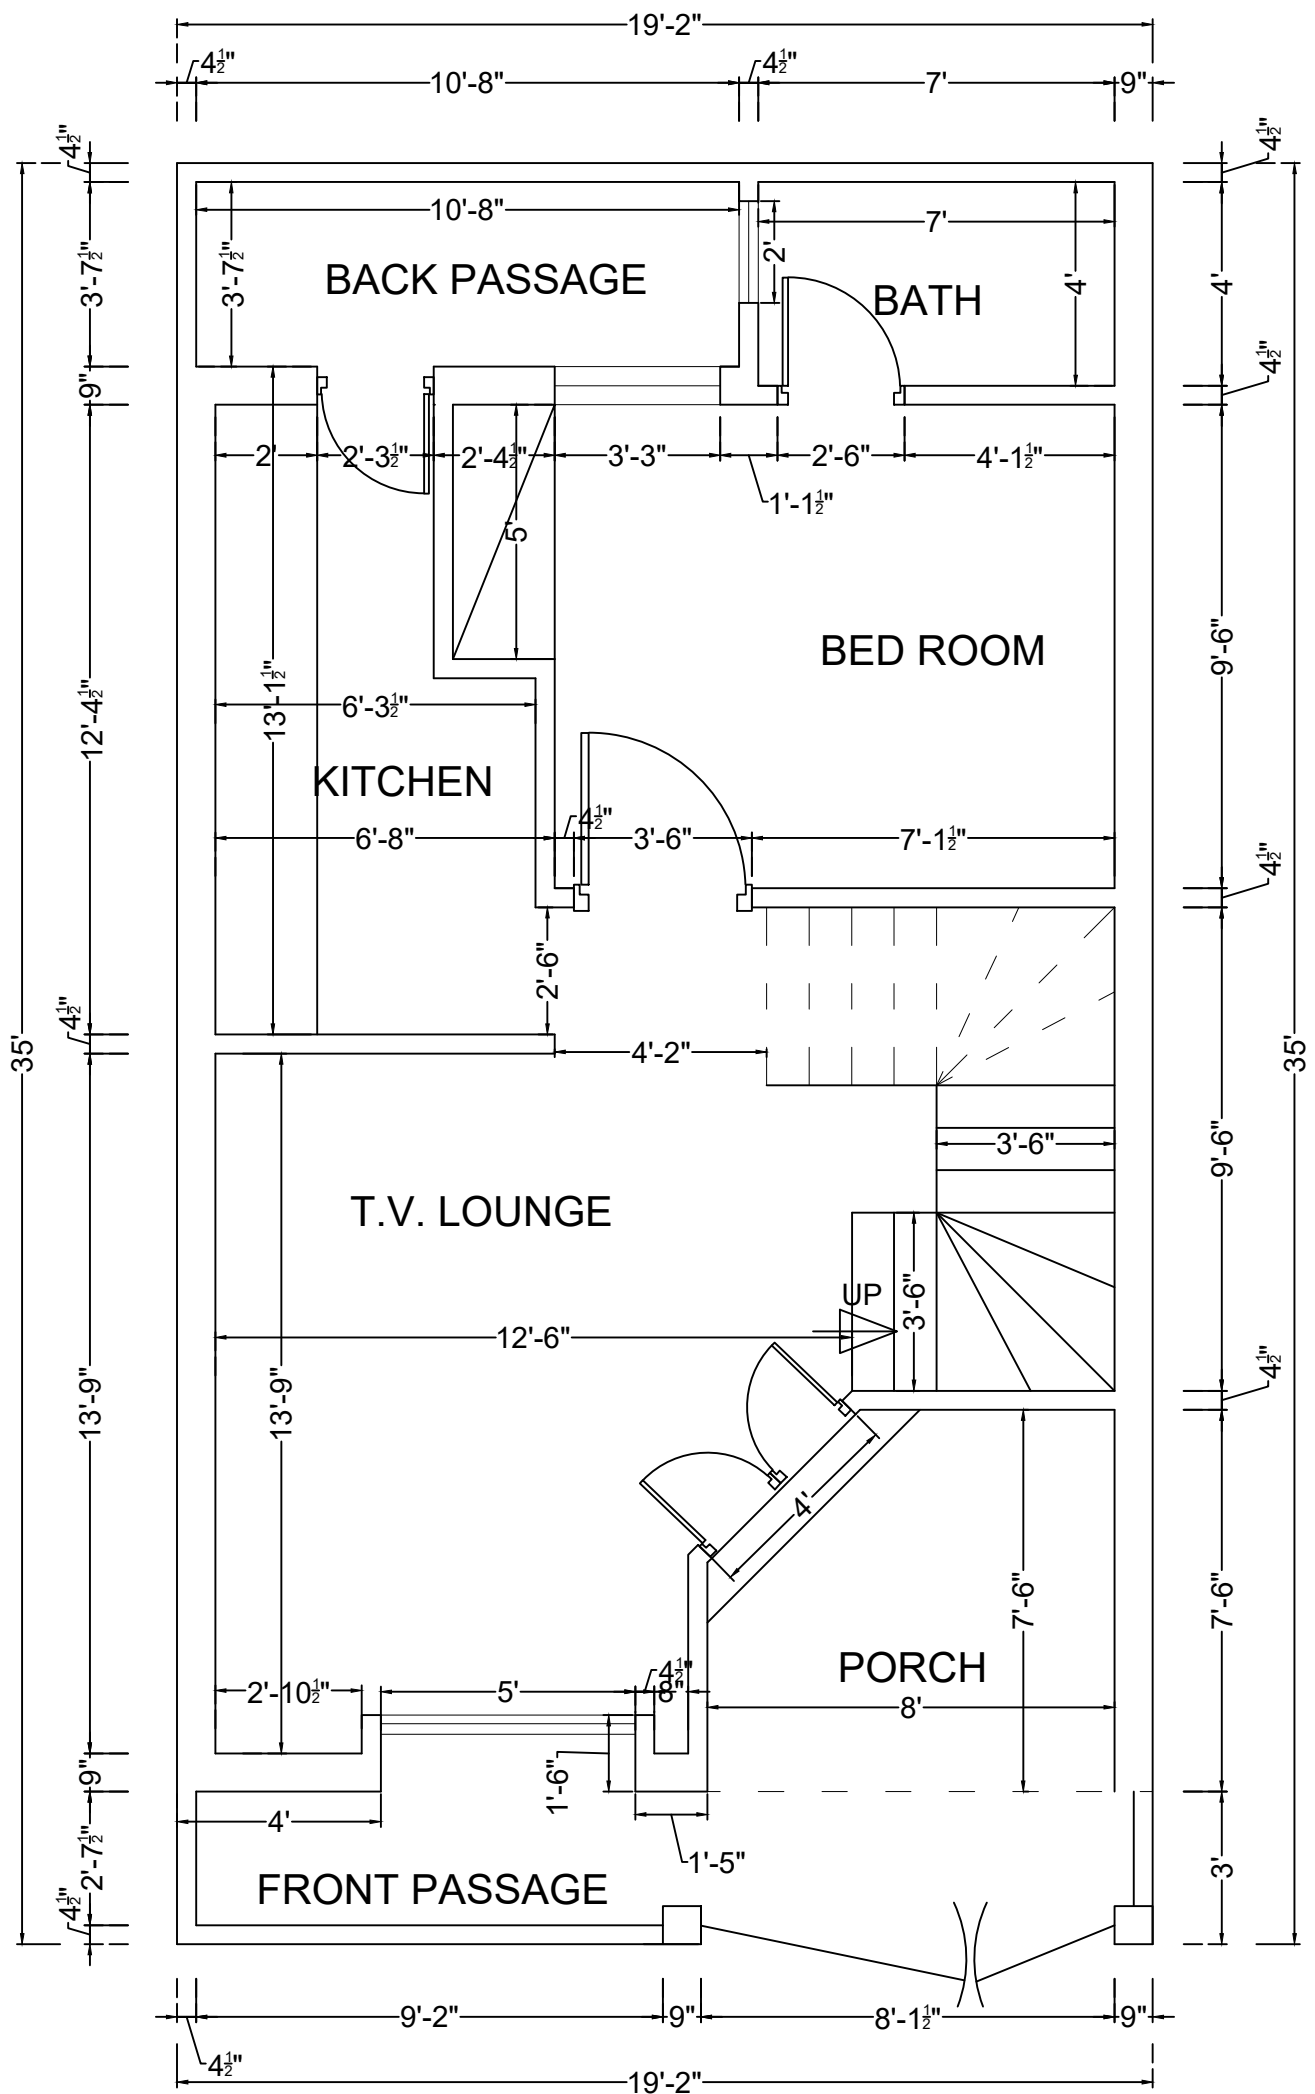


MAIN ENTRANCE
GROUND FLOOR WORKING PLAN
PLOT NO. 16 SIZE - 19'-2"x35'-0"
ALI HOUSING SCHEME



SALMAN AMJAD AND ASSOCIATES:

ARCHITECT, INTERIOR DESIGN, CONSTRUCTION.
APPROVED AS CATEGORY-A ARCHITECT LDA.
REGISTERED PCATP-06011 AND LDA TPRA-298.
OFFICE NO. 35 GROUND FLOOR, MIAN PLAZA.
JOHAR TOWN, LAHORE Mobile no. : 0306-4706139.

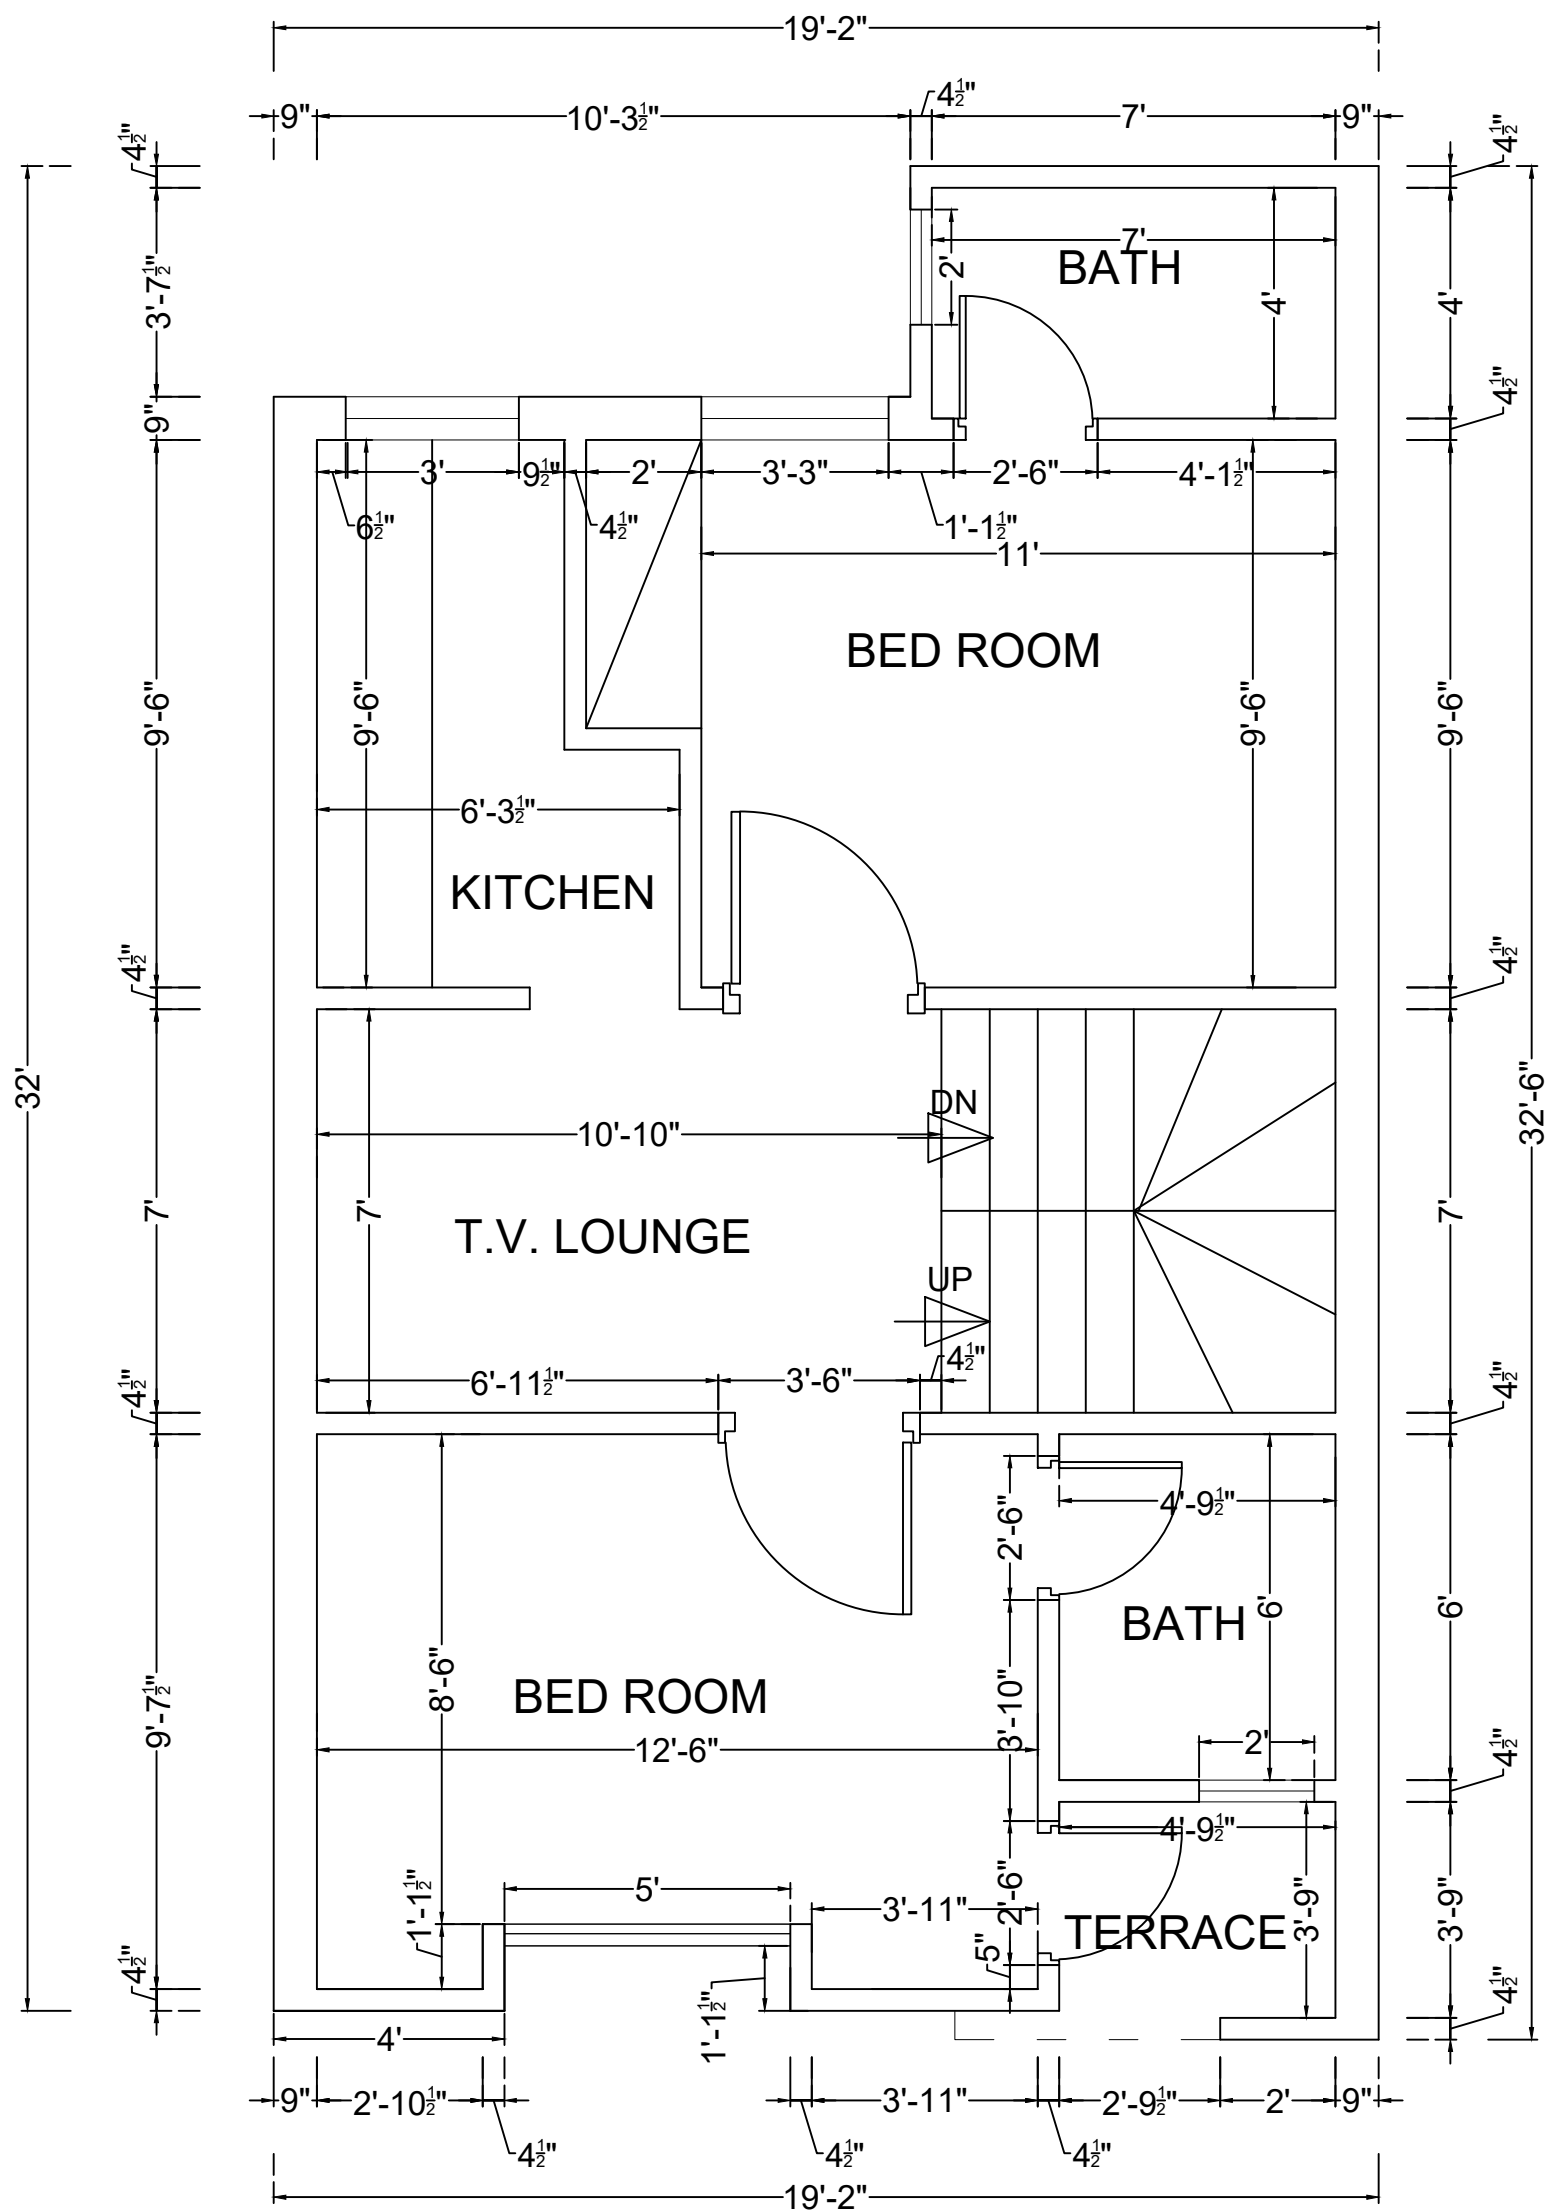


FIRST FLOOR WORKING PLAN
 PLOT NO. 16 SIZE - 19'-2"x35'-0"
 ALI HOUSING SCHEME



SALMAN AMJAD AND ASSOCIATES:

ARCHITECT, INTERIOR DESIGN, CONSTRUCTION.
 APPROVED AS CATEGORY-A ARCHITECT LDA.
 REGISTERED PCATP-06011 AND LDA TPRA-298.
 OFFICE NO. 35 GROUND FLOOR, MIAN PLAZA.
 JOHAR TOWN, LAHORE Mobile no. : 0306-4706139.

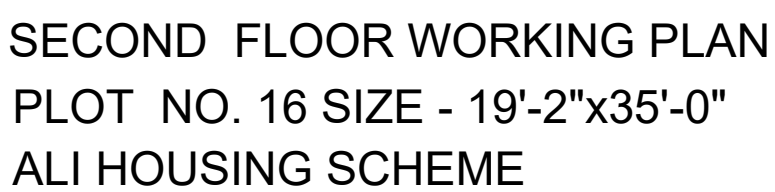

ARCHITECT, INTERIOR DESIGN, CONSTRUCTION.
APPROVED AS CATEGORY-A ARCHITECT LDA.
REGISTERED PCATP-06011 AND LDA TPRA-298.
OFFICE NO. 35 GROUND FLOOR, MIAN PLAZA.
JOHAR TOWN, LAHORE Mobile no. : 0306-4706139.

LEGEND FOR SYMBOLS-ELECTRICAL WORKS		
SIGN.	DESCRIPTION	SILL LEVEL
	WALL LIGHT	8'-0"
	WATER PROOF LIGHT	AS SITE
	CEILING LIGHT	9'-6" OR A.S.
	CHANDILIER LIGHT	9'-6" OR A.S.
	CONCEALED LIGHT	AS SITE
	SPOT LIGHT	9'-6" OR A.S.
	CEILING FAN	9'-6" OR A.S.
	20W SINGLE TUBE LIGHT	AS SITE
	40W SINGLE TUBE LIGHT	8'-0"
	WALL SOCKET	4'-0"
	3 PIN SWITCH	1'-0" OR A.S.
	SPLIT A.C.	8'-0"
	EXHAUST FAN	AS SITE
	DISTRIBUTION BOARD	5'-0"
	T.V. POINT	4'-0"
	TELEPHONE POINT	1'-0"
	GATE INTERCOM	4'-0"
	INTERCOM RECEIVER	4'-0"
	BELL PUSH	4'-0"



ELECTRICAL SCHEDULE

PLOT NO. 16 SIZE - 19'-2"x35'-0"
ALI HOUSING SCHEME



SALMAN AMJAD AND ASSOCIATES:

ARCHITECT, INTERIOR DESIGN, CONSTRUCTION.
APPROVED AS CATEGORY-A ARCHITECT LDA.
REGISTERED PCATP-06011 AND LDA TPRA-298.
OFFICE NO. 35 GROUND FLOOR, MIAN PLAZA.
JOHAR TOWN, LAHORE Mobile no. : 0306-4706139.

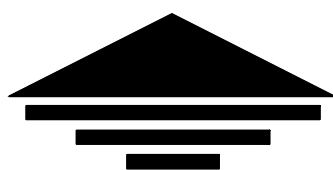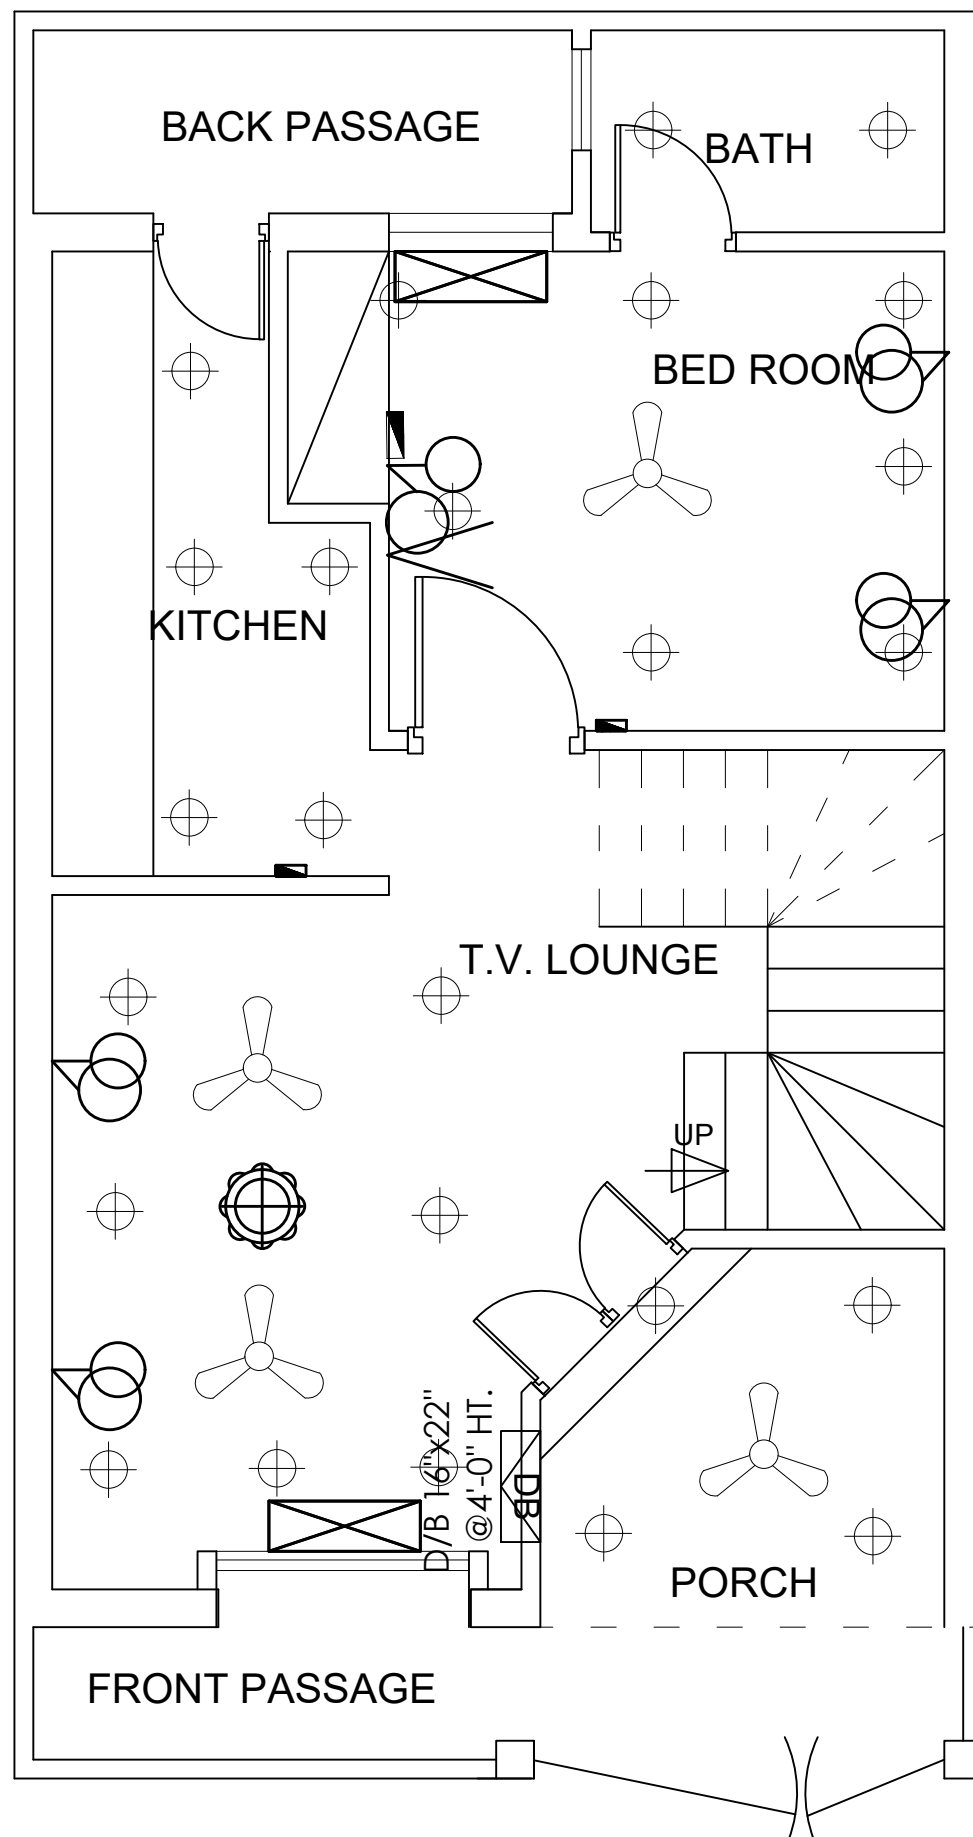


MAIN ENTRANCE

GROUND FLOOR PLAN (ELECTRICAL)
PLOT NO. 16 SIZE - 19'-2"x35'-0"
ALI HOUSING SCHEME



SALMAN AMJAD AND ASSOCIATES:

ARCHITECT, INTERIOR DESIGN, CONSTRUCTION.
APPROVED AS CATEGORY-A ARCHITECT LDA.
REGISTERED PCATP-06011 AND LDA TPRA-298.
OFFICE NO. 35 GROUND FLOOR, MIAN PLAZA.
JOHAR TOWN, LAHORE Mobile no. : 0306-4706139.

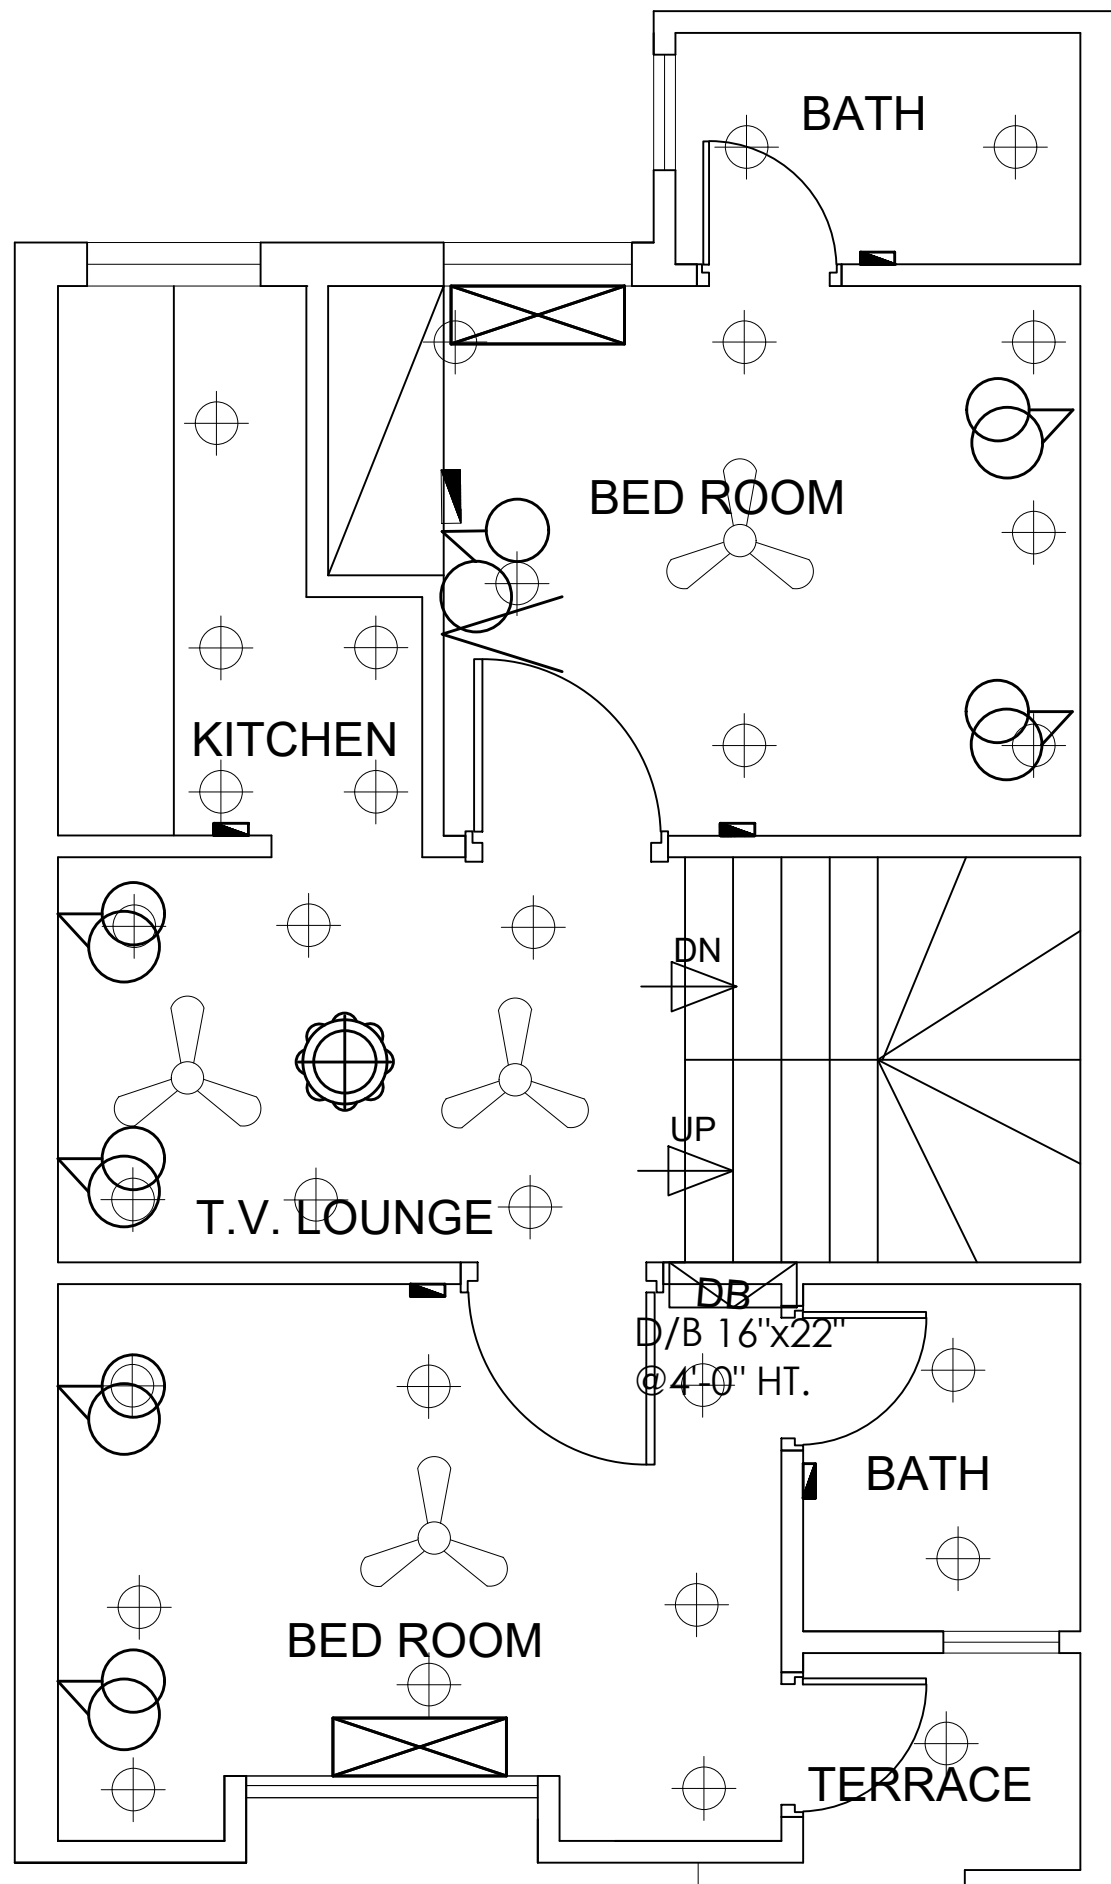


FIRST FLOOR PLAN (ELECTRICAL)
 PLOT NO. 16 SIZE - 19'-2"x35'-0"
 ALI HOUSING SCHEME



SALMAN AMJAD AND ASSOCIATES:

ARCHITECT, INTERIOR DESIGN, CONSTRUCTION.
 APPROVED AS CATEGORY-A ARCHITECT LDA.
 REGISTERED PCATP-06011 AND LDA TPRA-298.
 OFFICE NO. 35 GROUND FLOOR, MIAN PLAZA.
 JOHAR TOWN, LAHORE Mobile no. : 0306-4706139.

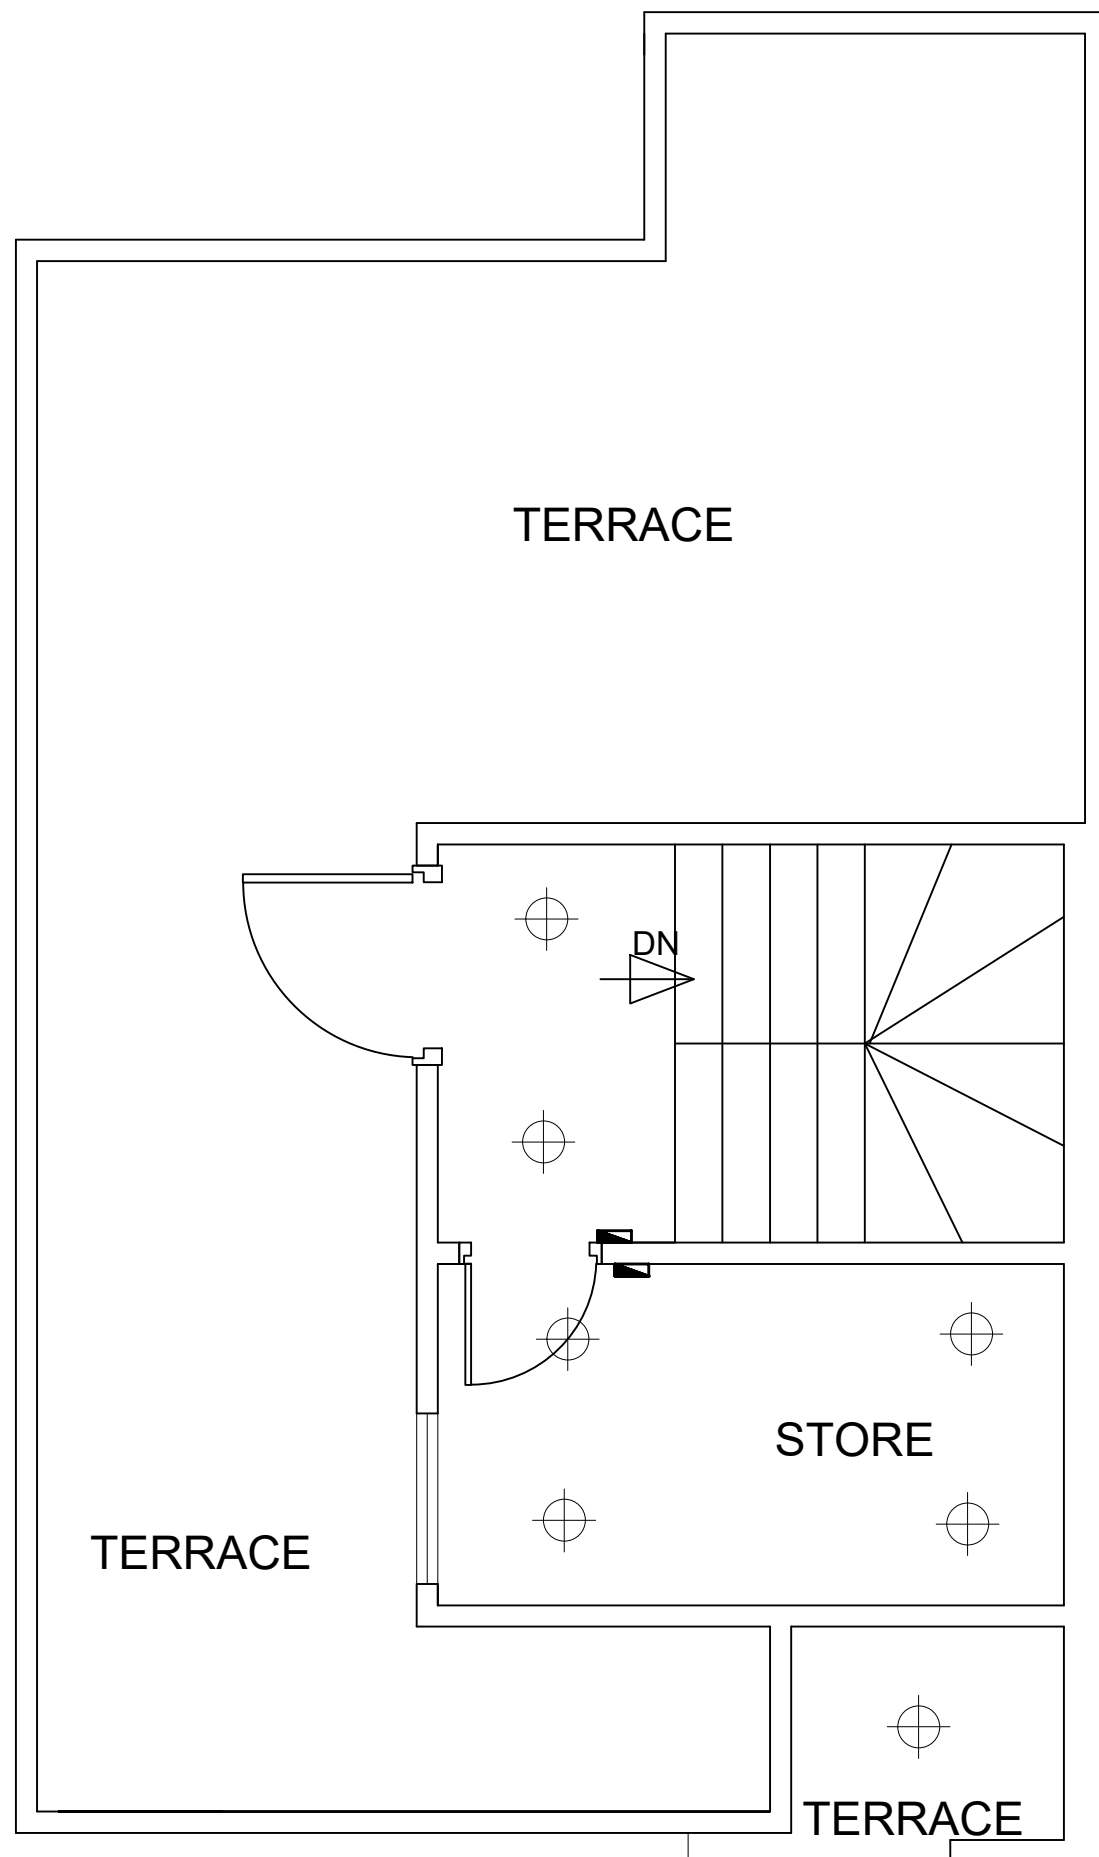


SECOND FLOOR PLAN (ELECTRICAL)
PLOT NO. 16 SIZE - 19'-2"x35'-0"
ALI HOUSING SCHEME



SALMAN AMJAD AND ASSOCIATES:

ARCHITECT, INTERIOR DESIGN, CONSTRUCTION.
APPROVED AS CATEGORY-A ARCHITECT LDA.
REGISTERED PCATP-06011 AND LDA TPRA-298.
OFFICE NO. 35 GROUND FLOOR, MIAN PLAZA.
JOHAR TOWN, LAHORE Mobile no. : 0306-4706139.

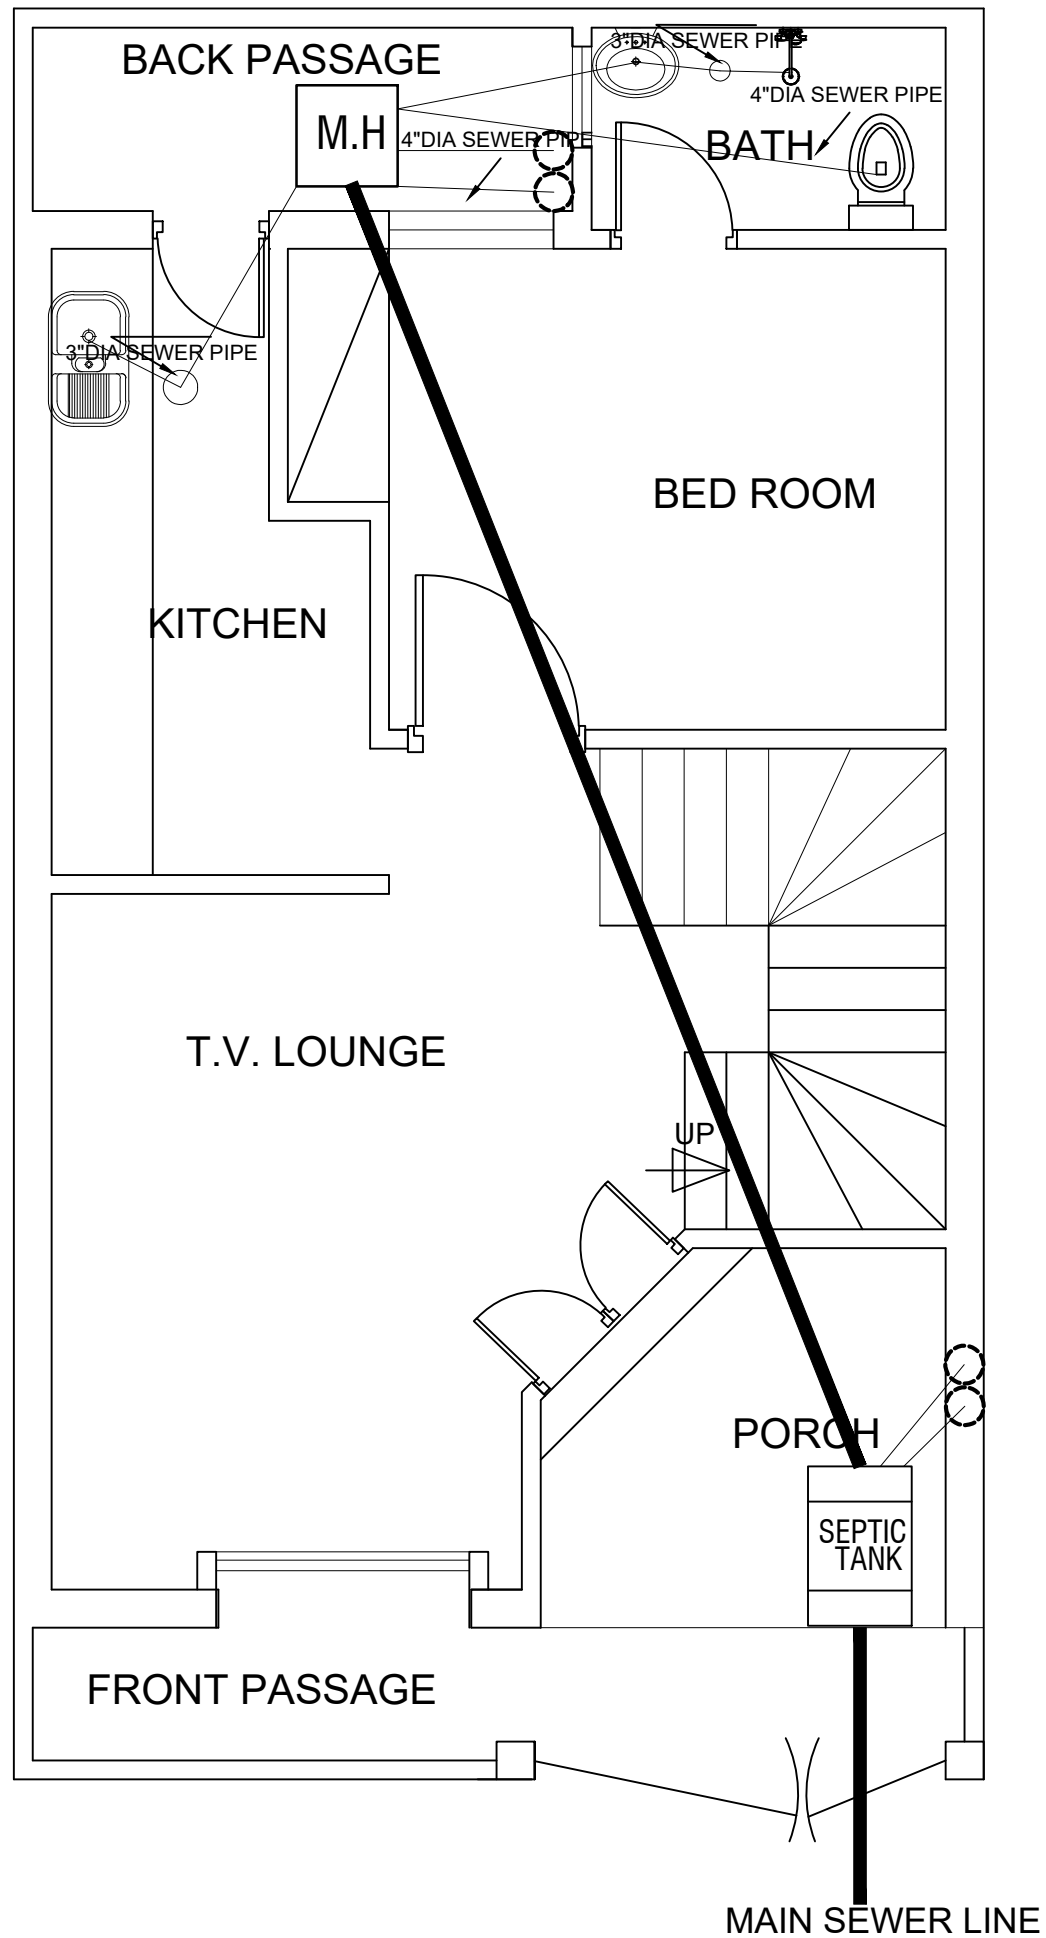


MAIN ENTRANCE

GROUND FLOOR SEWERAGE PLAN
PLOT NO. 16 SIZE - 19'-2"x35'-0"
ALI HOUSING SCHEME



SALMAN AMJAD AND ASSOCIATES:

ARCHITECT, INTERIOR DESIGN, CONSTRUCTION.
APPROVED AS CATEGORY-A ARCHITECT LDA.
REGISTERED PCATP-06011 AND LDA TPRA-298.
OFFICE NO. 35 GROUND FLOOR, MIAN PLAZA.
JOHAR TOWN, LAHORE Mobile no. : 0306-4706139.

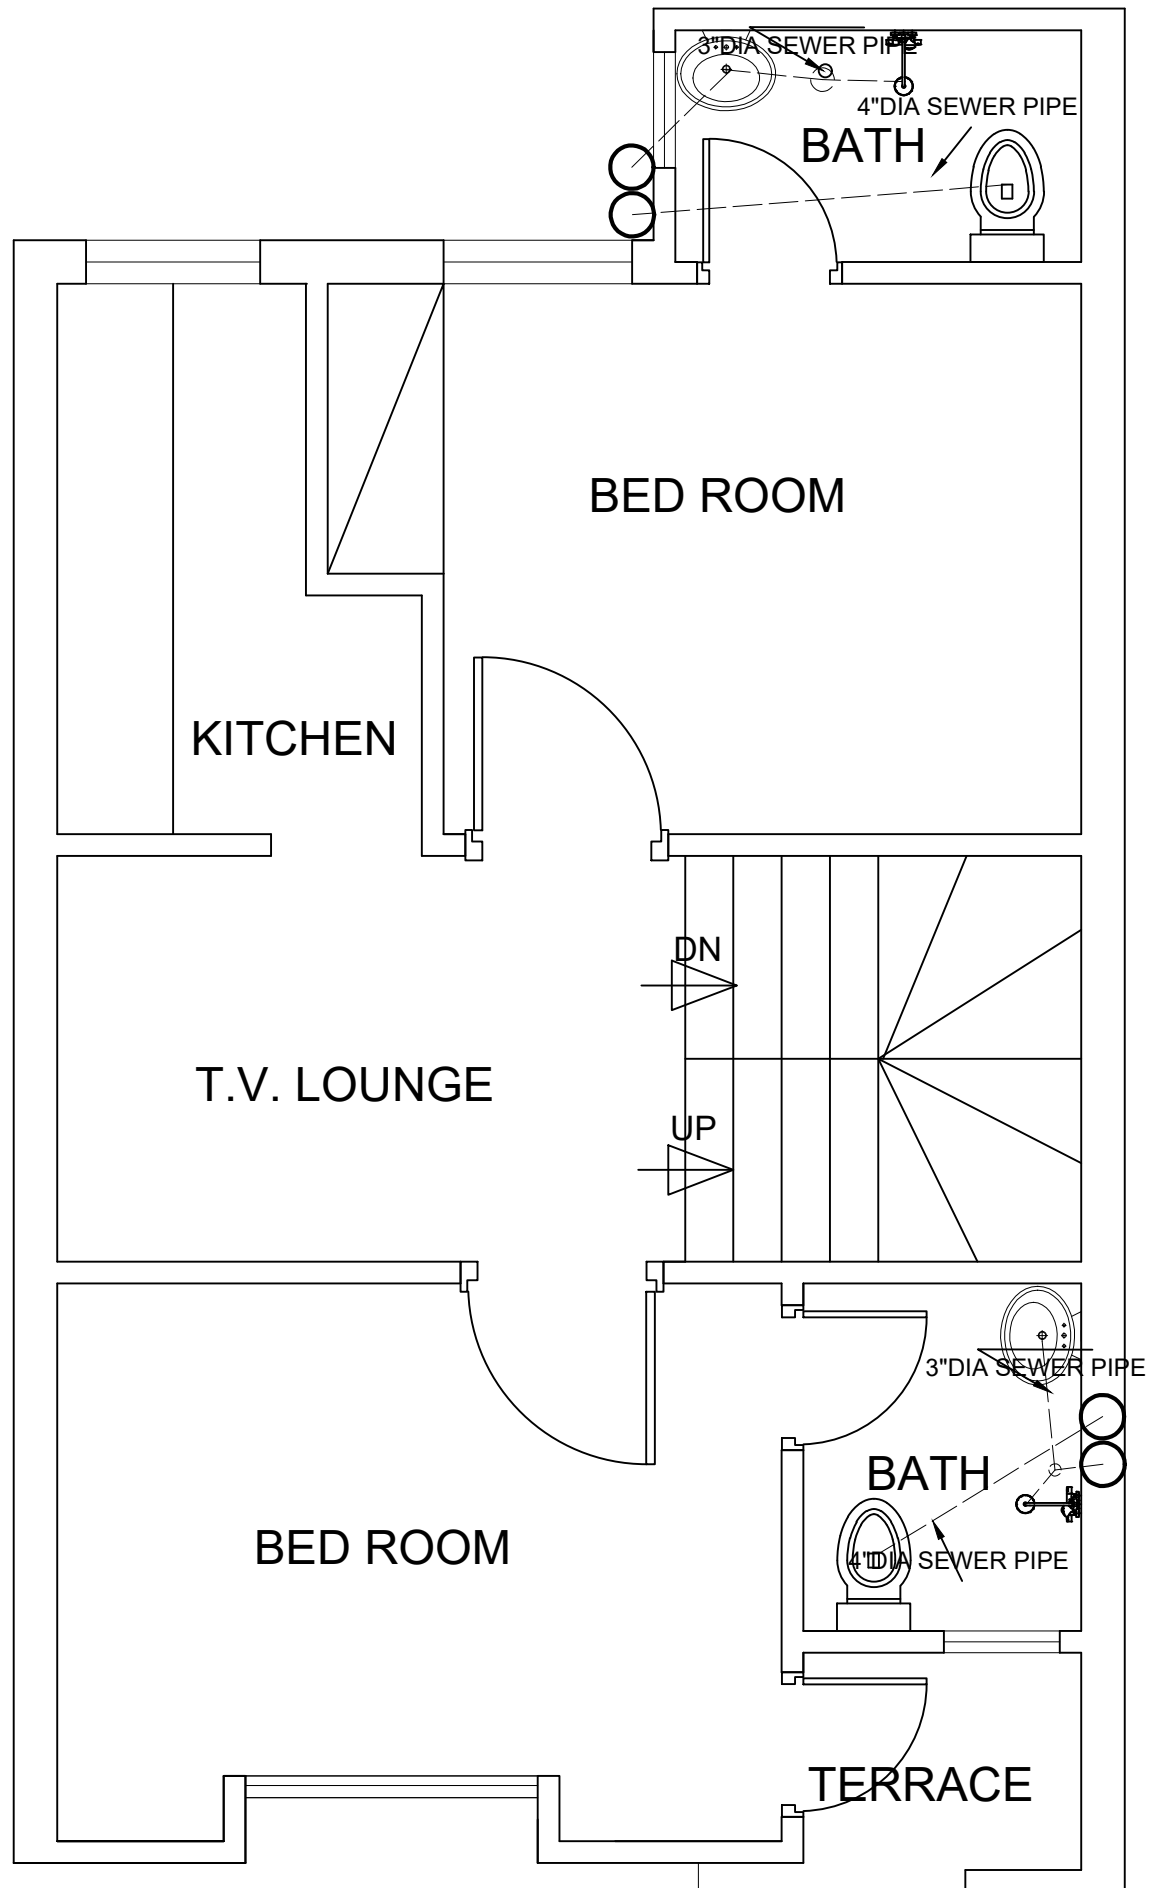


FIRST FLOOR SEWERAGE PLAN
PLOT NO. 16 SIZE - 19'-2"x35'-0"
ALI HOUSING SCHEME



SALMAN AMJAD AND ASSOCIATES:

ARCHITECT, INTERIOR DESIGN, CONSTRUCTION.
APPROVED AS CATEGORY-A ARCHITECT LDA.
REGISTERED PCATP-06011 AND LDA TPRA-298.
OFFICE NO. 35 GROUND FLOOR, MIAN PLAZA.
JOHAR TOWN, LAHORE Mobile no. : 0306-4706139.

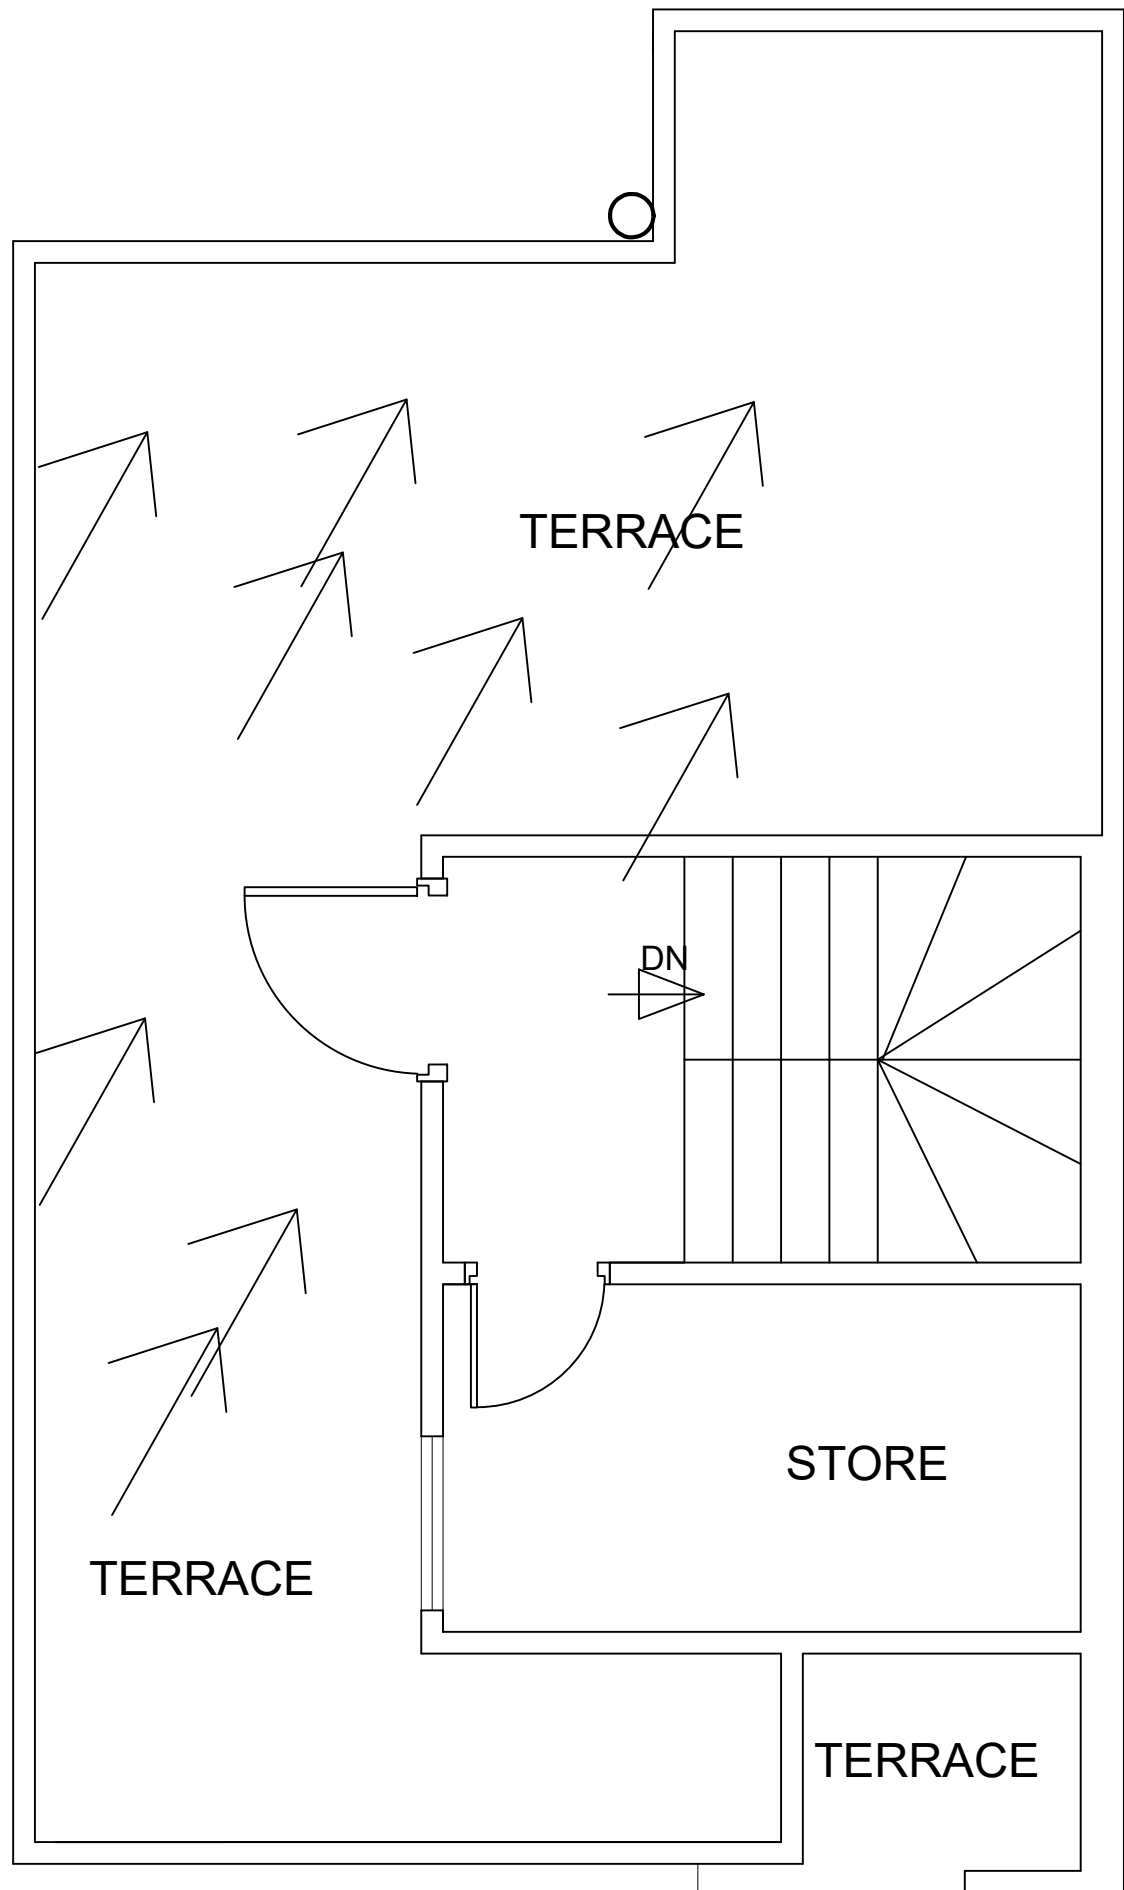


SECOND FLOOR SEWERAGE PLAN
PLOT NO. 16 SIZE - 19'-2"x35'-0"
ALI HOUSING SCHEME



SALMAN AMJAD AND ASSOCIATES:

ARCHITECT, INTERIOR DESIGN, CONSTRUCTION.
APPROVED AS CATEGORY-A ARCHITECT LDA.
REGISTERED PCATP-06011 AND LDA TPRA-298.
OFFICE NO. 35 GROUND FLOOR, MIAN PLAZA.
JOHAR TOWN, LAHORE Mobile no. : 0306-4706139.

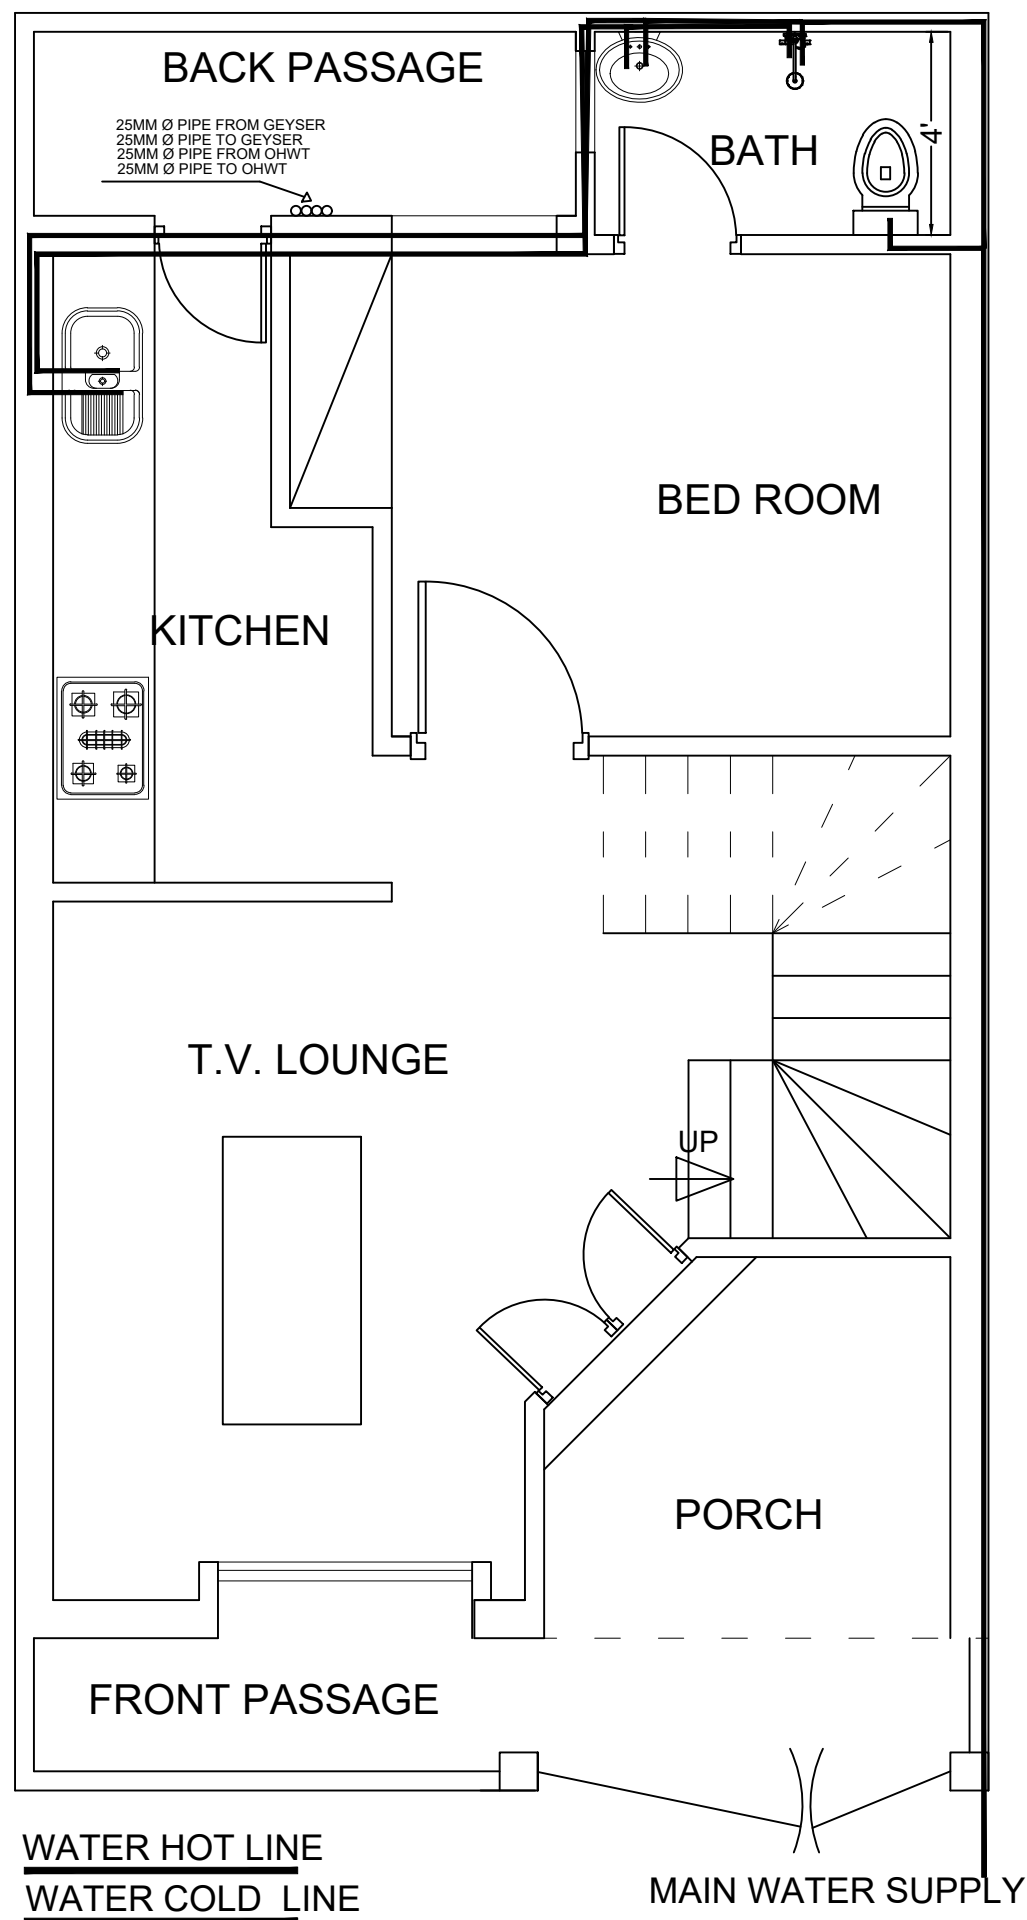


GROUND FLOOR PLUMBING PLAN
PLOT NO. 16 SIZE - 19'-2"x35'-0"
ALI HOUSING SCHEME



SALMAN AMJAD AND ASSOCIATES:

ARCHITECT, INTERIOR DESIGN, CONSTRUCTION.
APPROVED AS CATEGORY-A ARCHITECT LDA.
REGISTERED PCATP-06011 AND LDA TPRA-298.
OFFICE NO. 35 GROUND FLOOR, MIAN PLAZA,
JOHAR TOWN, LAHORE Mobile no. : 0306-4706139.

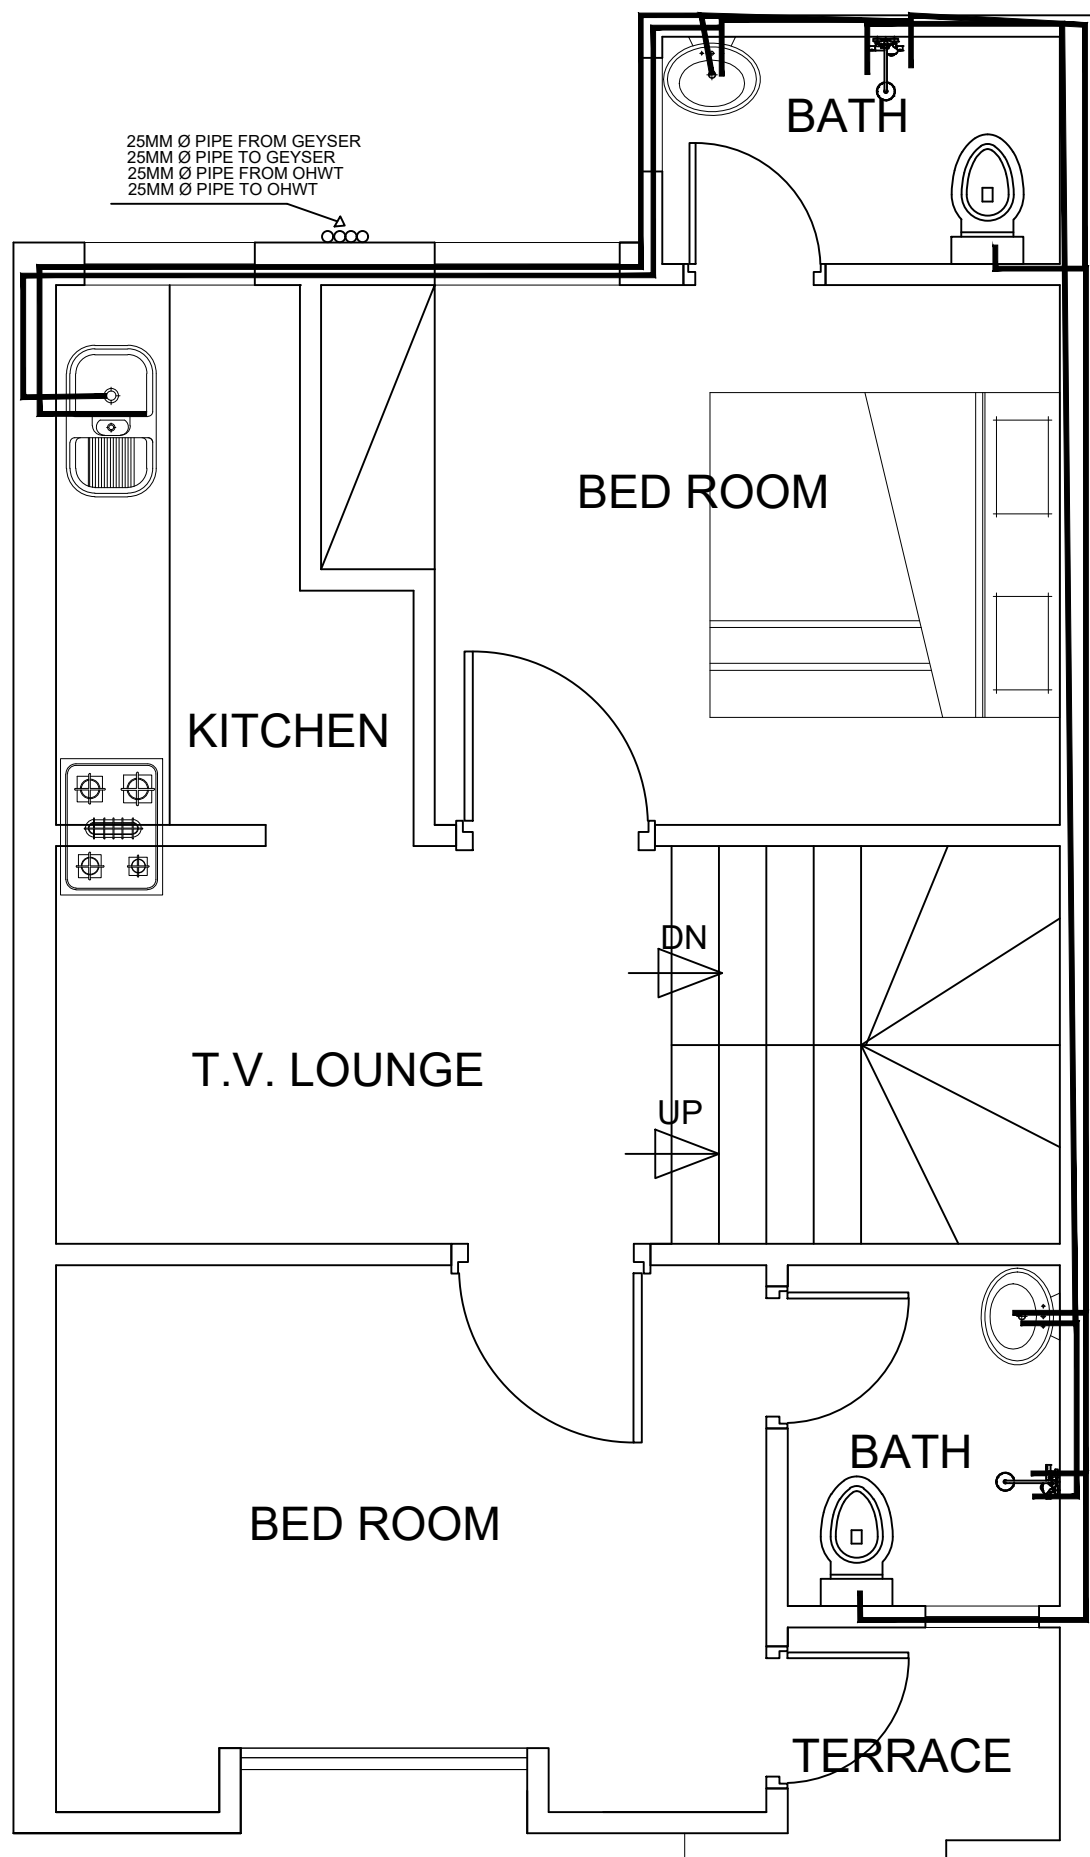


FIRST FLOOR PLUMBING PLAN
PLOT NO. 16 SIZE - 19'-2"x35'-0"
ALI HOUSING SCHEME



SALMAN AMJAD AND ASSOCIATES:

ARCHITECT, INTERIOR DESIGN, CONSTRUCTION.
APPROVED AS CATEGORY-A ARCHITECT LDA.
REGISTERED PCATP-06011 AND LDA TPRA-298.
OFFICE NO. 35 GROUND FLOOR, MIAN PLAZA.
JOHAR TOWN, LAHORE Mobile no. : 0306-4706139.

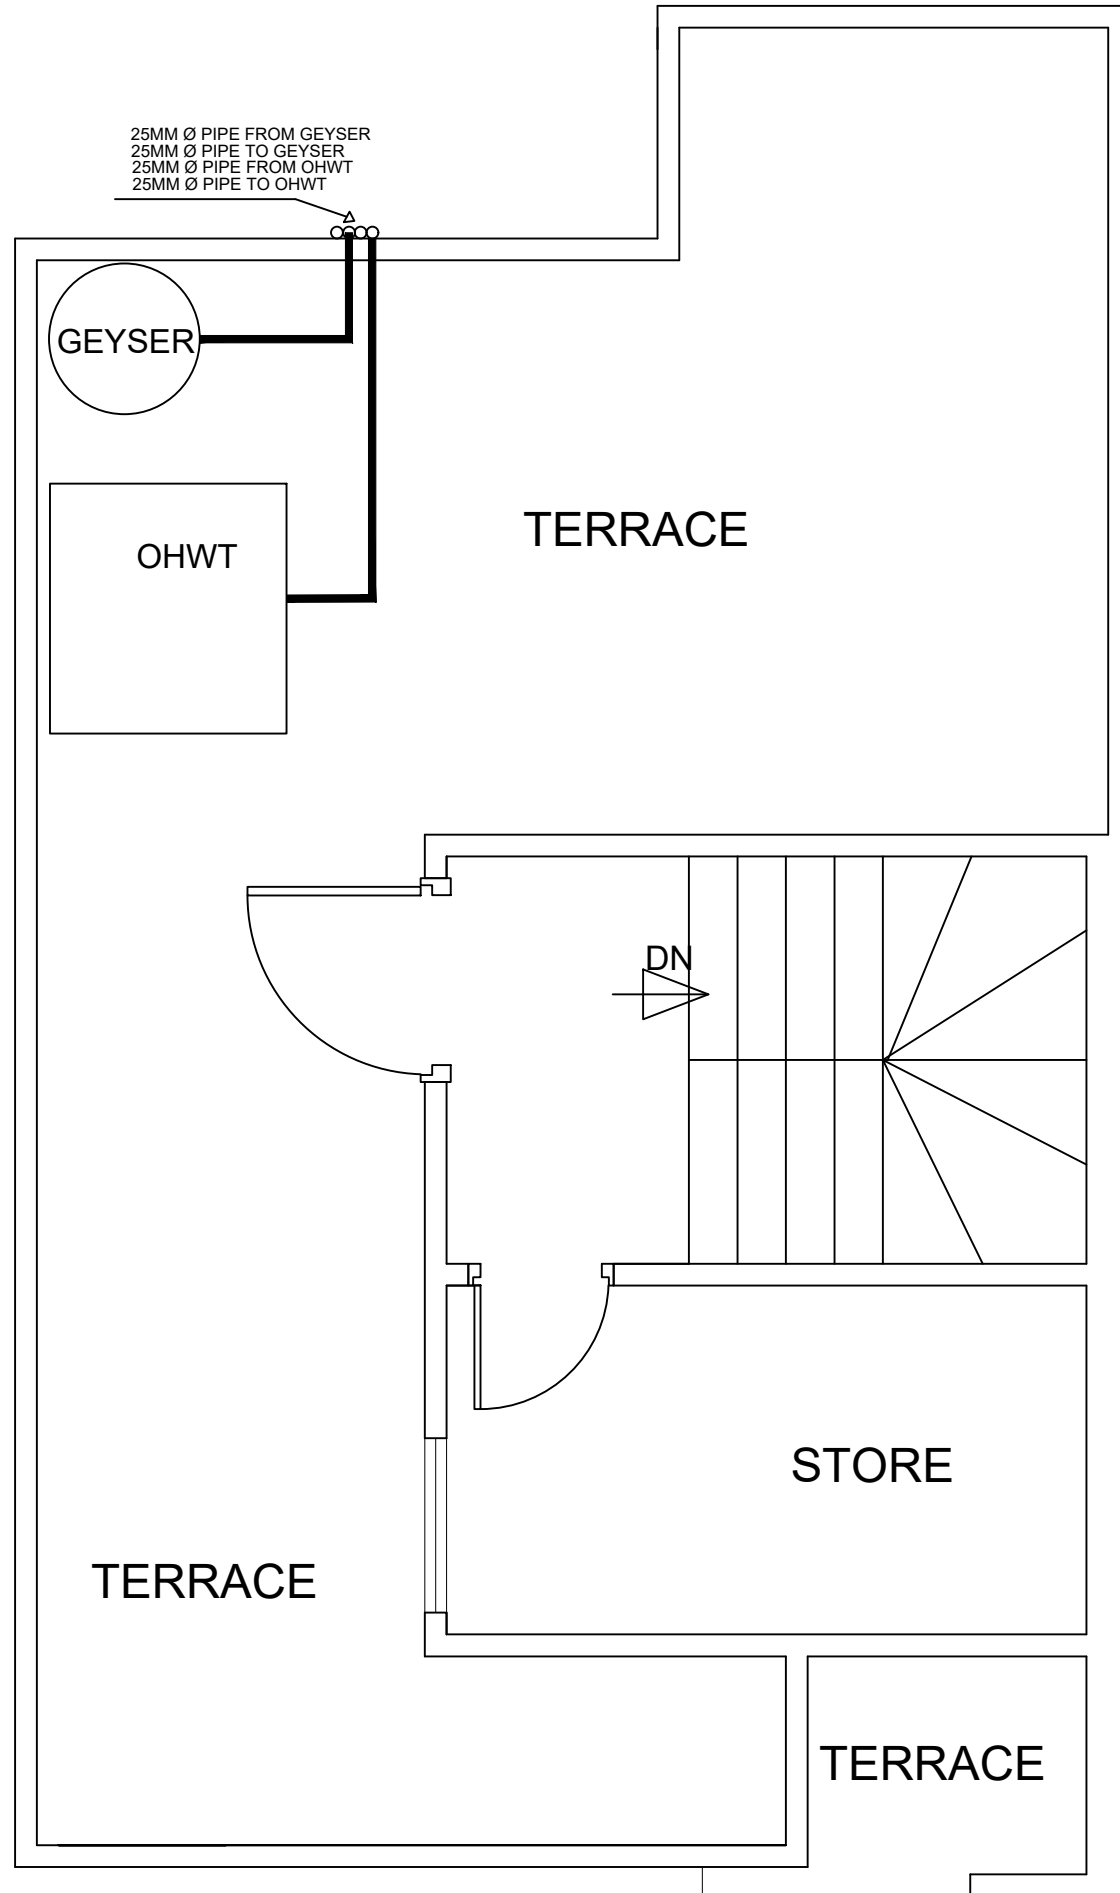


SECOND FLOOR PLUMBING PLAN
 PLOT NO. 16 SIZE - 19'-2"x35'-0"
 ALI HOUSING SCHEME

WATER HOT LINE
WATER COLD LINE



SALMAN AMJAD AND ASSOCIATES:

ARCHITECT, INTERIOR DESIGN, CONSTRUCTION.
 APPROVED AS CATEGORY-A ARCHITECT LDA.
 REGISTERED PCATP-06011 AND LDA TPRA-298.
 OFFICE NO. 35 GROUND FLOOR, MIAN PLAZA.
 JOHAR TOWN, LAHORE Mobile no. : 0306-4706139.

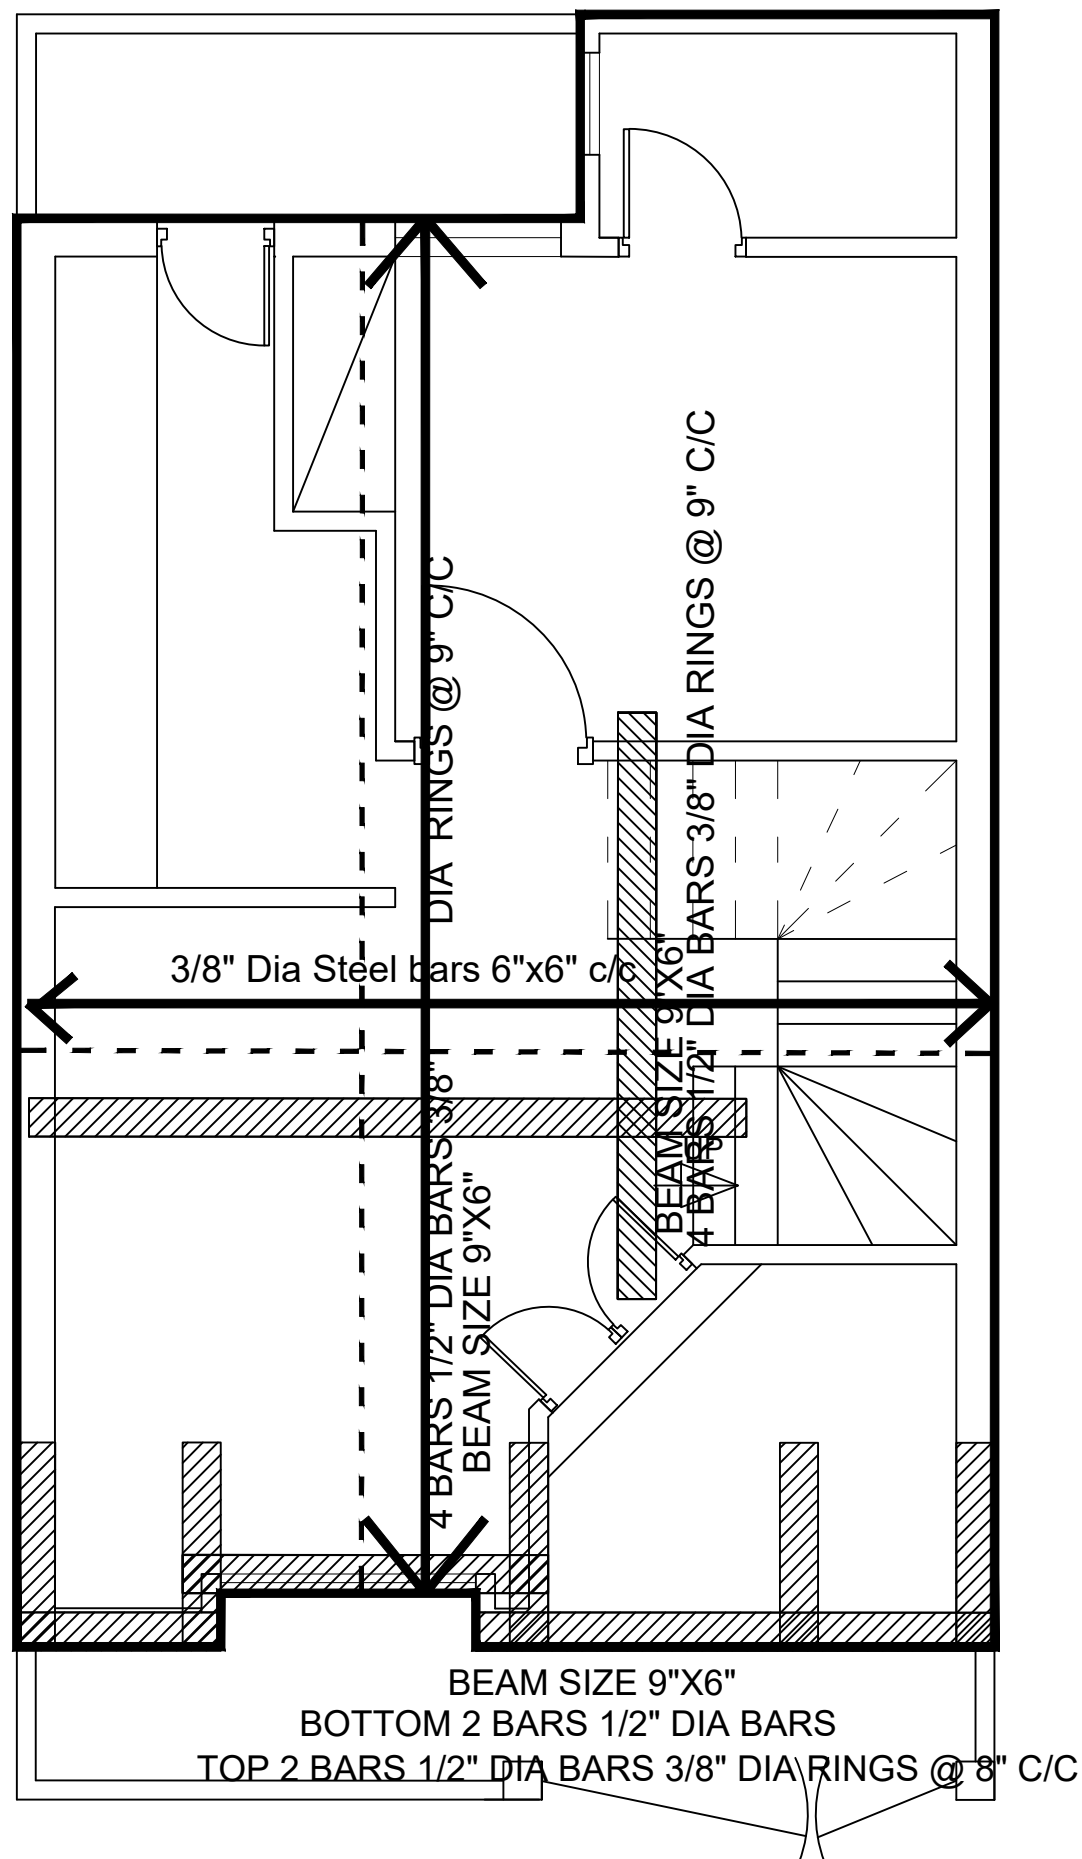


MAIN ENTRANCE

GROUND FLOOR STRUCTRUL PLAN
PLOT NO. 16 SIZE - 19'-2"x35'-0"
ALI HOUSING SCHEME



SALMAN AMJAD AND ASSOCIATES:

ARCHITECT, INTERIOR DESIGN, CONSTRUCTION.
APPROVED AS CATEGORY-A ARCHITECT LDA.
REGISTERED PCATP-06011 AND LDA TPRA-298.
OFFICE NO. 35 GROUND FLOOR, MIAN PLAZA.
JOHAR TOWN, LAHORE Mobile no. : 0306-4706139.

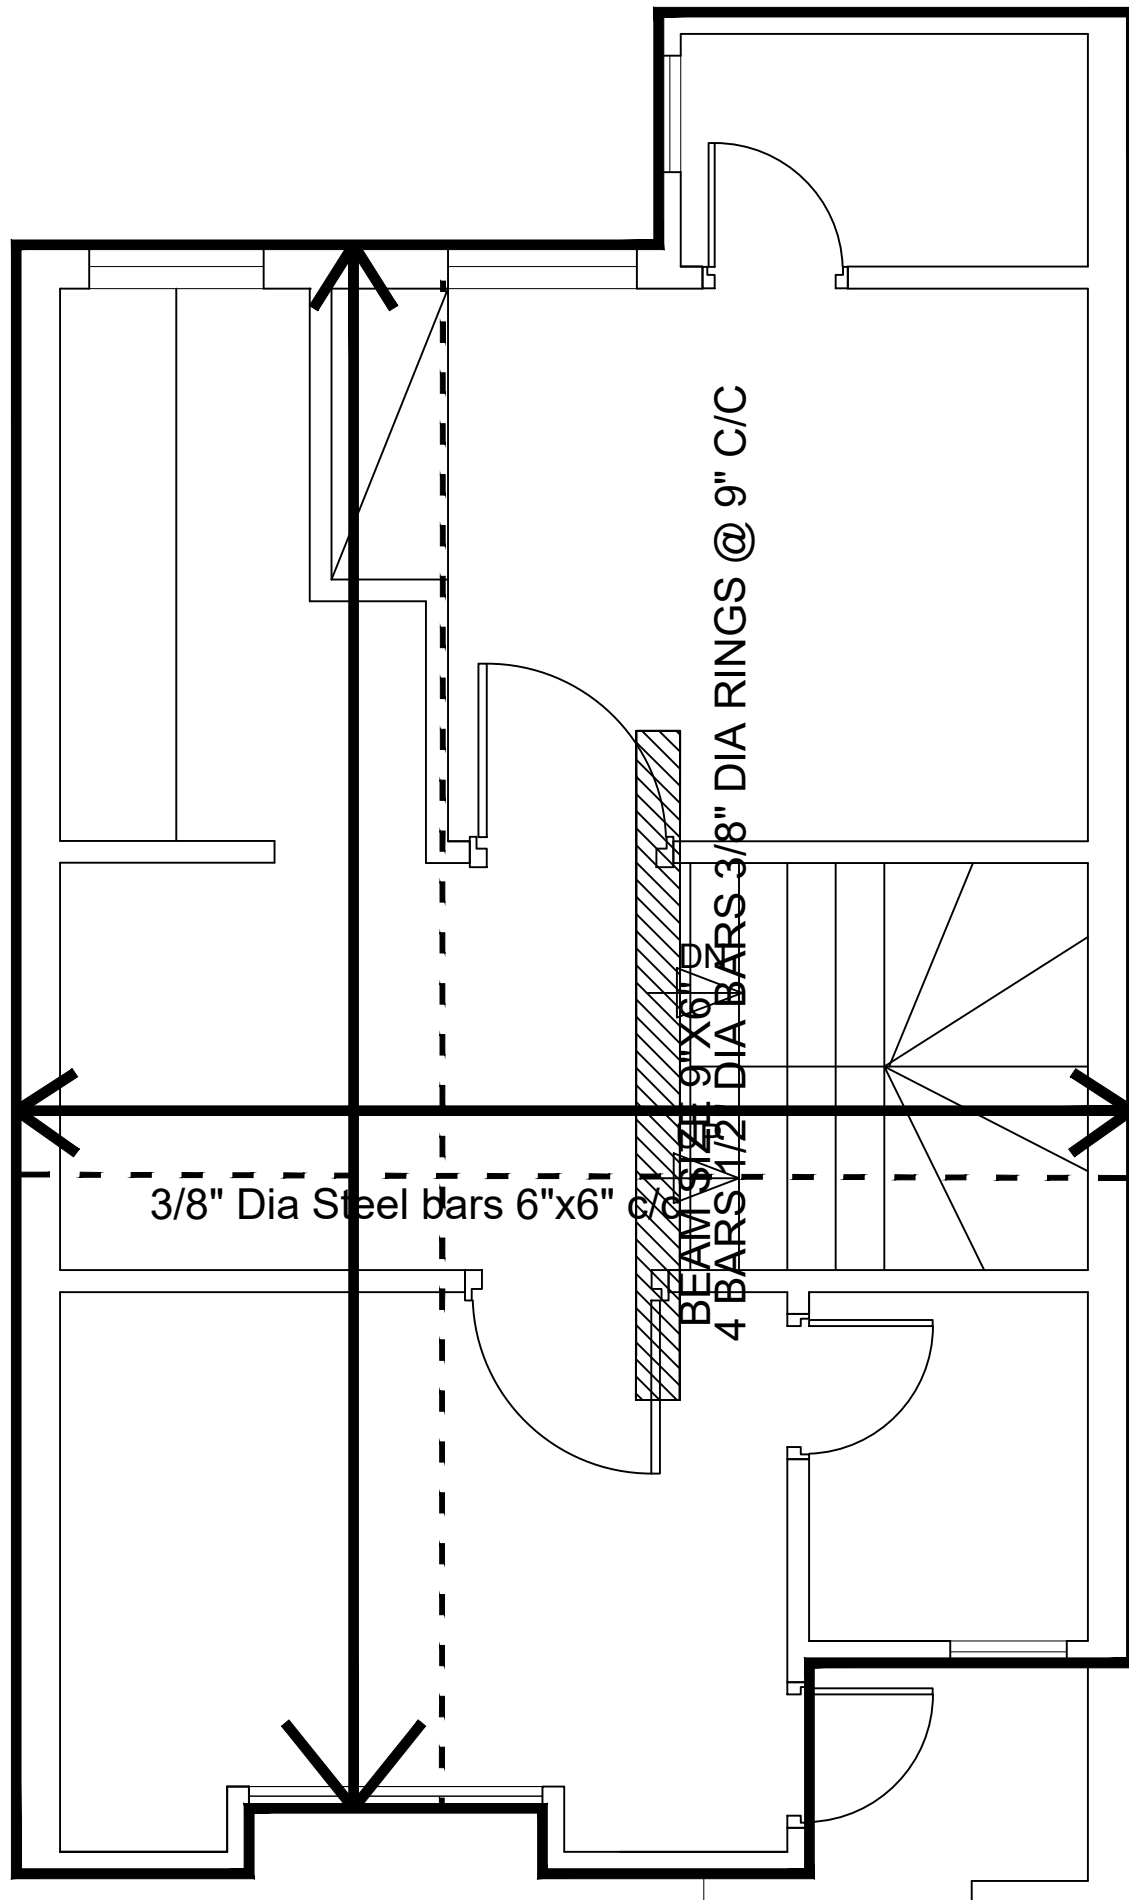


FIRST FLOOR STRUCTRUL PLAN
 PLOT NO. 16 SIZE - 19'-2"x35'-0"
 ALI HOUSING SCHEME



SALMAN AMJAD AND ASSOCIATES:

ARCHITECT, INTERIOR DESIGN, CONSTRUCTION.
 APPROVED AS CATEGORY-A ARCHITECT LDA.
 REGISTERED PCATP-06011 AND LDA TPRA-298.
 OFFICE NO. 35 GROUND FLOOR, MIAN PLAZA.
 JOHAR TOWN, LAHORE Mobile no. : 0306-4706139.

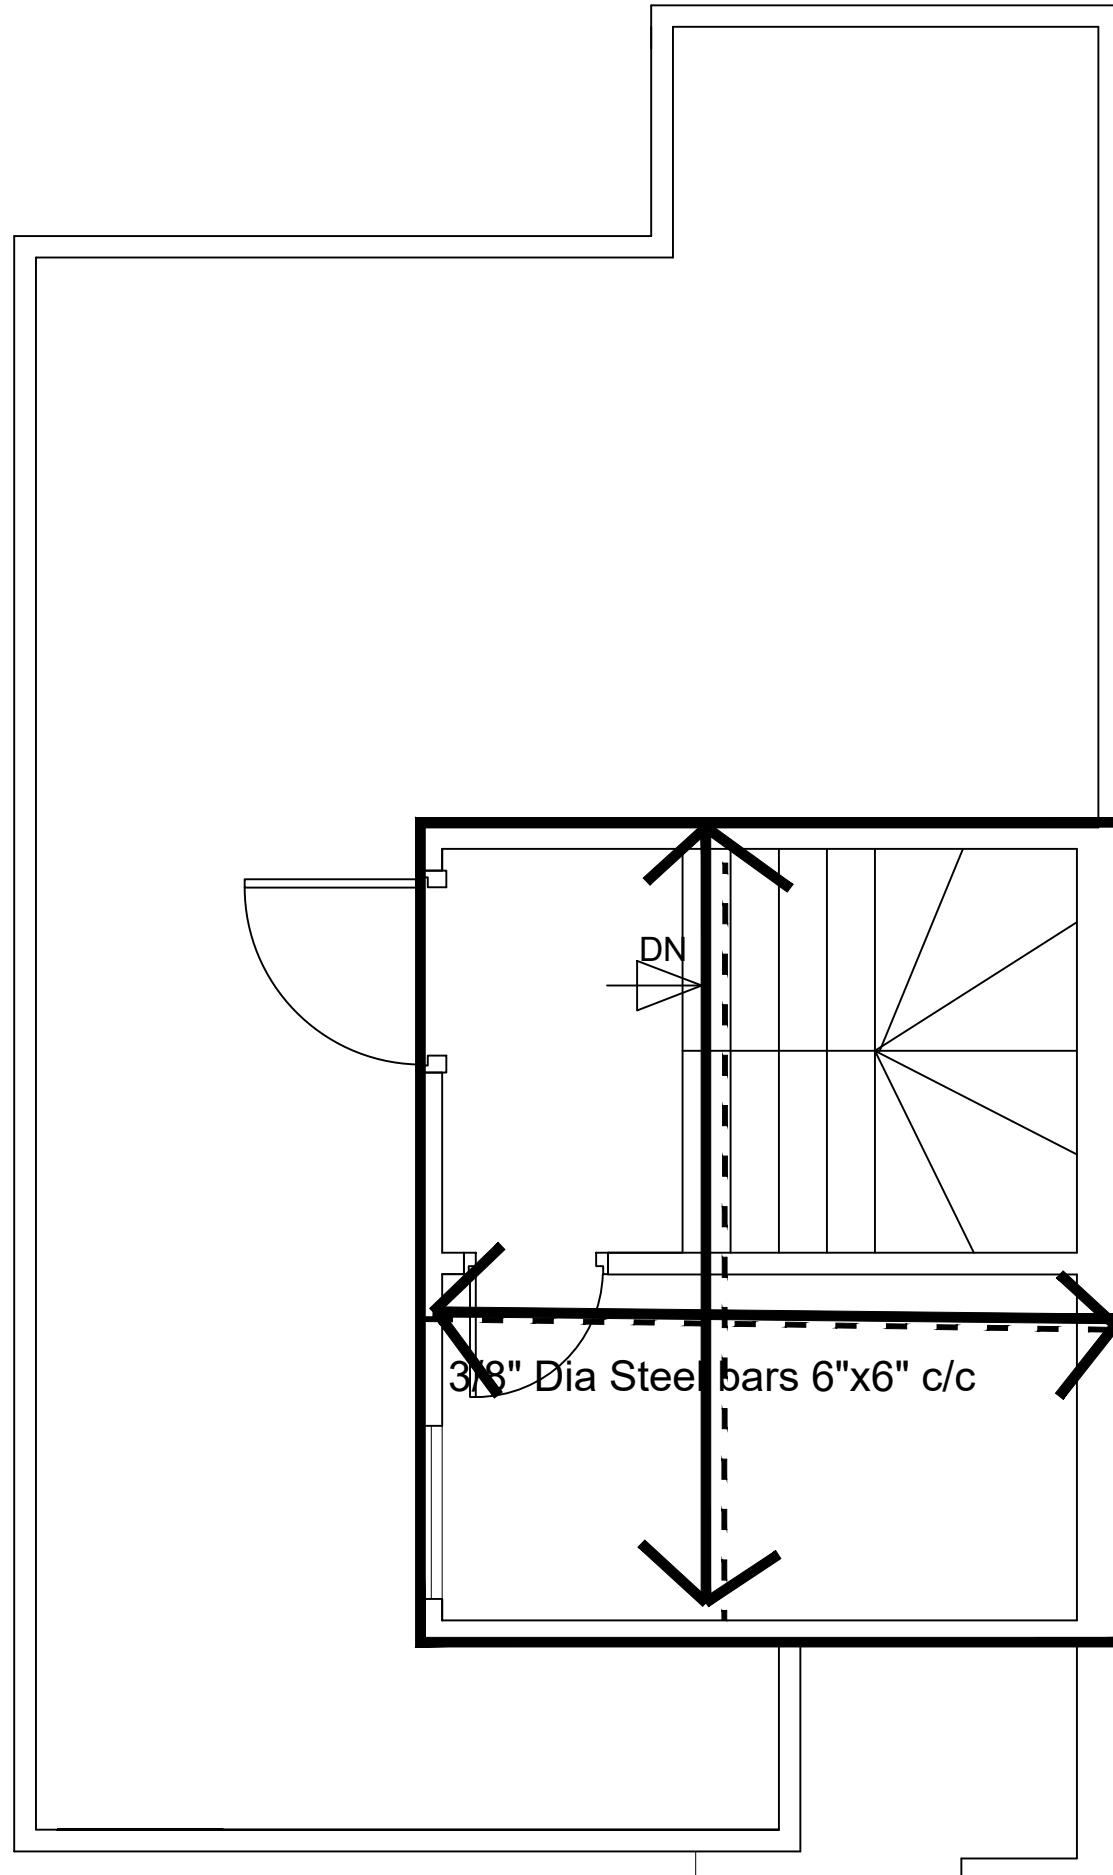

SECOND FLOOR STRUCTRUL PLAN
PLOT NO. 16 SIZE - 19'-2"x35'-0"
ALI HOUSING SCHEME



SALMAN AMJAD AND ASSOCIATES:

ARCHITECT, INTERIOR DESIGN, CONSTRUCTION.
APPROVED AS CATEGORY-A ARCHITECT LDA.
REGISTERED PCATP-06011 AND LDA TPRA-298.
OFFICE NO. 35 GROUND FLOOR, MIAN PLAZA.
JOHAR TOWN, LAHORE Mobile no. : 0306-4706139.