


GROUND FLOOR
 SOHAIL RASHID
 HASSAN BLOCK
 PLOT NO 12 22'-6"x40'
 ALI HOUSING SCHEME, LAHORE

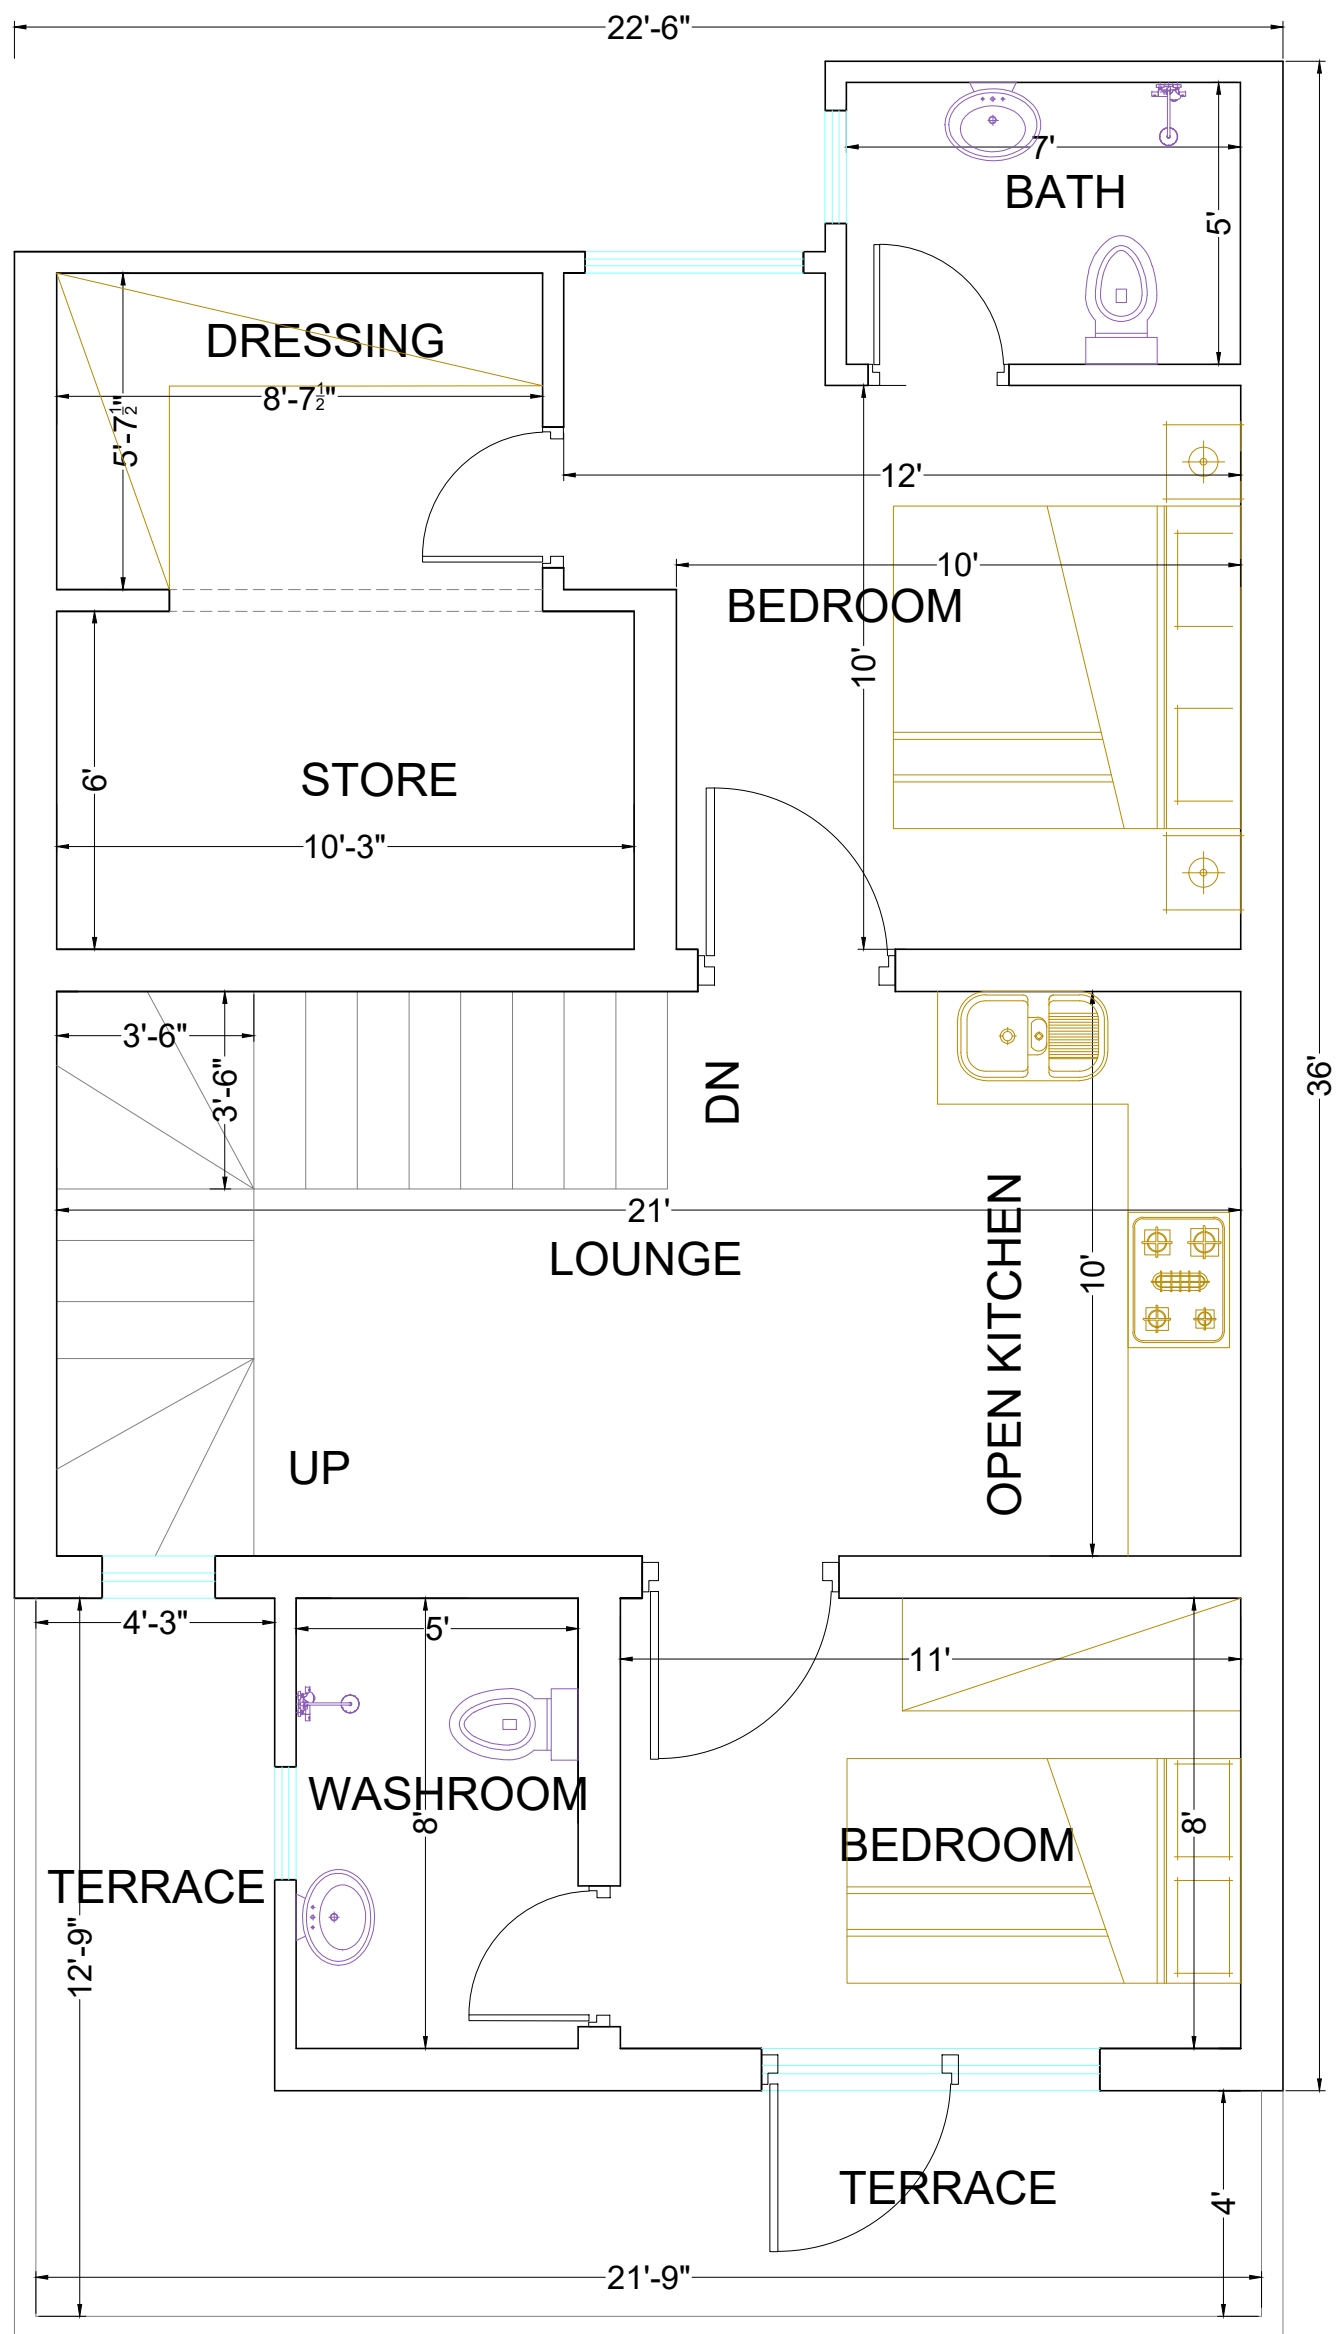

SALMAN AMJAD AND ASSOCIATES:

APPROVED AS CATEGORY-A ARCHITECT LDA.
 REGISTERED PCATP-06011 AND LDA TPRA-298
 OFFICE NO. FIRST FLOOR, MUSTAFA TOWN,
 HIDAYATULLAH STREET, LAHORE
 MOBILE NO → 0306-4706139




FIRST FLOOR
SOHAIL RASHID
HASSAN BLOCK
PLOT NO 12 22'-6"x40'
ALI HOUSING SCHEME, LAHORE



SALMAN AMJAD AND ASSOCIATES:

APPROVED AS CATEGORY-A ARCHITECT LDA.
 REGISTERED PCATP-06011 AND LDA TPRA-298
 OFFICE NO. FIRST FLOOR, MUSTAFA TOWN,
 HIDAYATULLAH STREET, LAHORE
 MOBILE NO → 0306-4706139

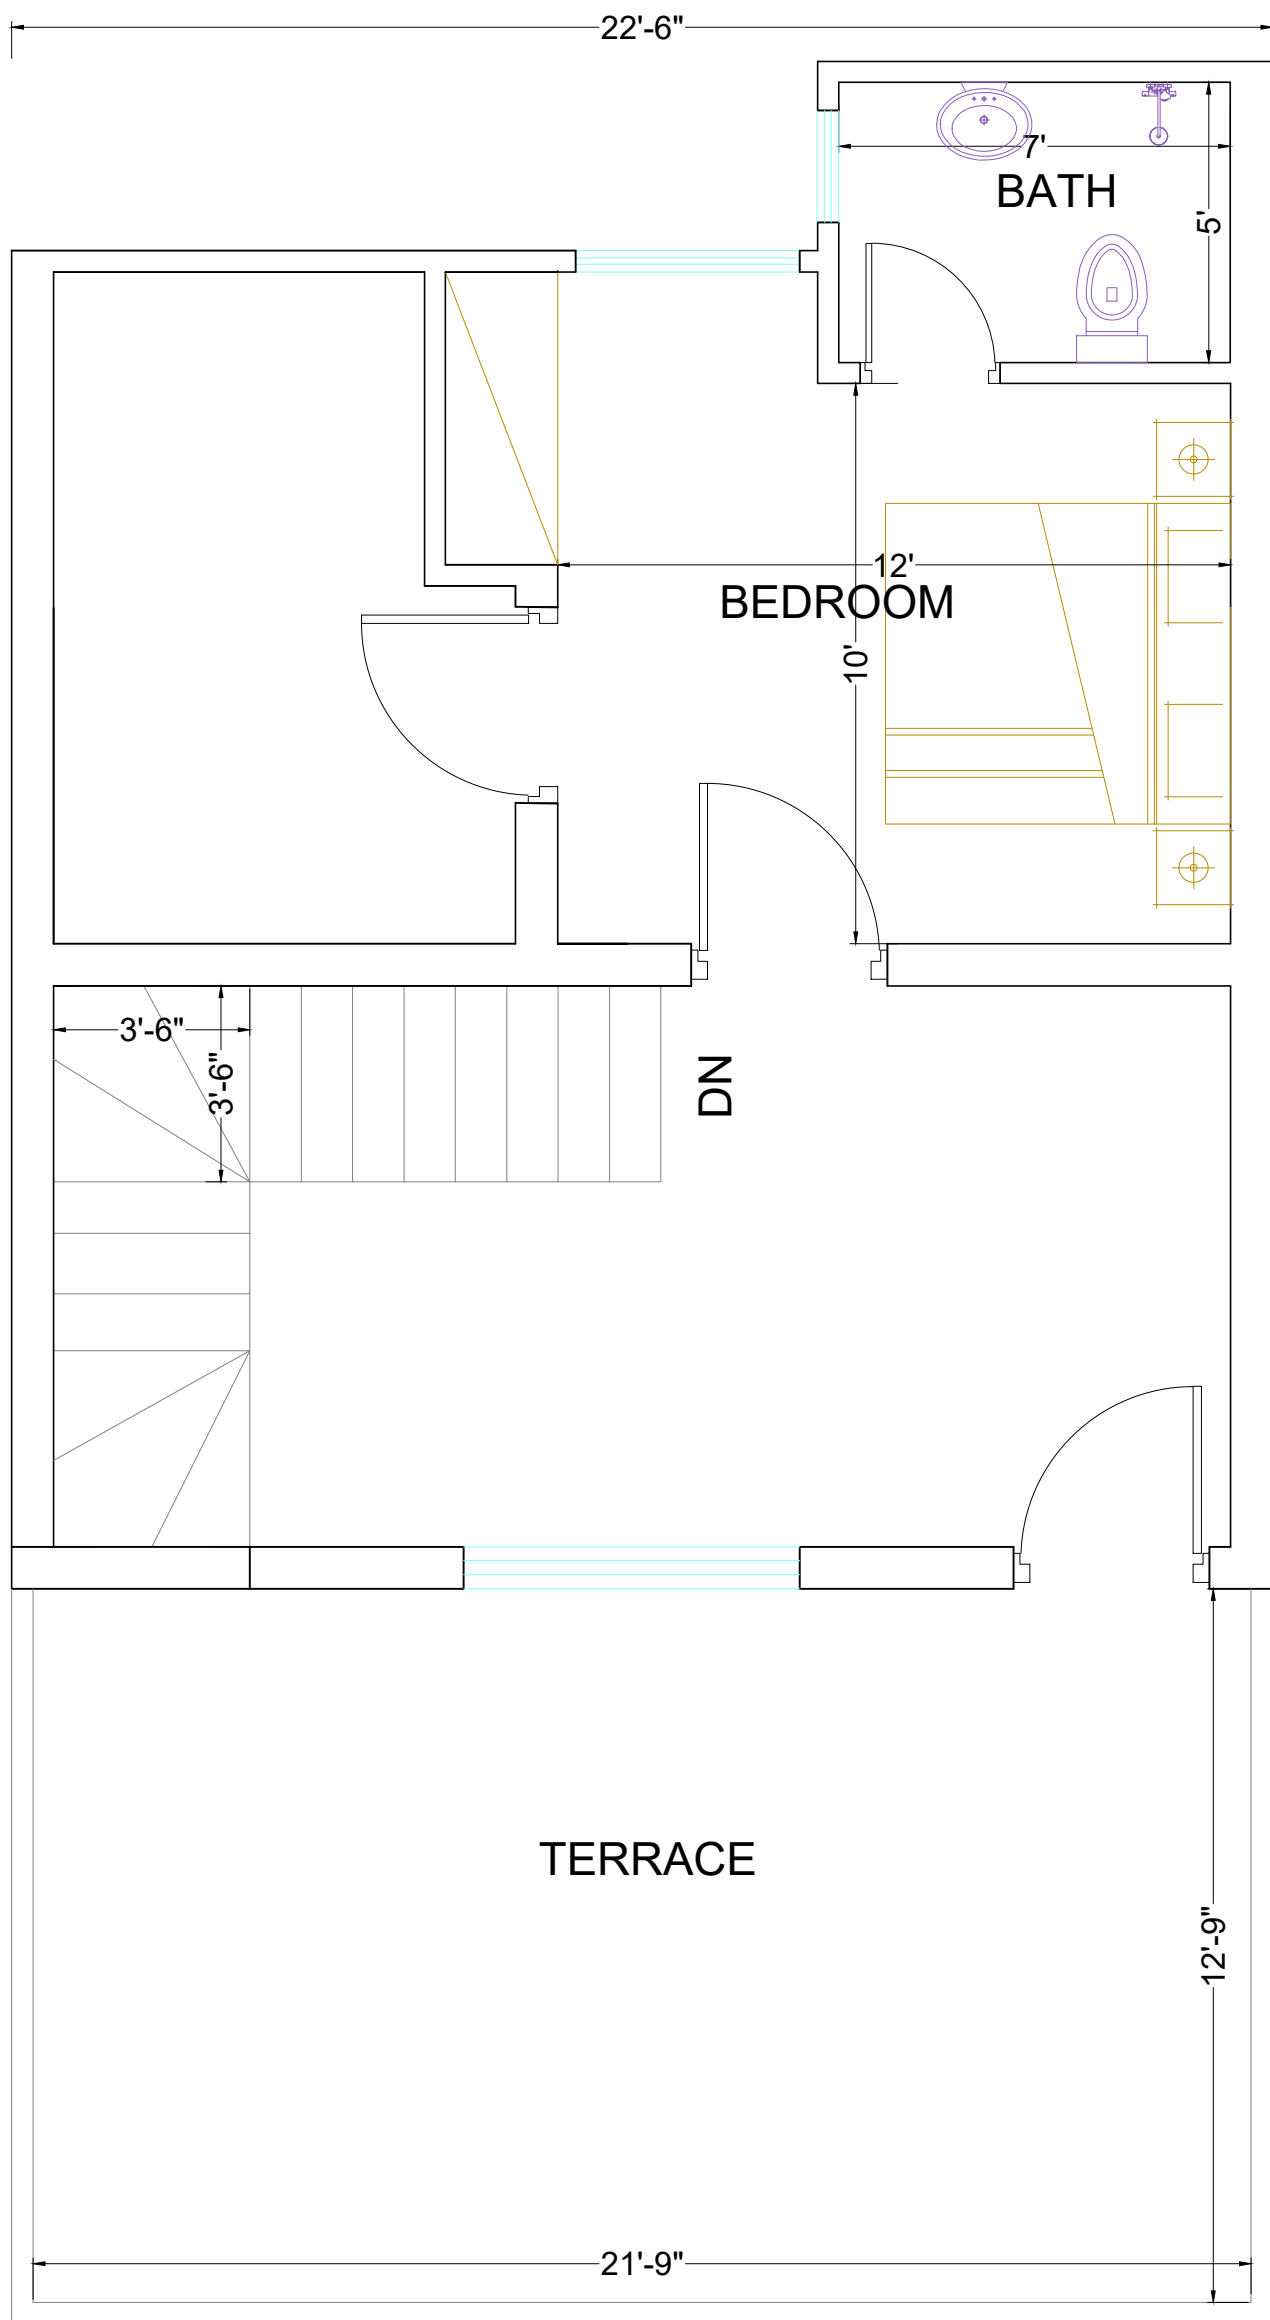


SECOND FLOOR
SOHAIL RASHID
HASSAN BLOCK
PLOT NO 12 22'-6"x40'
ALI HOUSING SCHEME, LAHORE




SALMAN AMJAD AND ASSOCIATES:

APPROVED AS CATEGORY-A ARCHITECT LDA.
REGISTERED PCATP-06011 AND LDA TPRA-298
OFFICE NO. FIRST FLOOR, MUSTAFA TOWN,
HIDAYATULLAH STREET, LAHORE
MOBILE NO → 0306-4706139

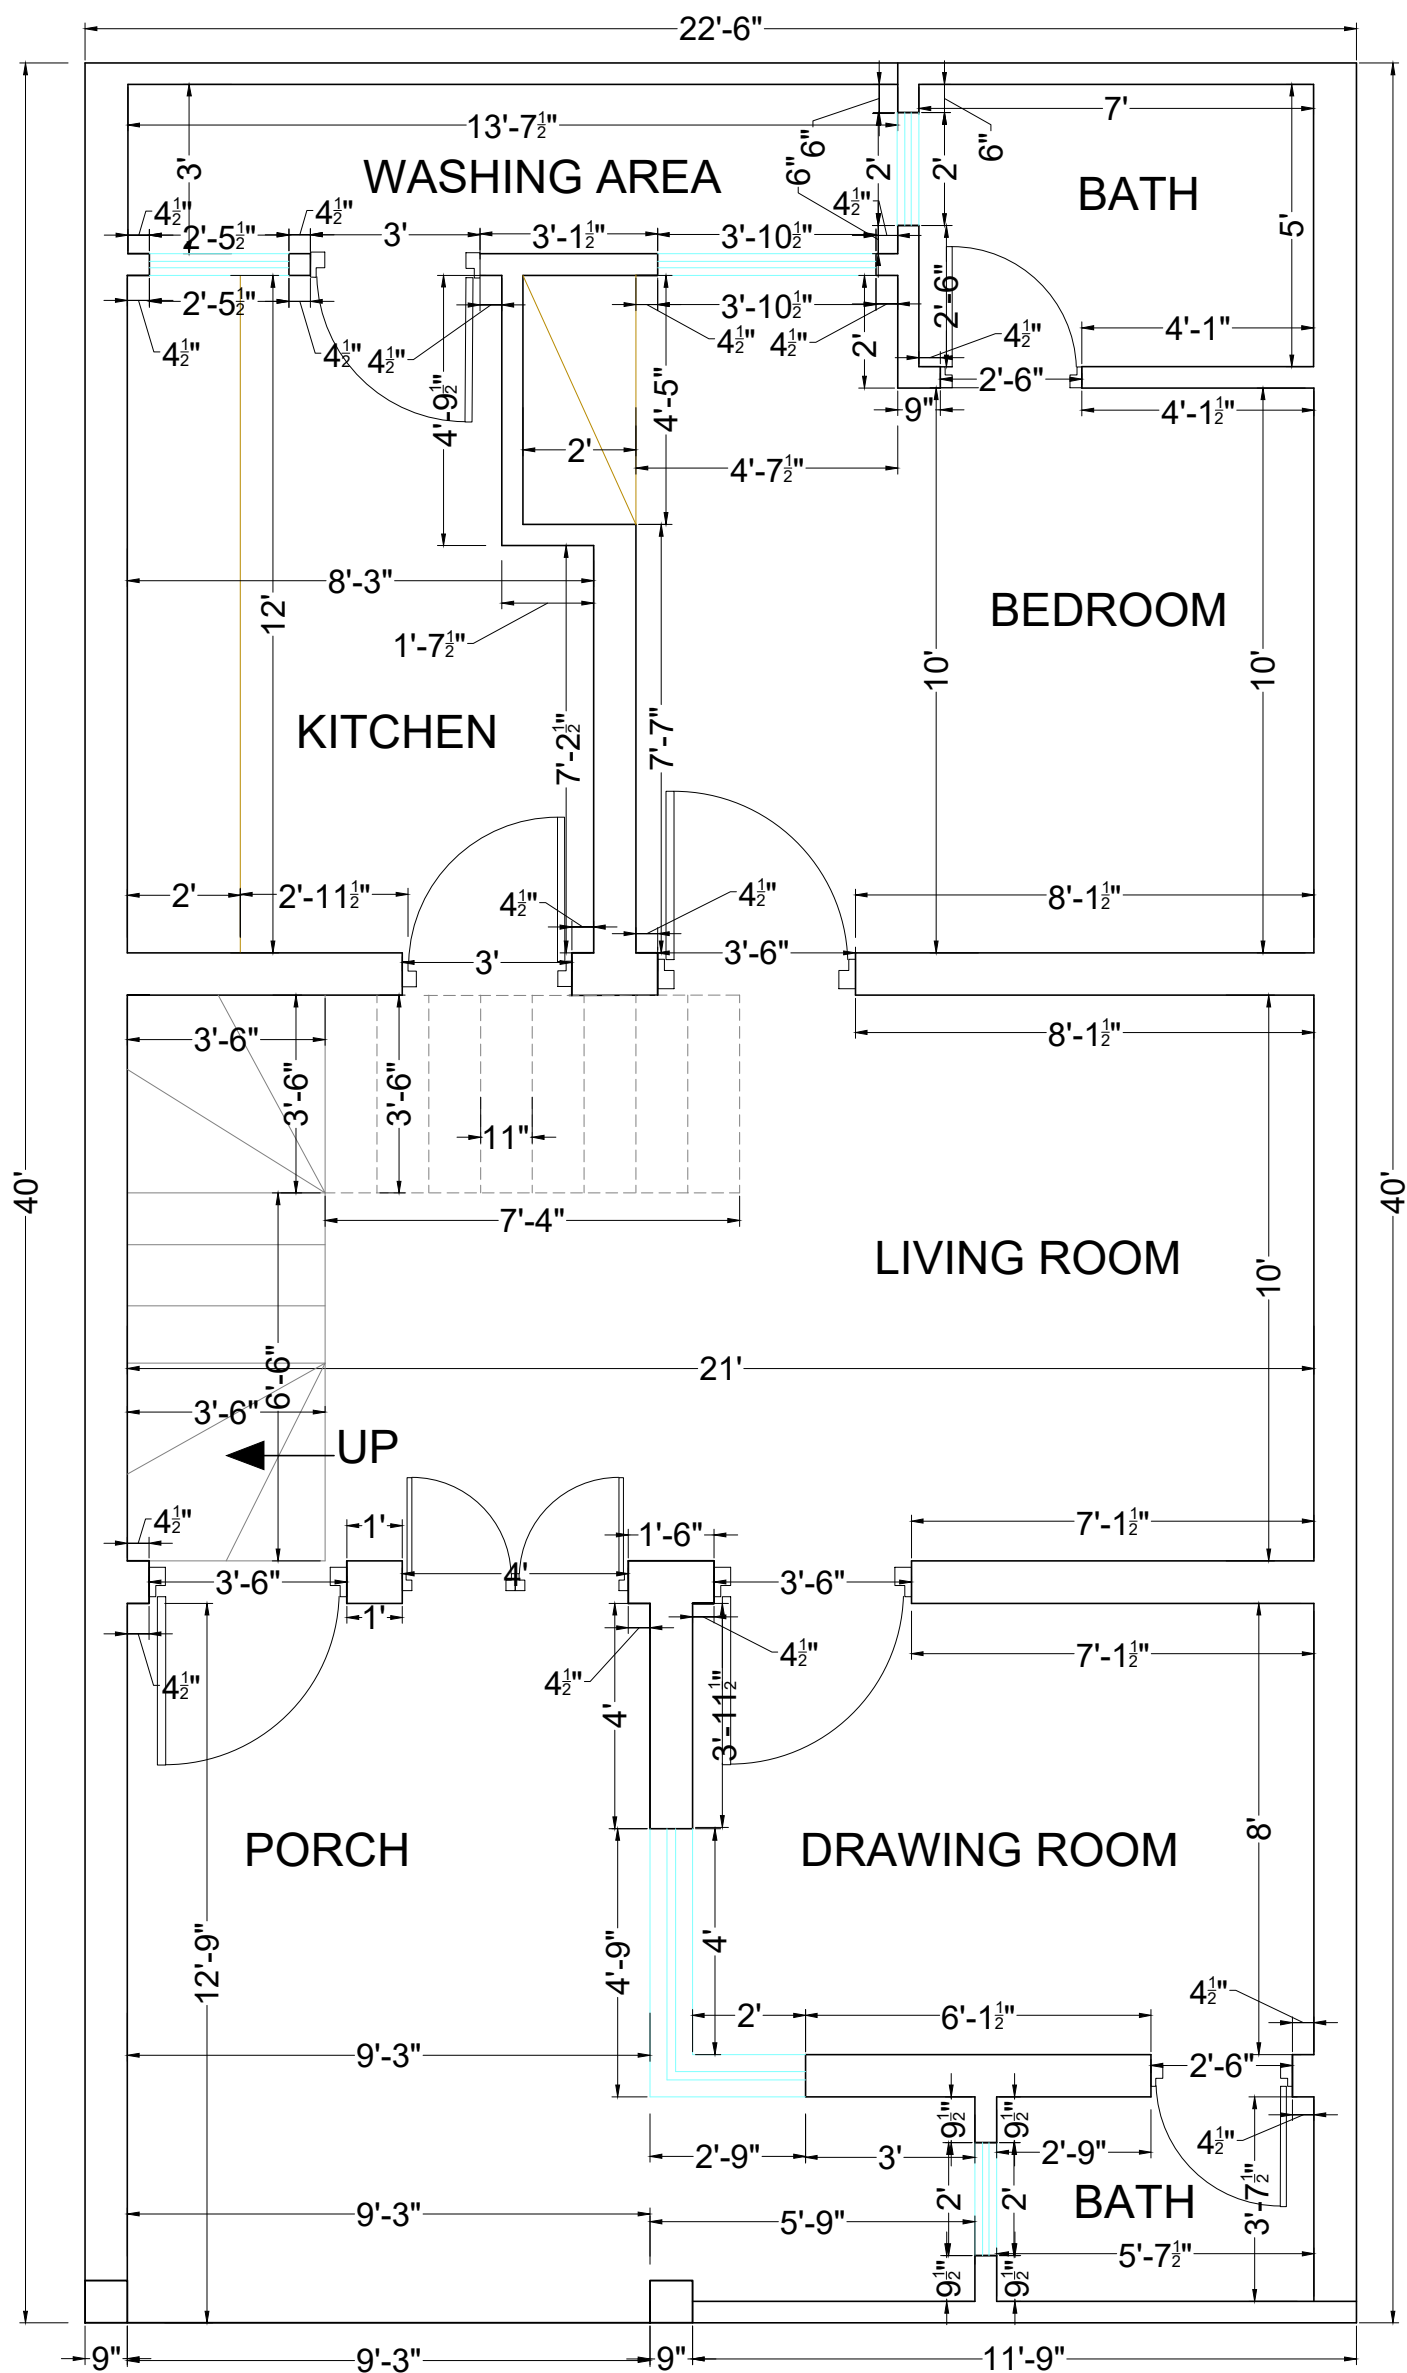

SALMAN AMJAD AND ASSOCIATES:

APPROVED AS CATEGORY-A ARCHITECT LDA.
 REGISTERED PCATP-06011 AND LDA TPRA-298
 OFFICE NO. FIRST FLOOR, MUSTAFA TOWN,
 HIDAYATULLAH STREET, LAHORE
 MOBILE NO → 0306-4706139

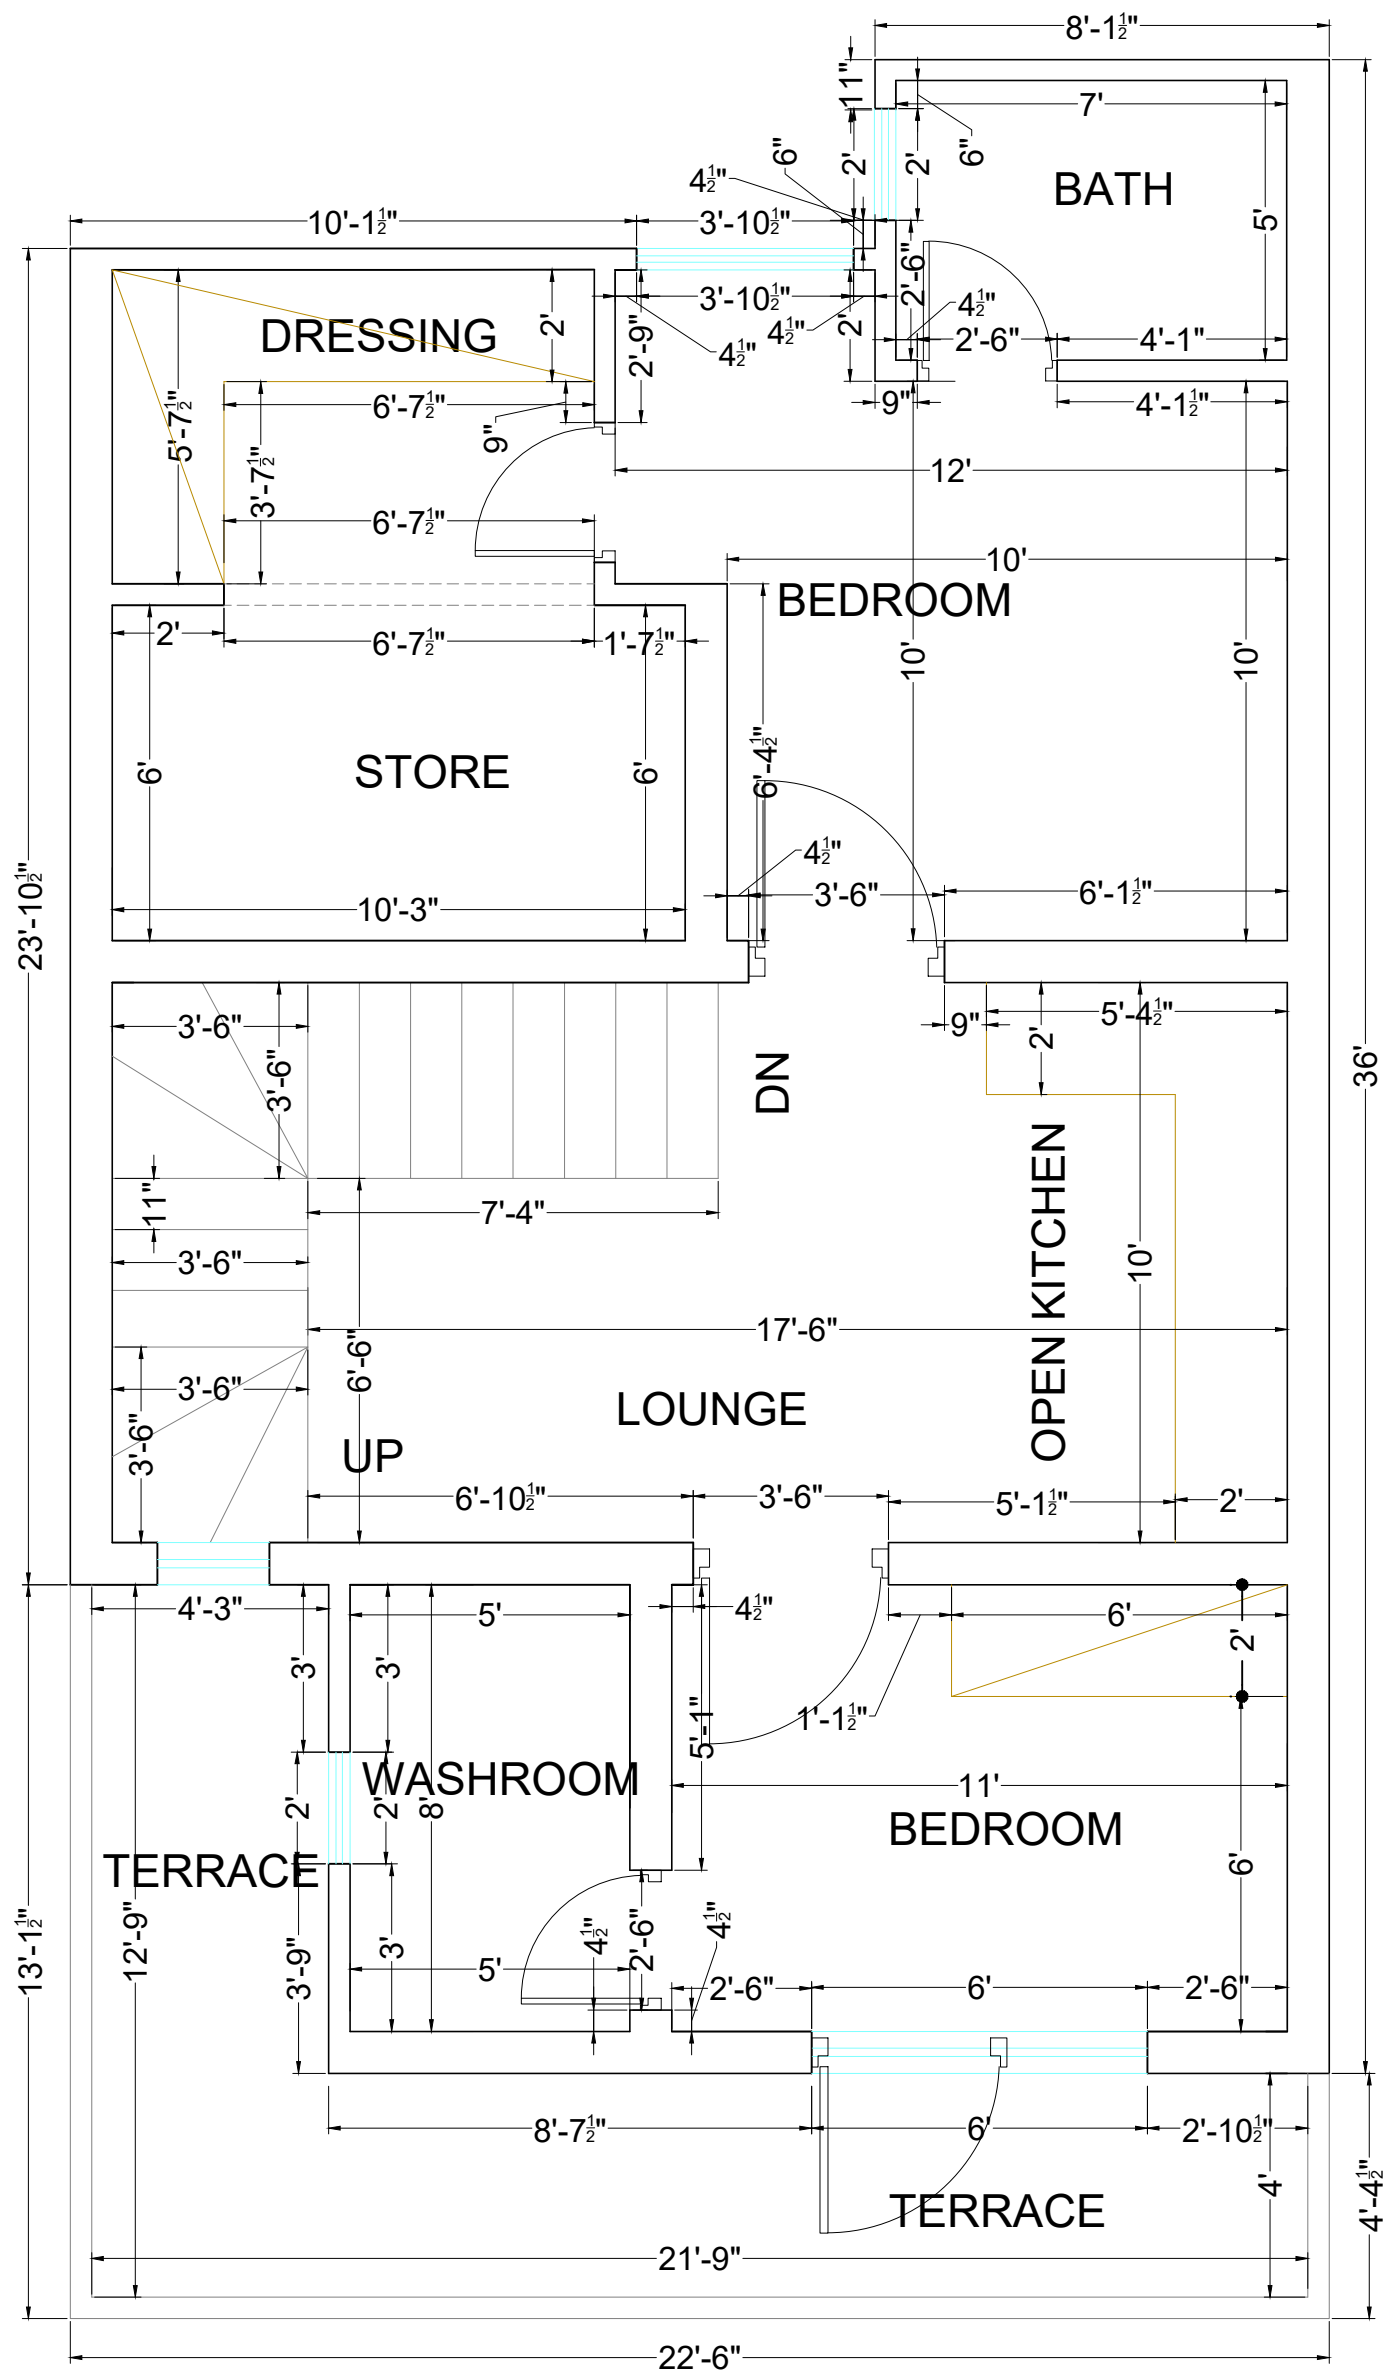


WORKING FIRST FLOOR
SOHAIL RASHID
HASSAN BLOCK
PLOT NO 12 22'-6"x40'
ALI HOUSING SCHEME, LAHORE



SALMAN AMJAD AND ASSOCIATES:

APPROVED AS CATEGORY-A ARCHITECT LDA.
 REGISTERED PCATP-06011 AND LDA TPRA-298
 OFFICE NO. FIRST FLOOR, MUSTAFA TOWN,
 HIDAYATULLAH STREET, LAHORE
 MOBILE NO → 0306-4706139


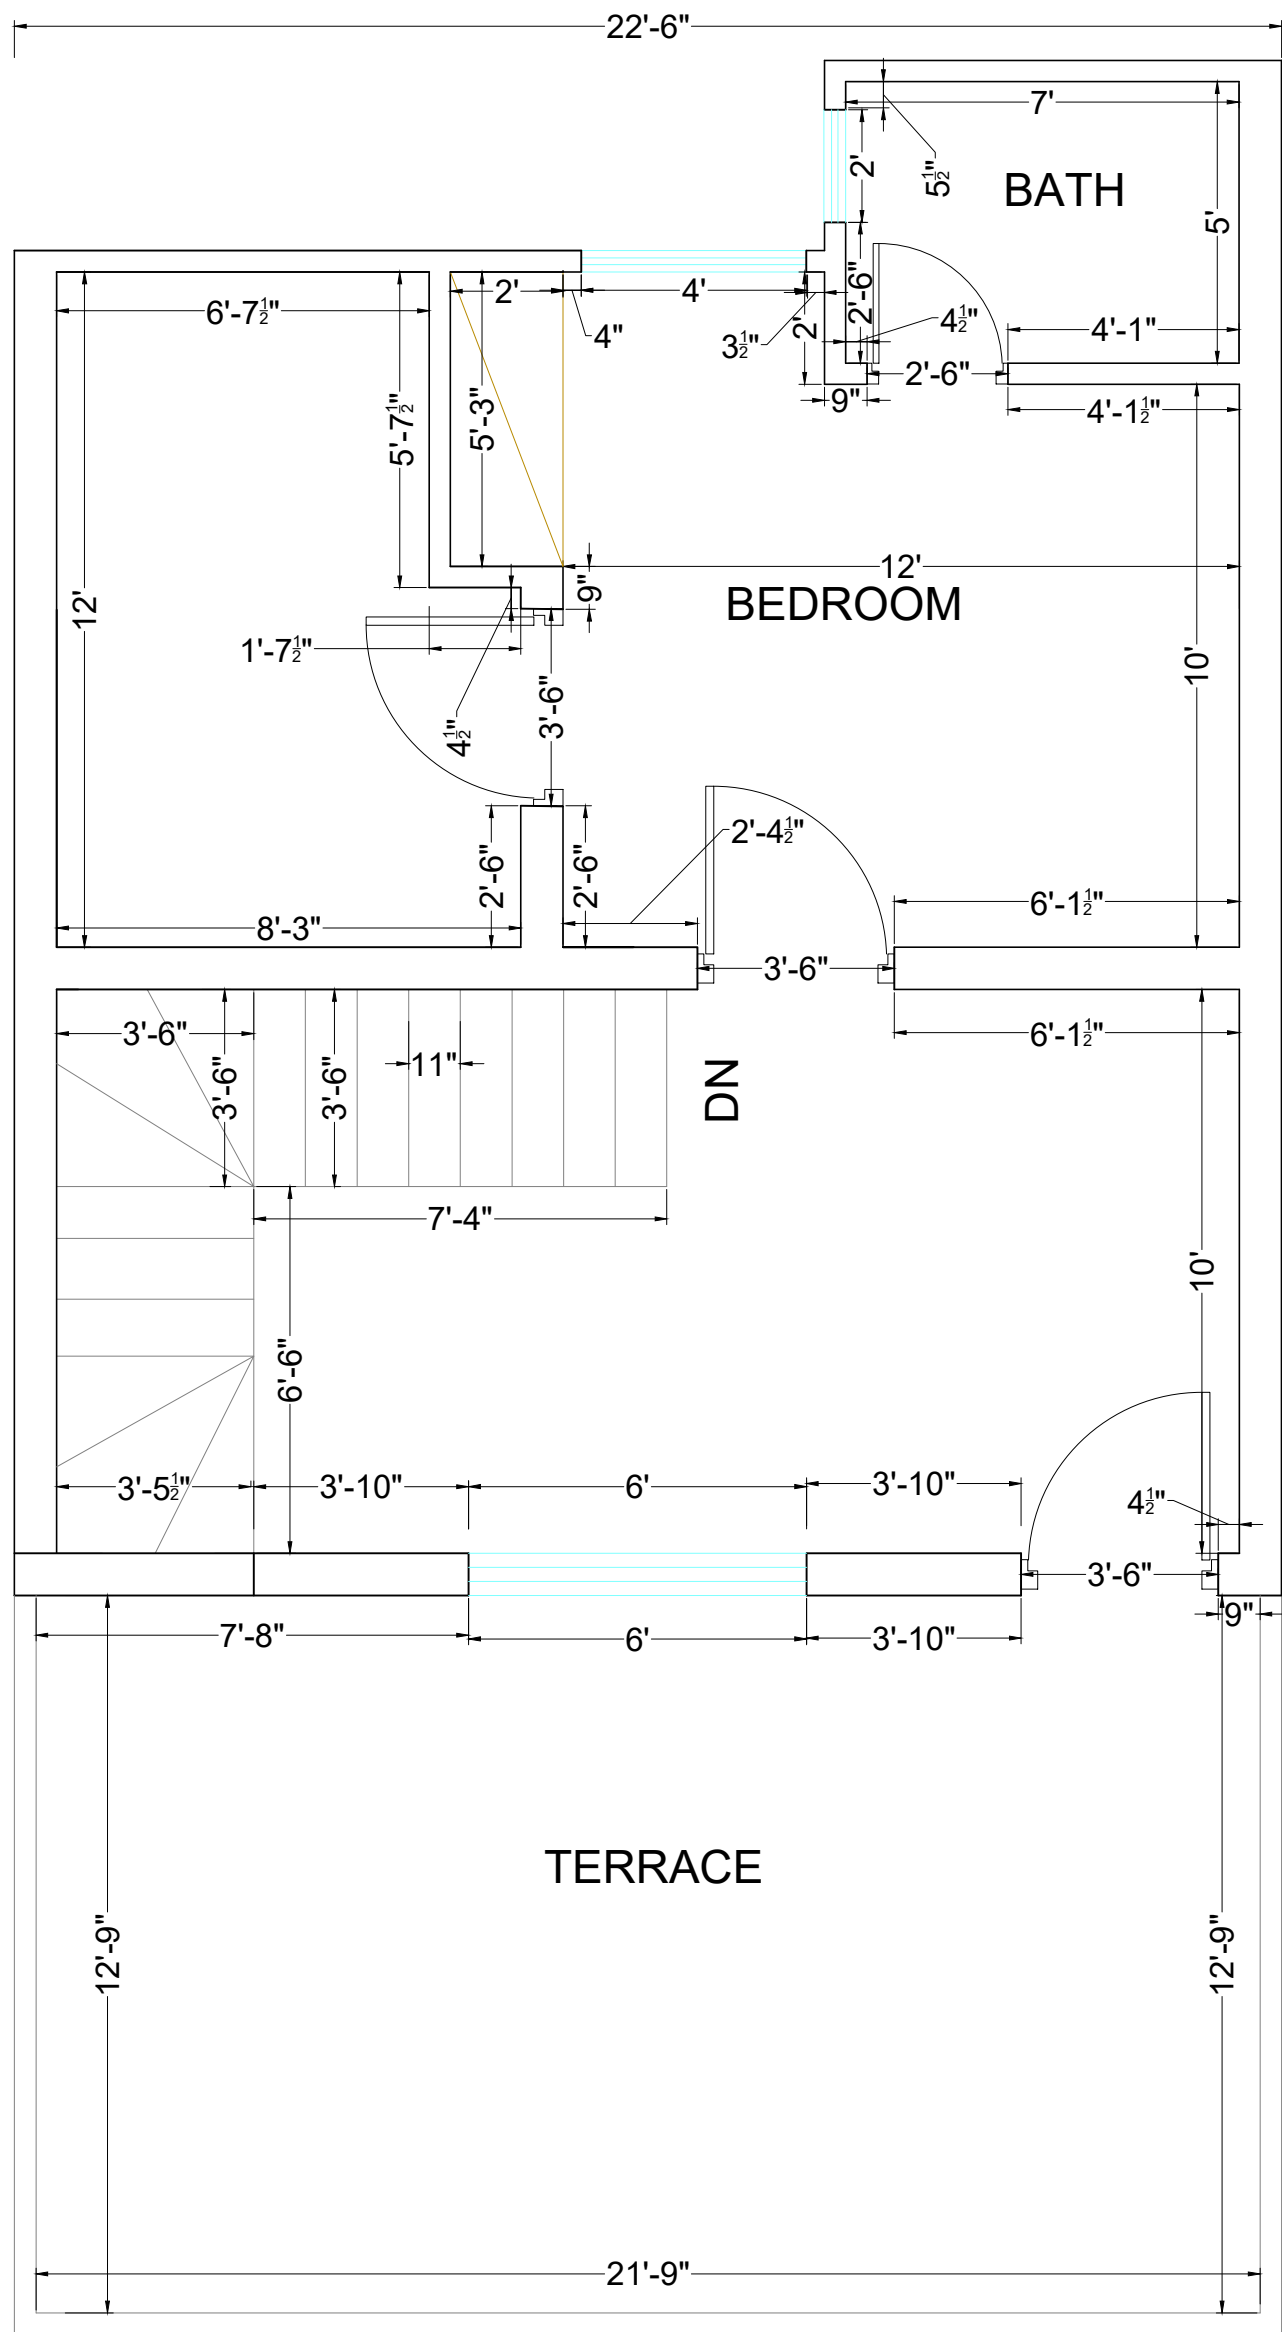












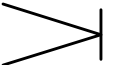


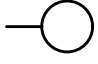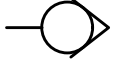

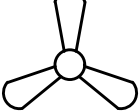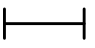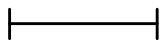

WORKING SECOND FLOOR
 SOHAIL RASHID
 HASSAN BLOCK
 PLOT NO 12 22'-6"x40'
 ALI HOUSING SCHEME, LAHORE




SALMAN AMJAD AND ASSOCIATES:

APPROVED AS CATEGORY-A ARCHITECT LDA.
 REGISTERED PCATP-06011 AND LDA TPRA-298
 OFFICE NO. FIRST FLOOR, MUSTAFA TOWN,
 HIDAYATULLAH STREET, LAHORE
 MOBILE NO → 0306-4706139

LEGEND FOR SYMBOLS-ELECTRICAL WORKS		
SIGN.	DESCRIPTION	SILL LEVEL
	WALL LIGHT	8'-0"
	WATER PROOF LIGHT	AS SITE
	CEILING LIGHT	9'-6" OR A.S.
	CHANDILIER LIGHT	9'-6" OR A.S.
	CONCEALED LIGHT	AS SITE
	SPOT LIGHT	9'-6" OR A.S.
	CEILING FAN	9'-6" OR A.S.
	20W SINGLE TUBE LIGHT	AS SITE
	40W SINGLE TUBE LIGHT	8'-0"
	WALL SOCKET	4'-0"
	3 PIN SWITCH	1'-0" OR A.S.
	SPLIT A.C.	8'-0"
	EXHAUST FAN	AS SITE
	DISTRIBUTION BOARD	5'-0"
	T.V. POINT	4'-0"
	TELEPHONE POINT	1'-0"
	GATE INTERCOM	4'-0"
	INTERCOM RECEIVER	4'-0"
	BELL PUSH	4'-0"

ELECTRICAL SCHEDULE

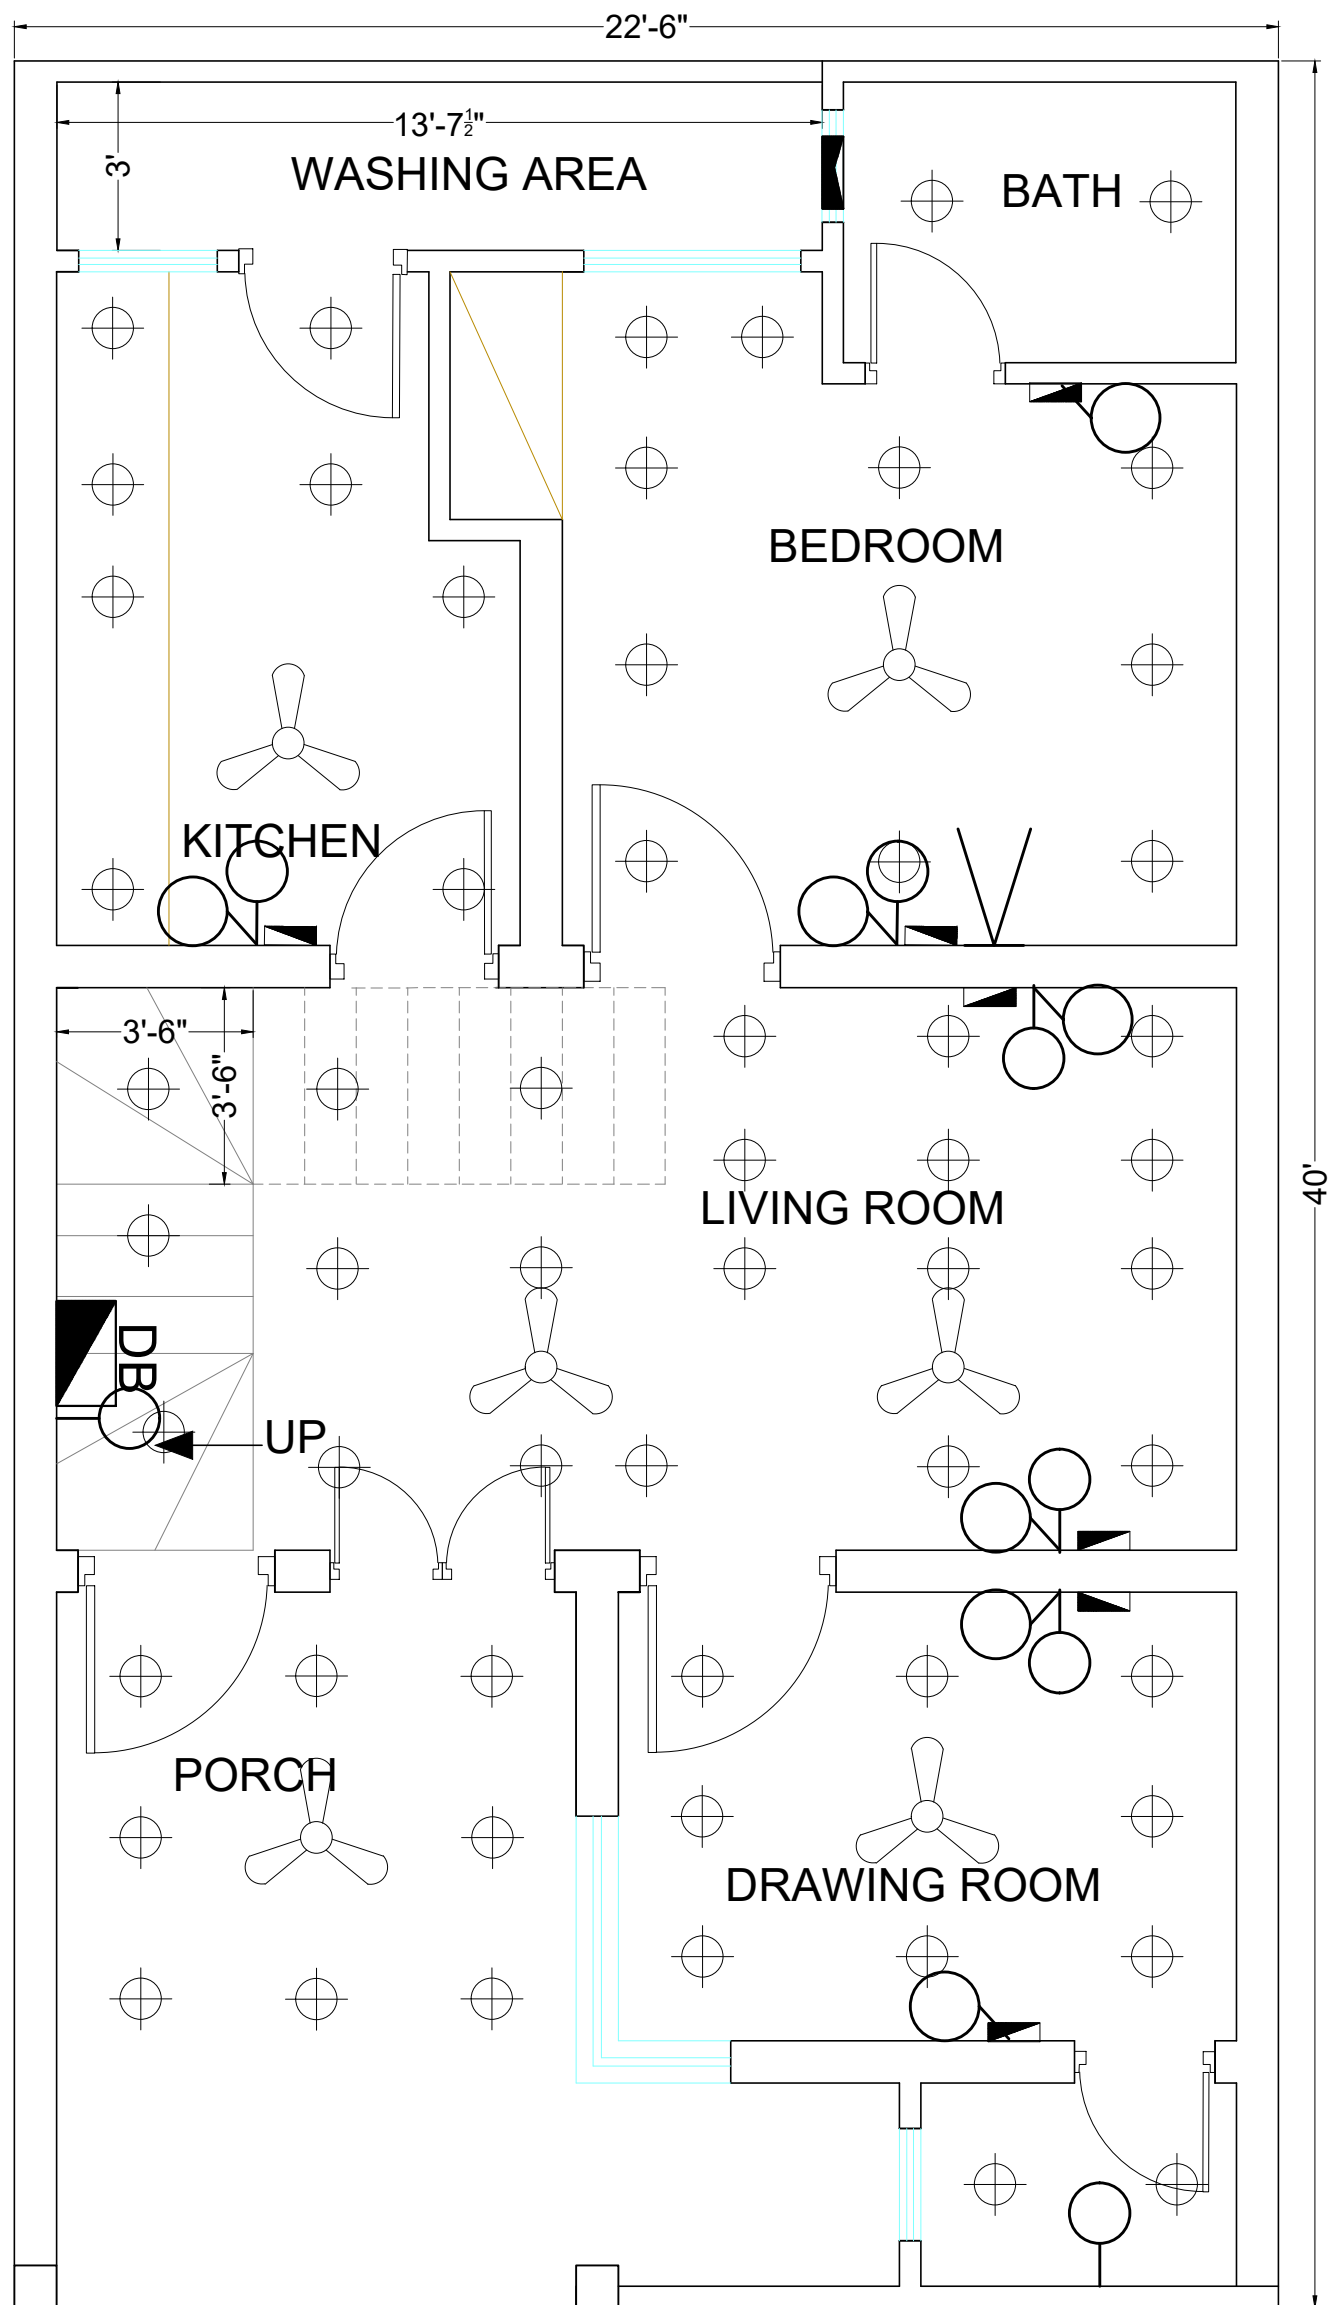


GROUND FLOOR ELECTRICAL PLAN
 SOHAIL RASHID
 HASSAN BLOCK
 PLOT NO 12 22'-6"x40'
 ALI HOUSING SCHEME, LAHORE



SALMAN AMJAD AND ASSOCIATES:

APPROVED AS CATEGORY-A ARCHITECT LDA.
 REGISTERED PCATP-06011 AND LDA TPRA-298
 OFFICE NO. FIRST FLOOR, MUSTAFA TOWN,
 HIDAYATULLAH STREET, LAHORE
 MOBILE NO → 0306-4706139

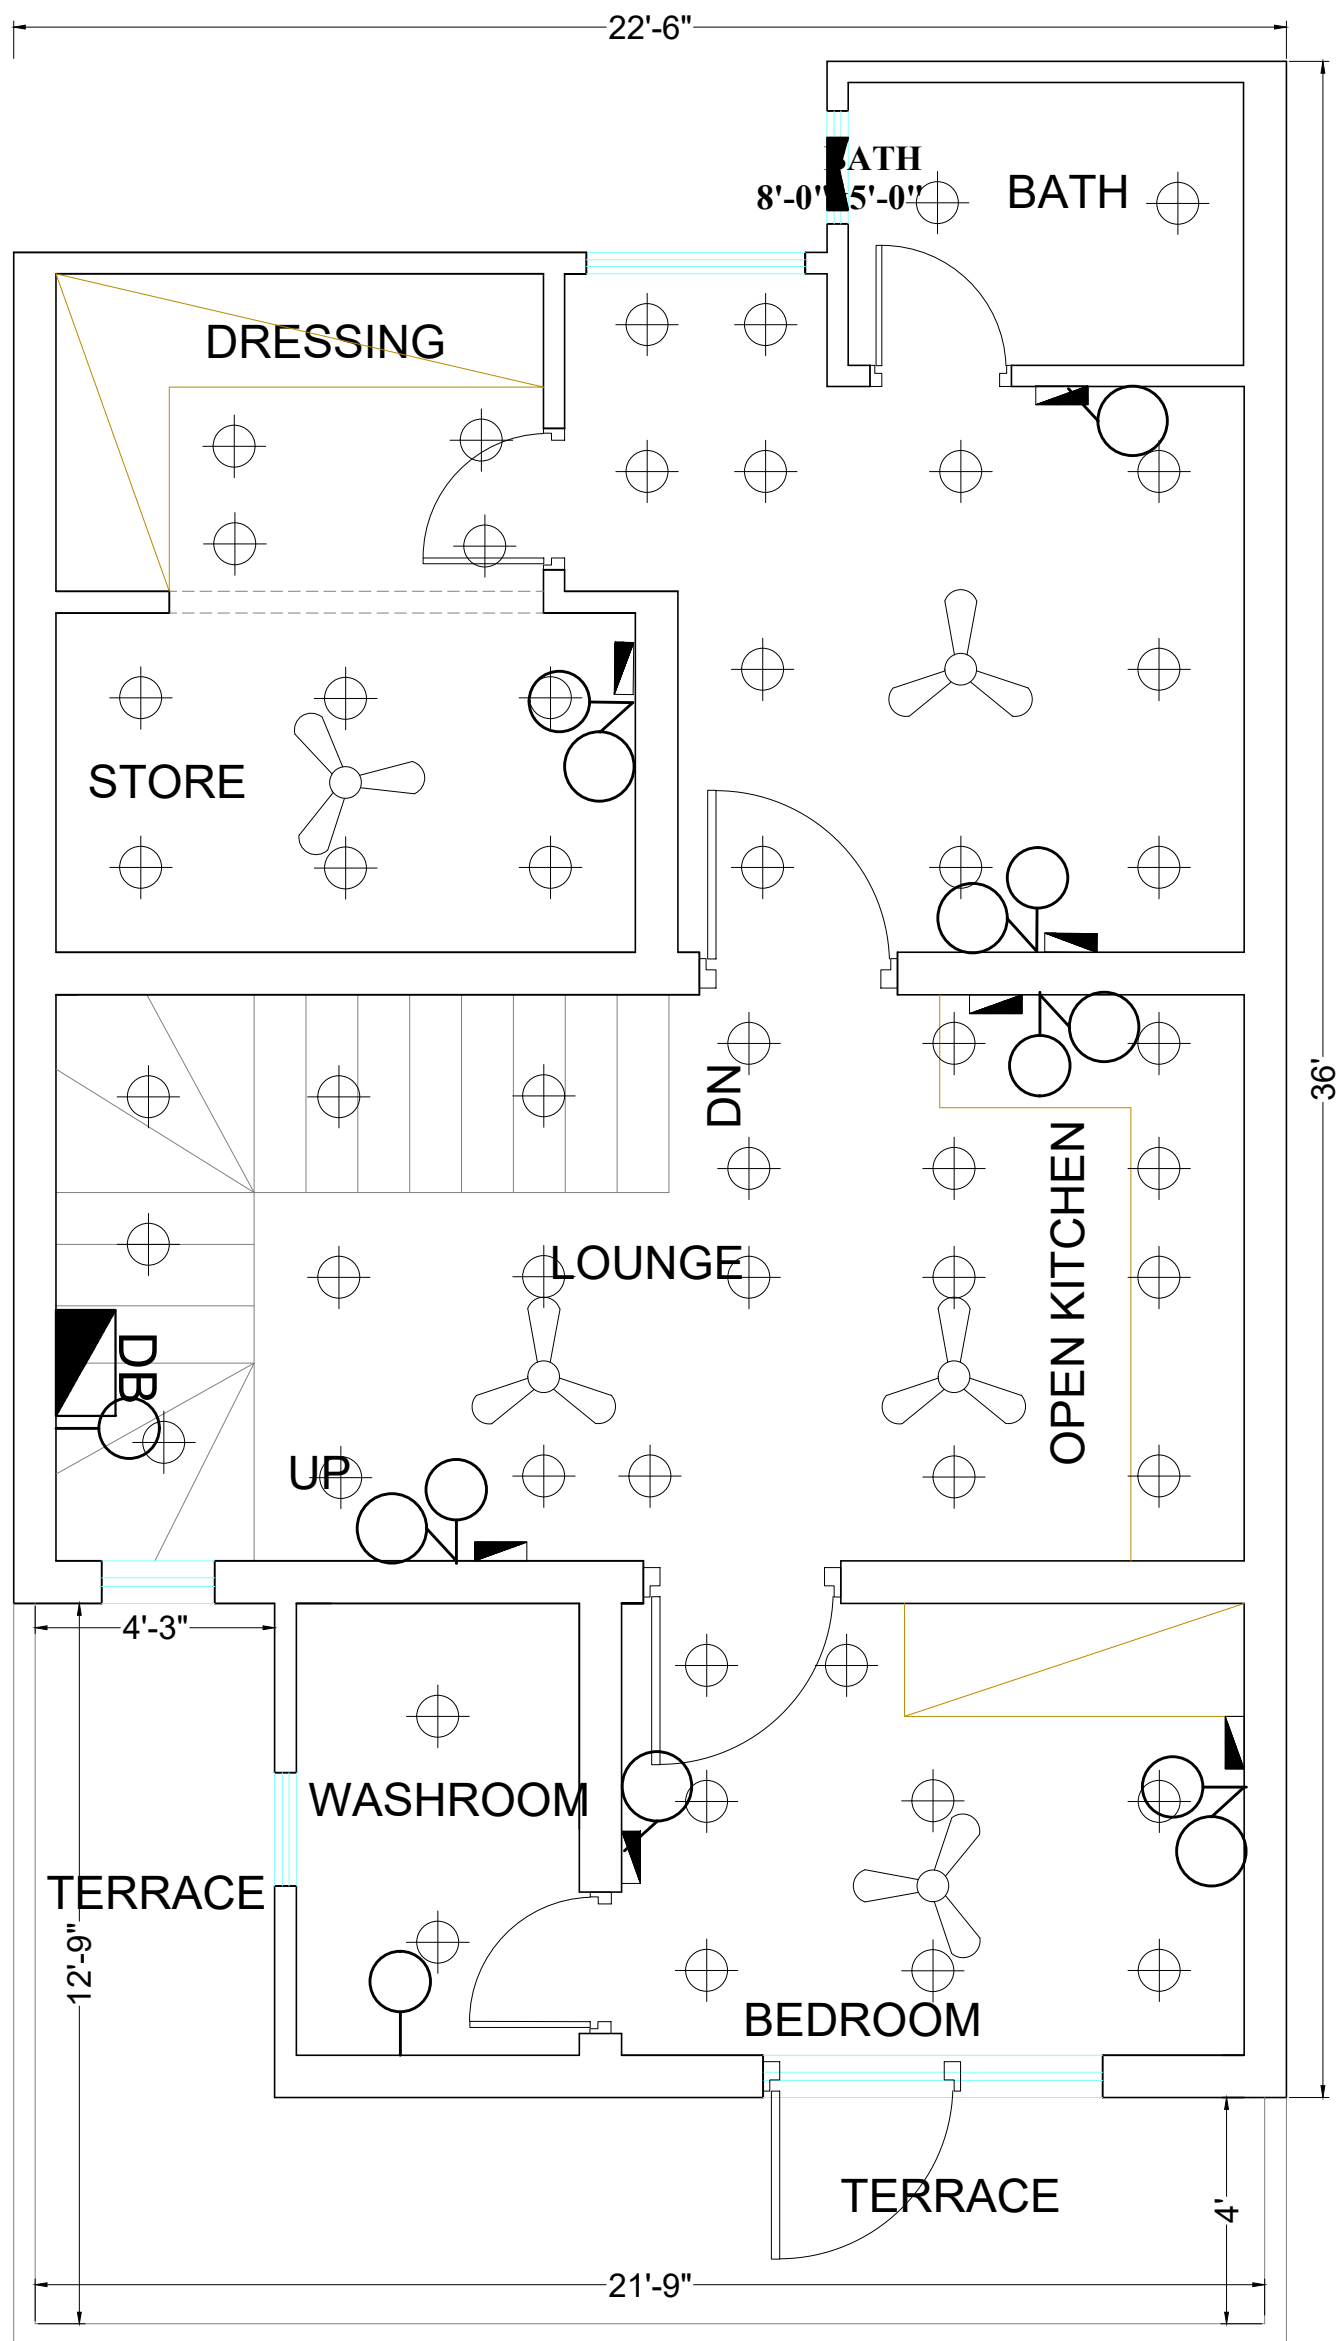


FIRST FLOOR ELECTRICAL PLAN
SOHAIL RASHID
HASSAN BLOCK
PLOT NO 12 22'-6"x40'
ALI HOUSING SCHEME, LAHORE



SALMAN AMJAD AND ASSOCIATES:

APPROVED AS CATEGORY-A ARCHITECT LDA.
REGISTERED PCATP-06011 AND LDA TPRA-298
OFFICE NO. FIRST FLOOR, MUSTAFA TOWN,
HIDAYATULLAH STREET, LAHORE
MOBILE NO → 0306-4706139

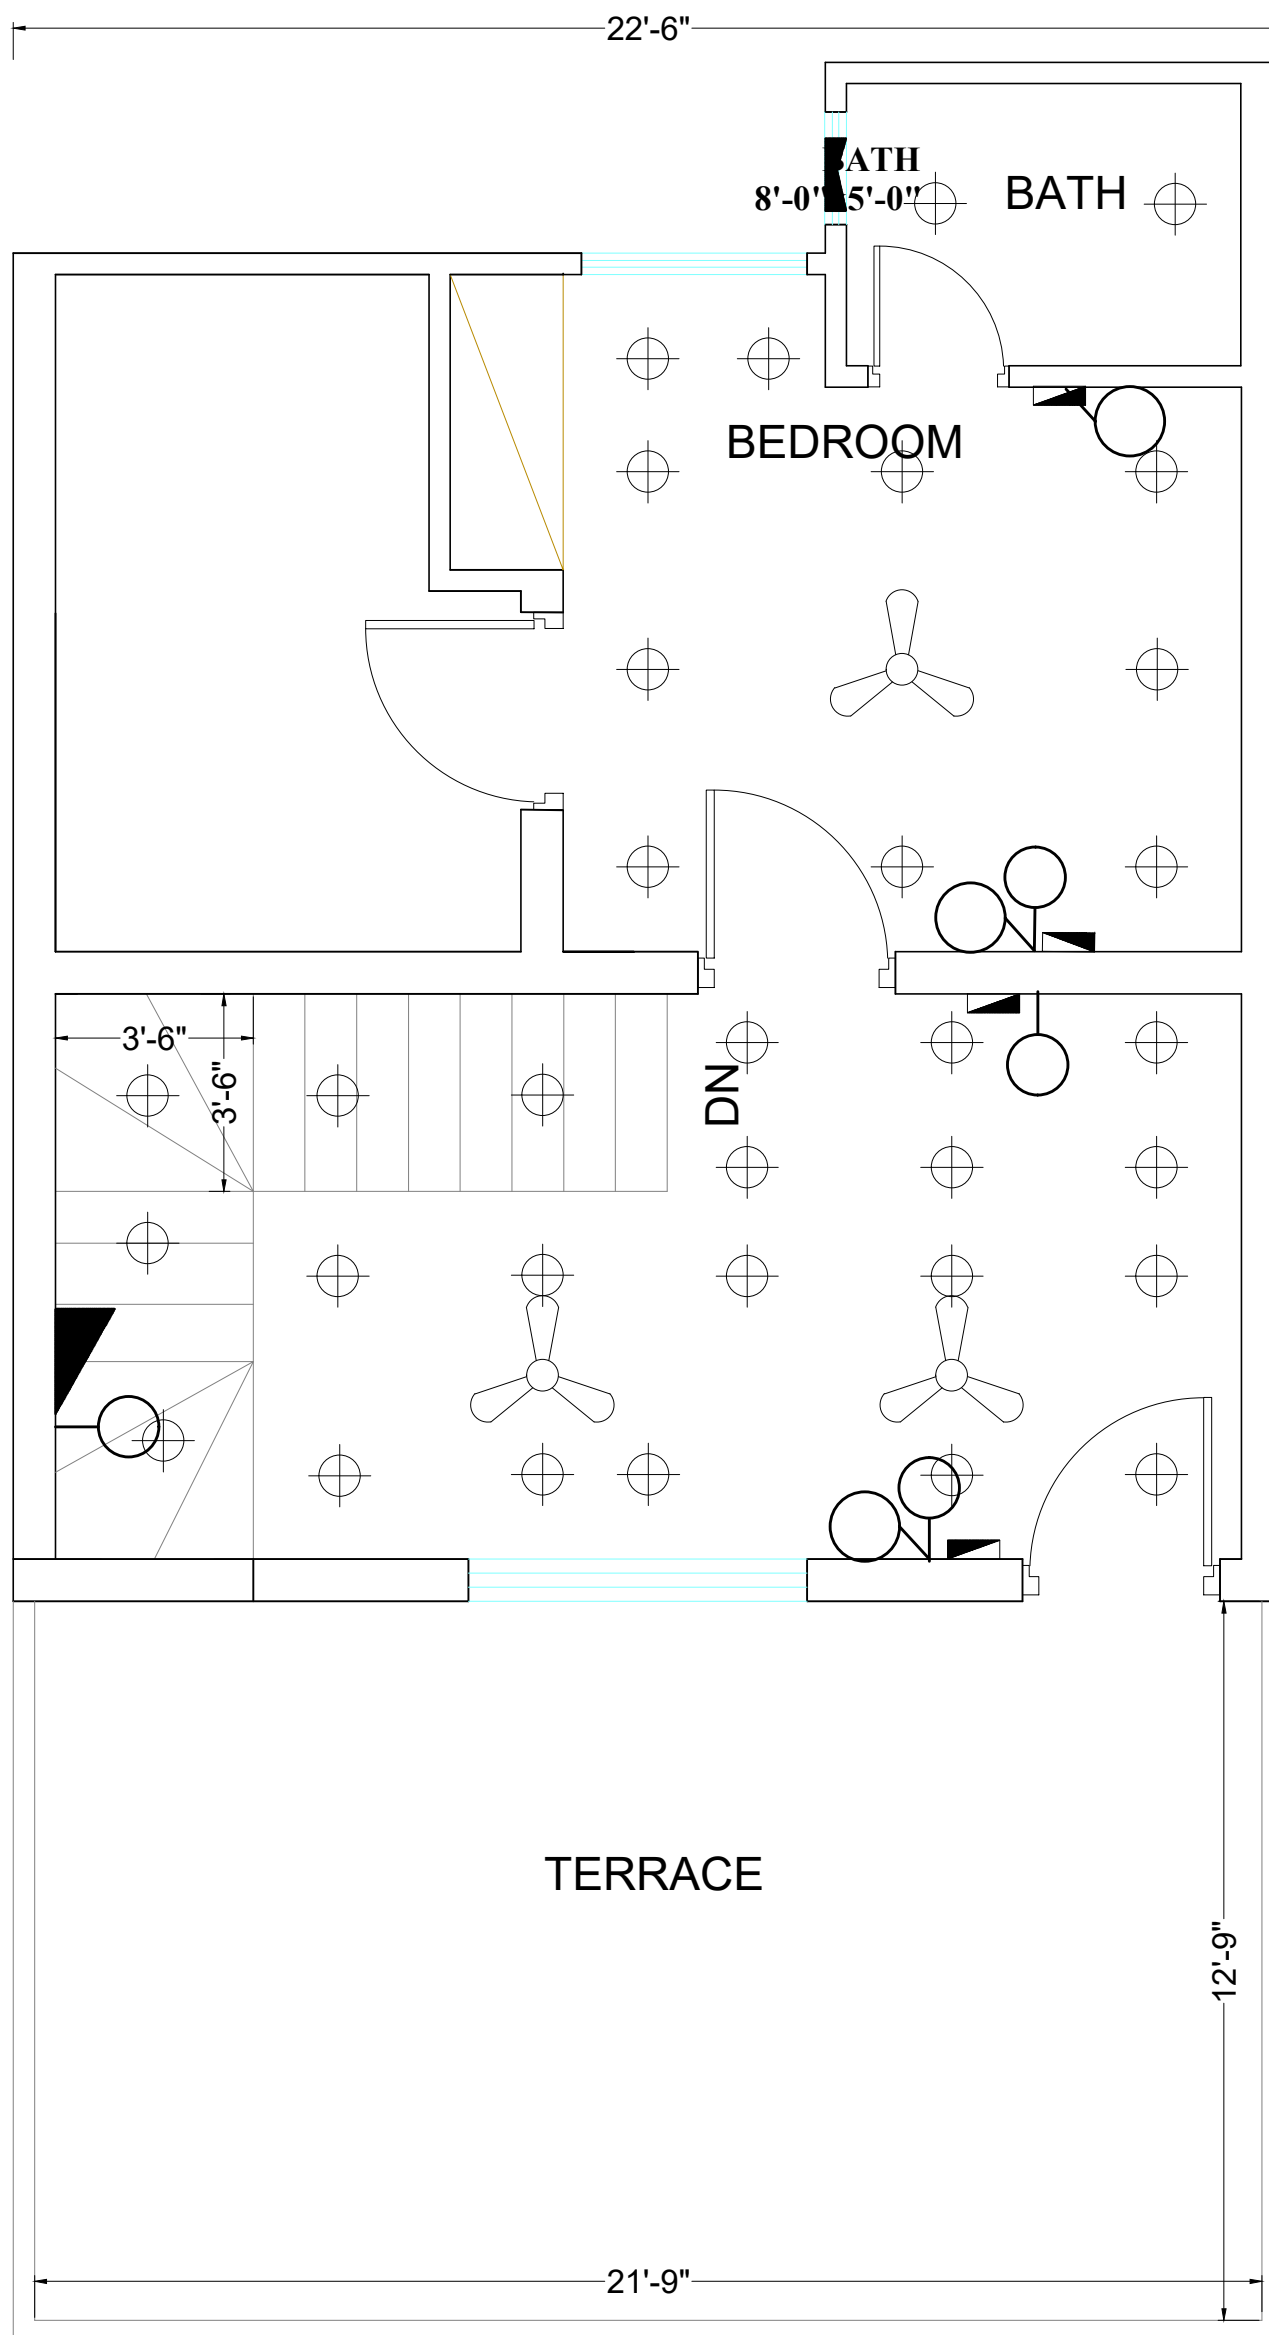


SECOND FLOOR ELECTRICAL PLAN
SOHAIL RASHID
HASSAN BLOCK
PLOT NO 12 22'-6"x40'
ALI HOUSING SCHEME, LAHORE



SALMAN AMJAD AND ASSOCIATES:

APPROVED AS CATEGORY-A ARCHITECT LDA.
REGISTERED PCATP-06011 AND LDA TPRA-298
OFFICE NO. FIRST FLOOR, MUSTAFA TOWN,
HIDAYATULLAH STREET, LAHORE
MOBILE NO → 0306-4706139

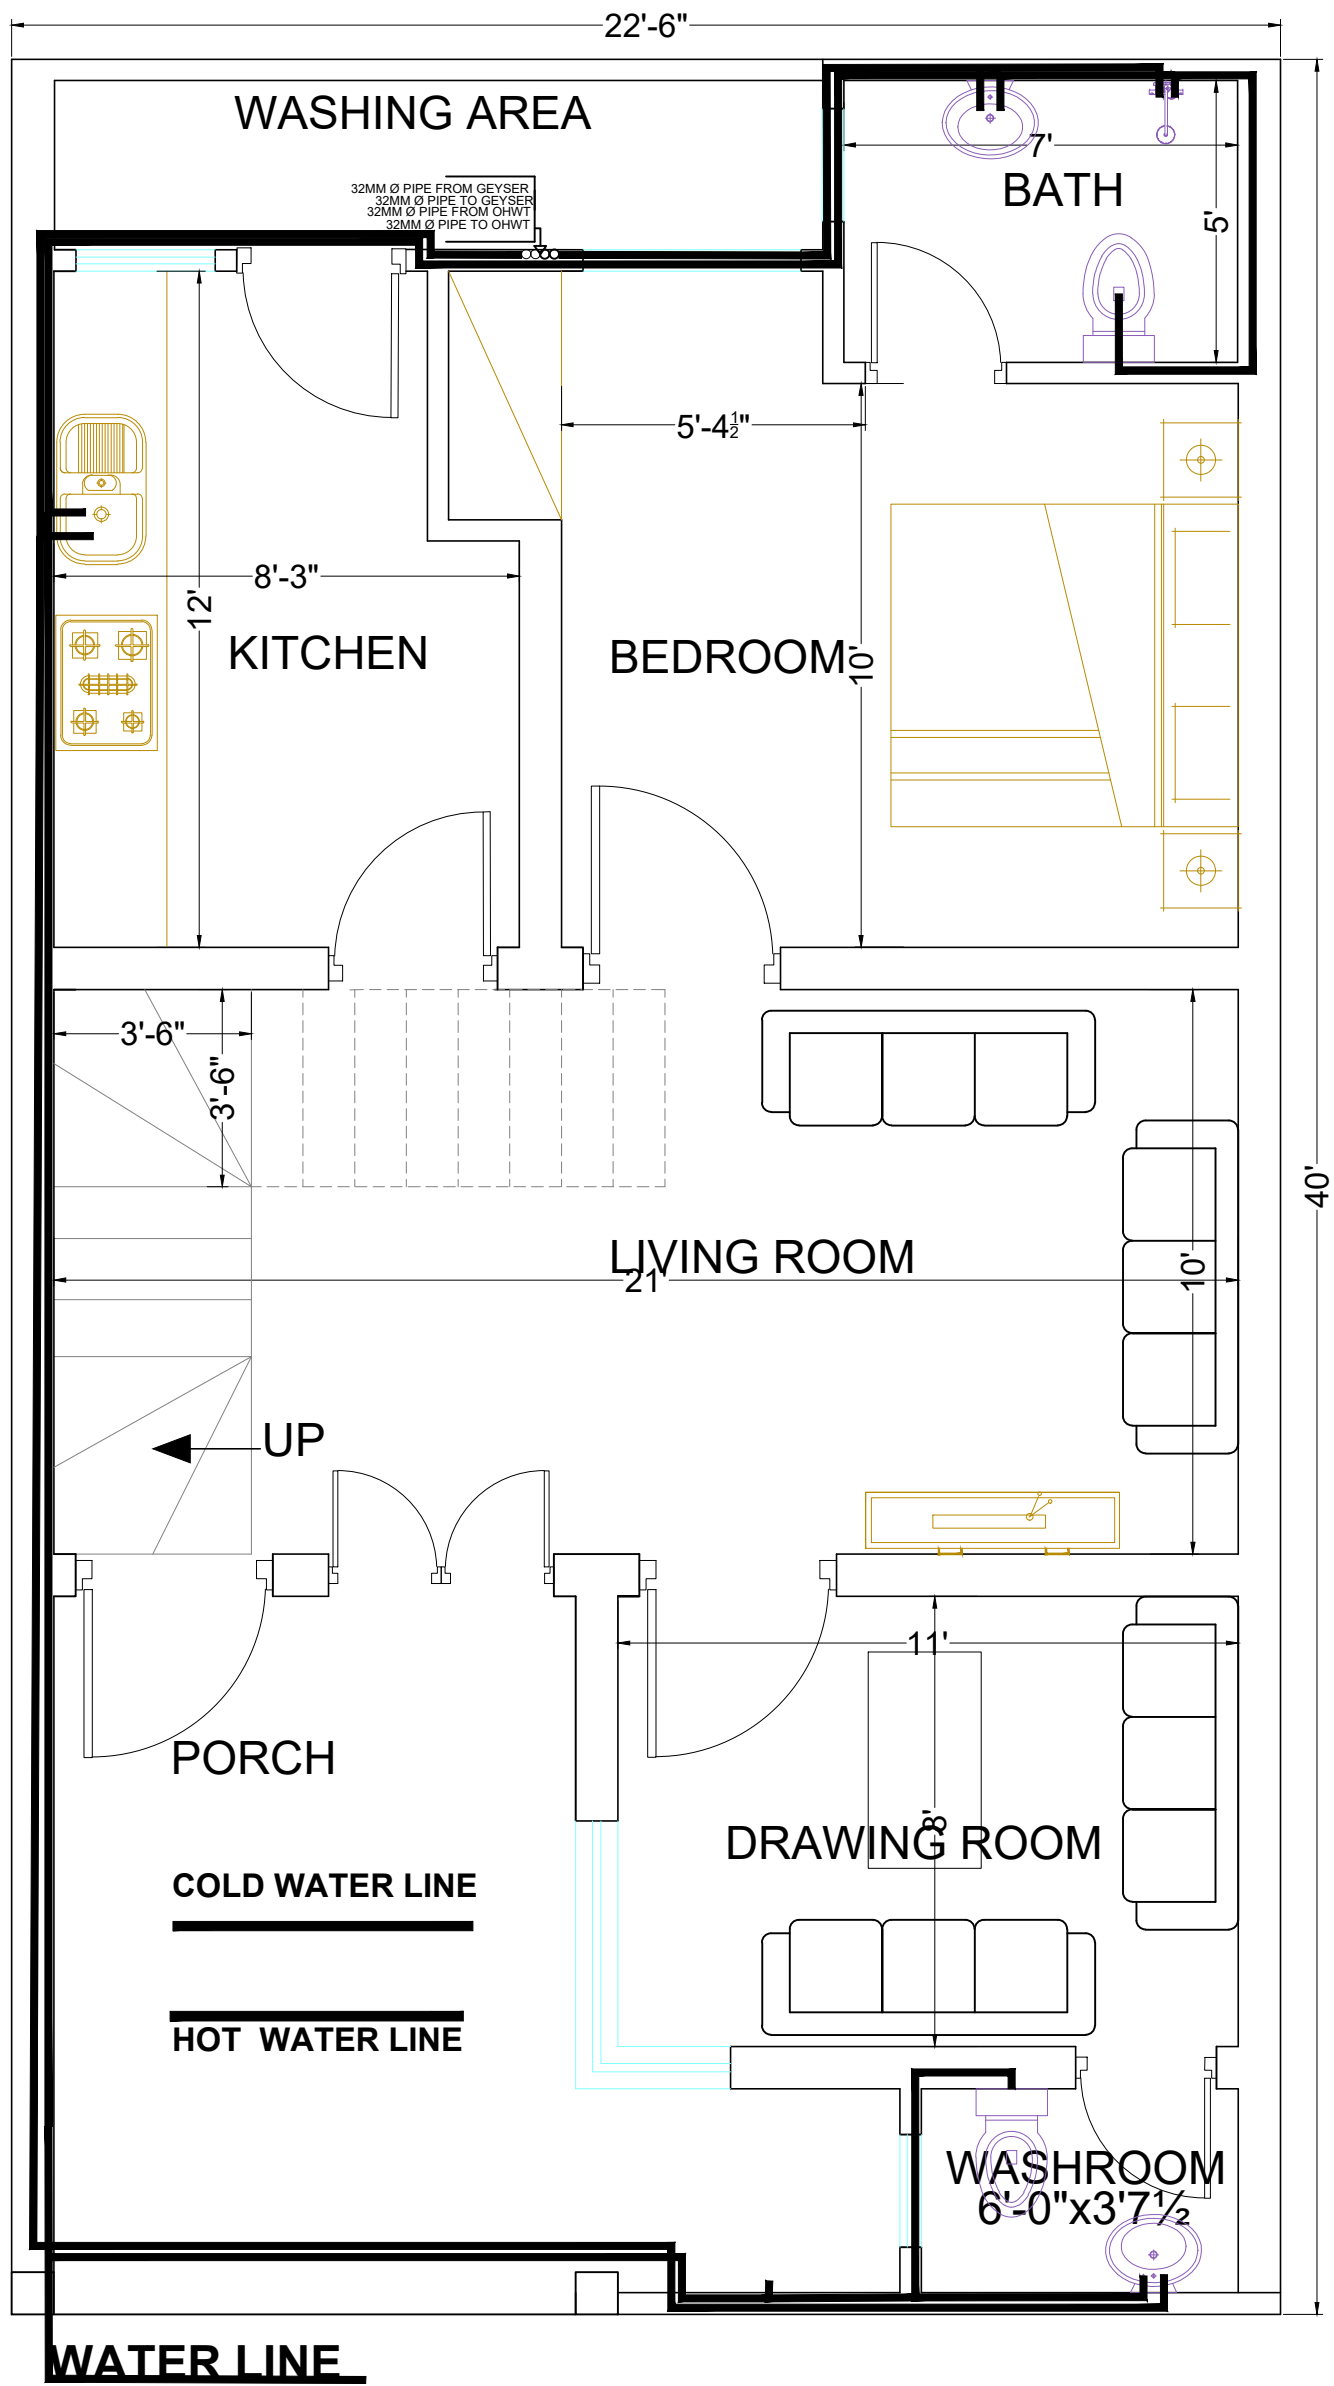


GROUND PLUMBING FLOOR
 SOHAIL RASHID
 HASSAN BLOCK
 PLOT NO 12 22'-6"x40'
 ALI HOUSING SCHEME, LAHORE



SALMAN AMJAD AND ASSOCIATES:

APPROVED AS CATEGORY-A ARCHITECT LDA.
 REGISTERED PCATP-06011 AND LDA TPRA-298
 OFFICE NO. FIRST FLOOR, MUSTAFA TOWN,
 HIDAYATULLAH STREET, LAHORE
 MOBILE NO → 0306-4706139

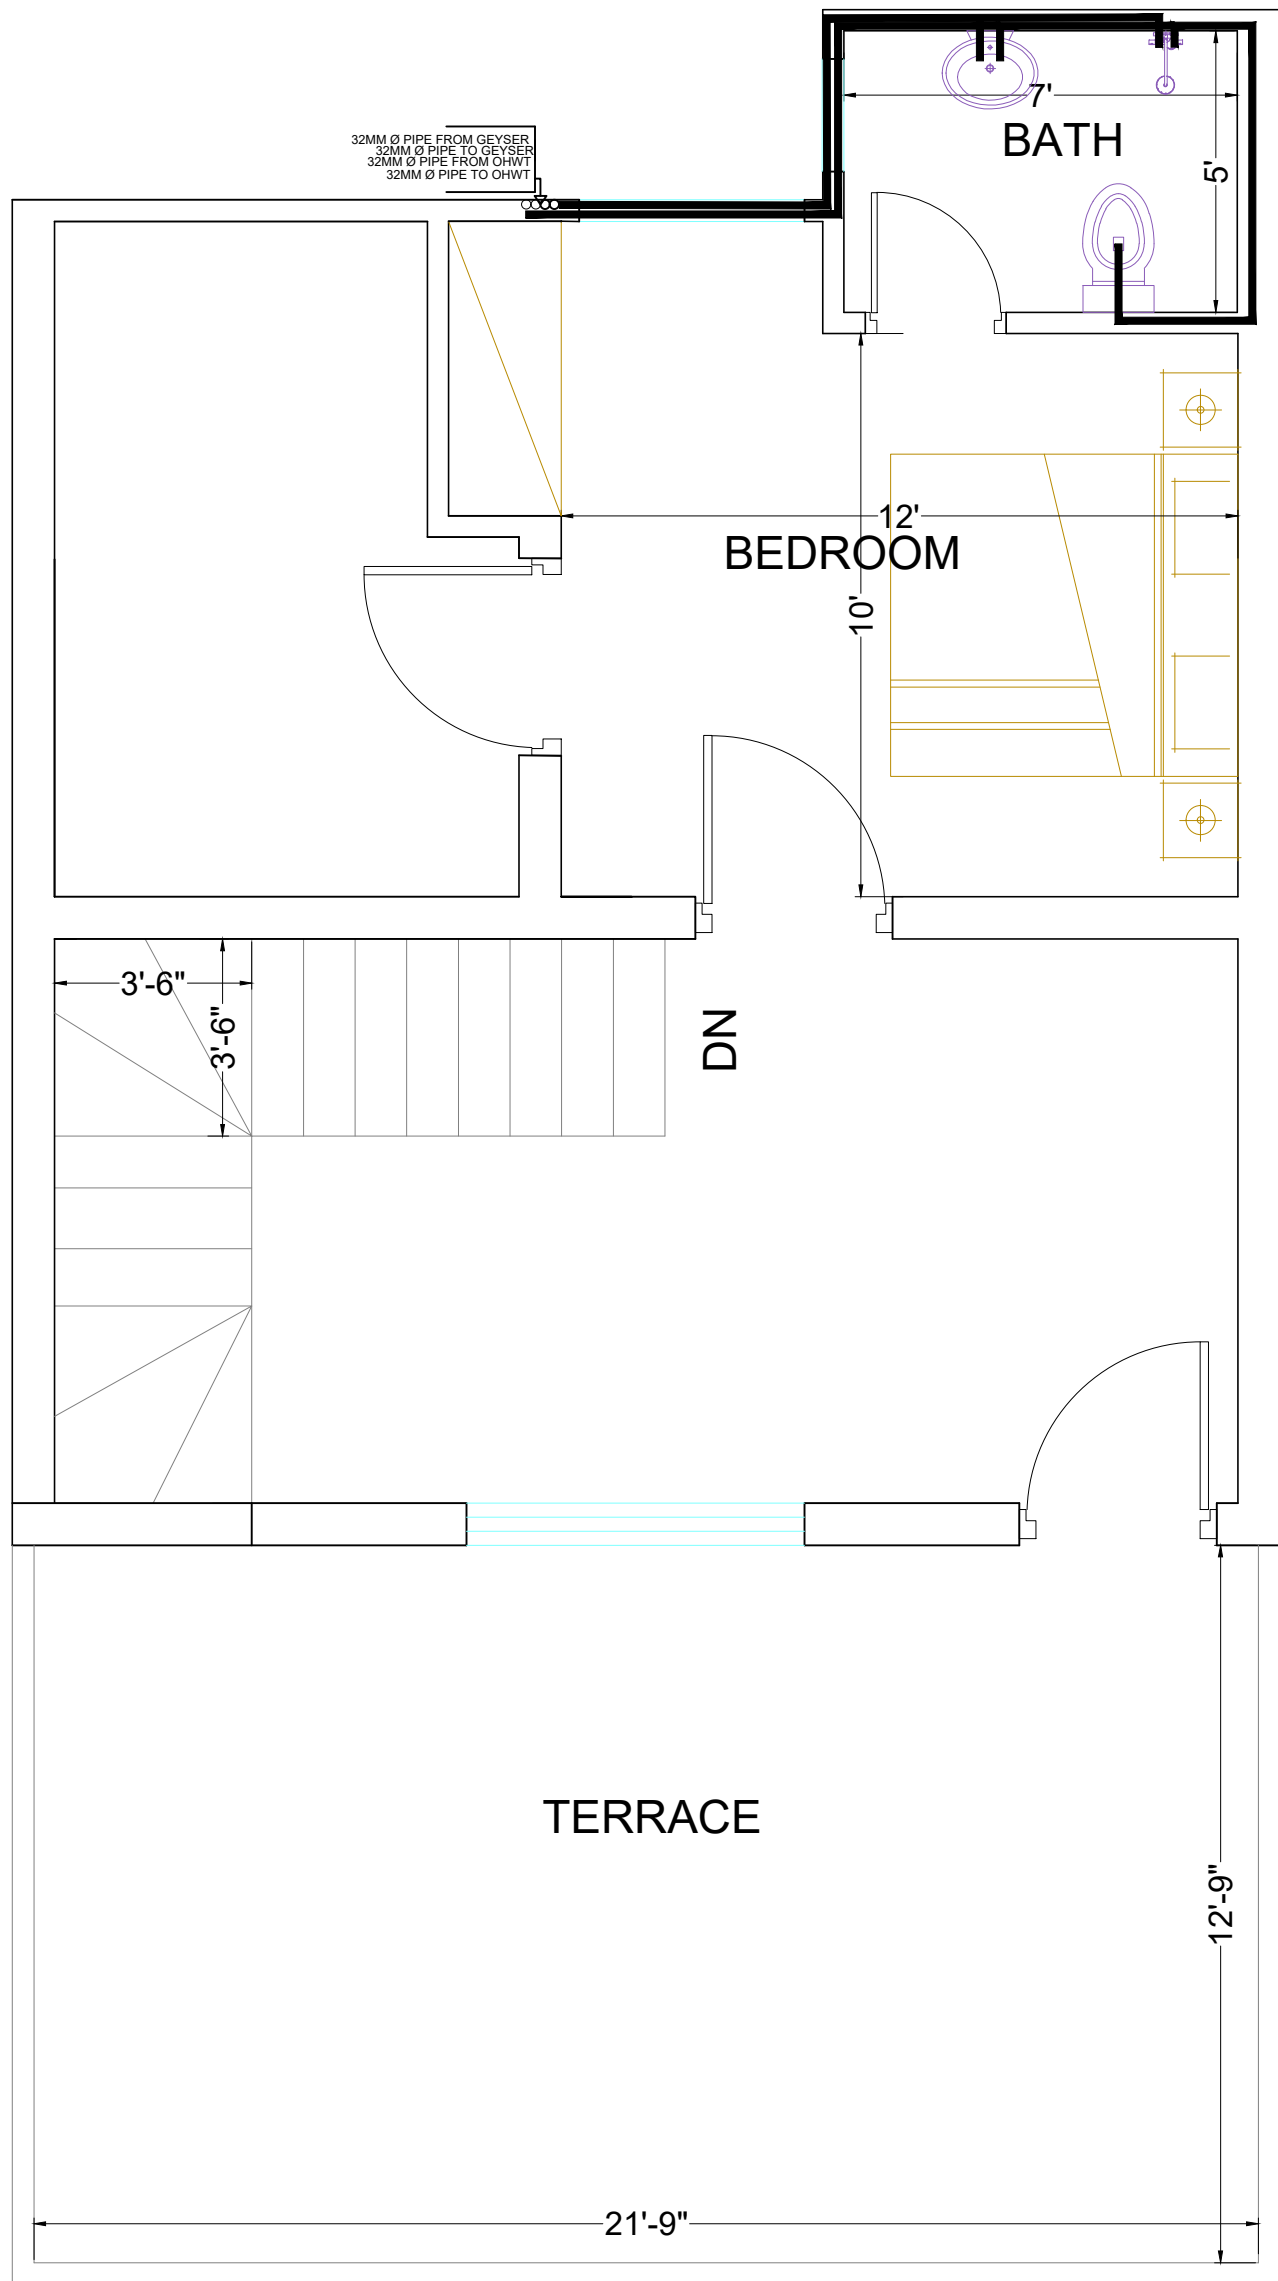

SECOND PLUMBING FLOOR
SOHAIL RASHID
HASSAN BLOCK
PLOT NO 12 22'-6"x40'
ALI HOUSING SCHEME, LAHORE


COLD WATER LINE

HOT WATER LINE



SALMAN AMJAD AND ASSOCIATES:

APPROVED AS CATEGORY-A ARCHITECT LDA.
REGISTERED PCATP-06011 AND LDA TPRA-298
OFFICE NO. FIRST FLOOR, MUSTAFA TOWN,
HIDAYATULLAH STREET, LAHORE
MOBILE NO → 0306-4706139

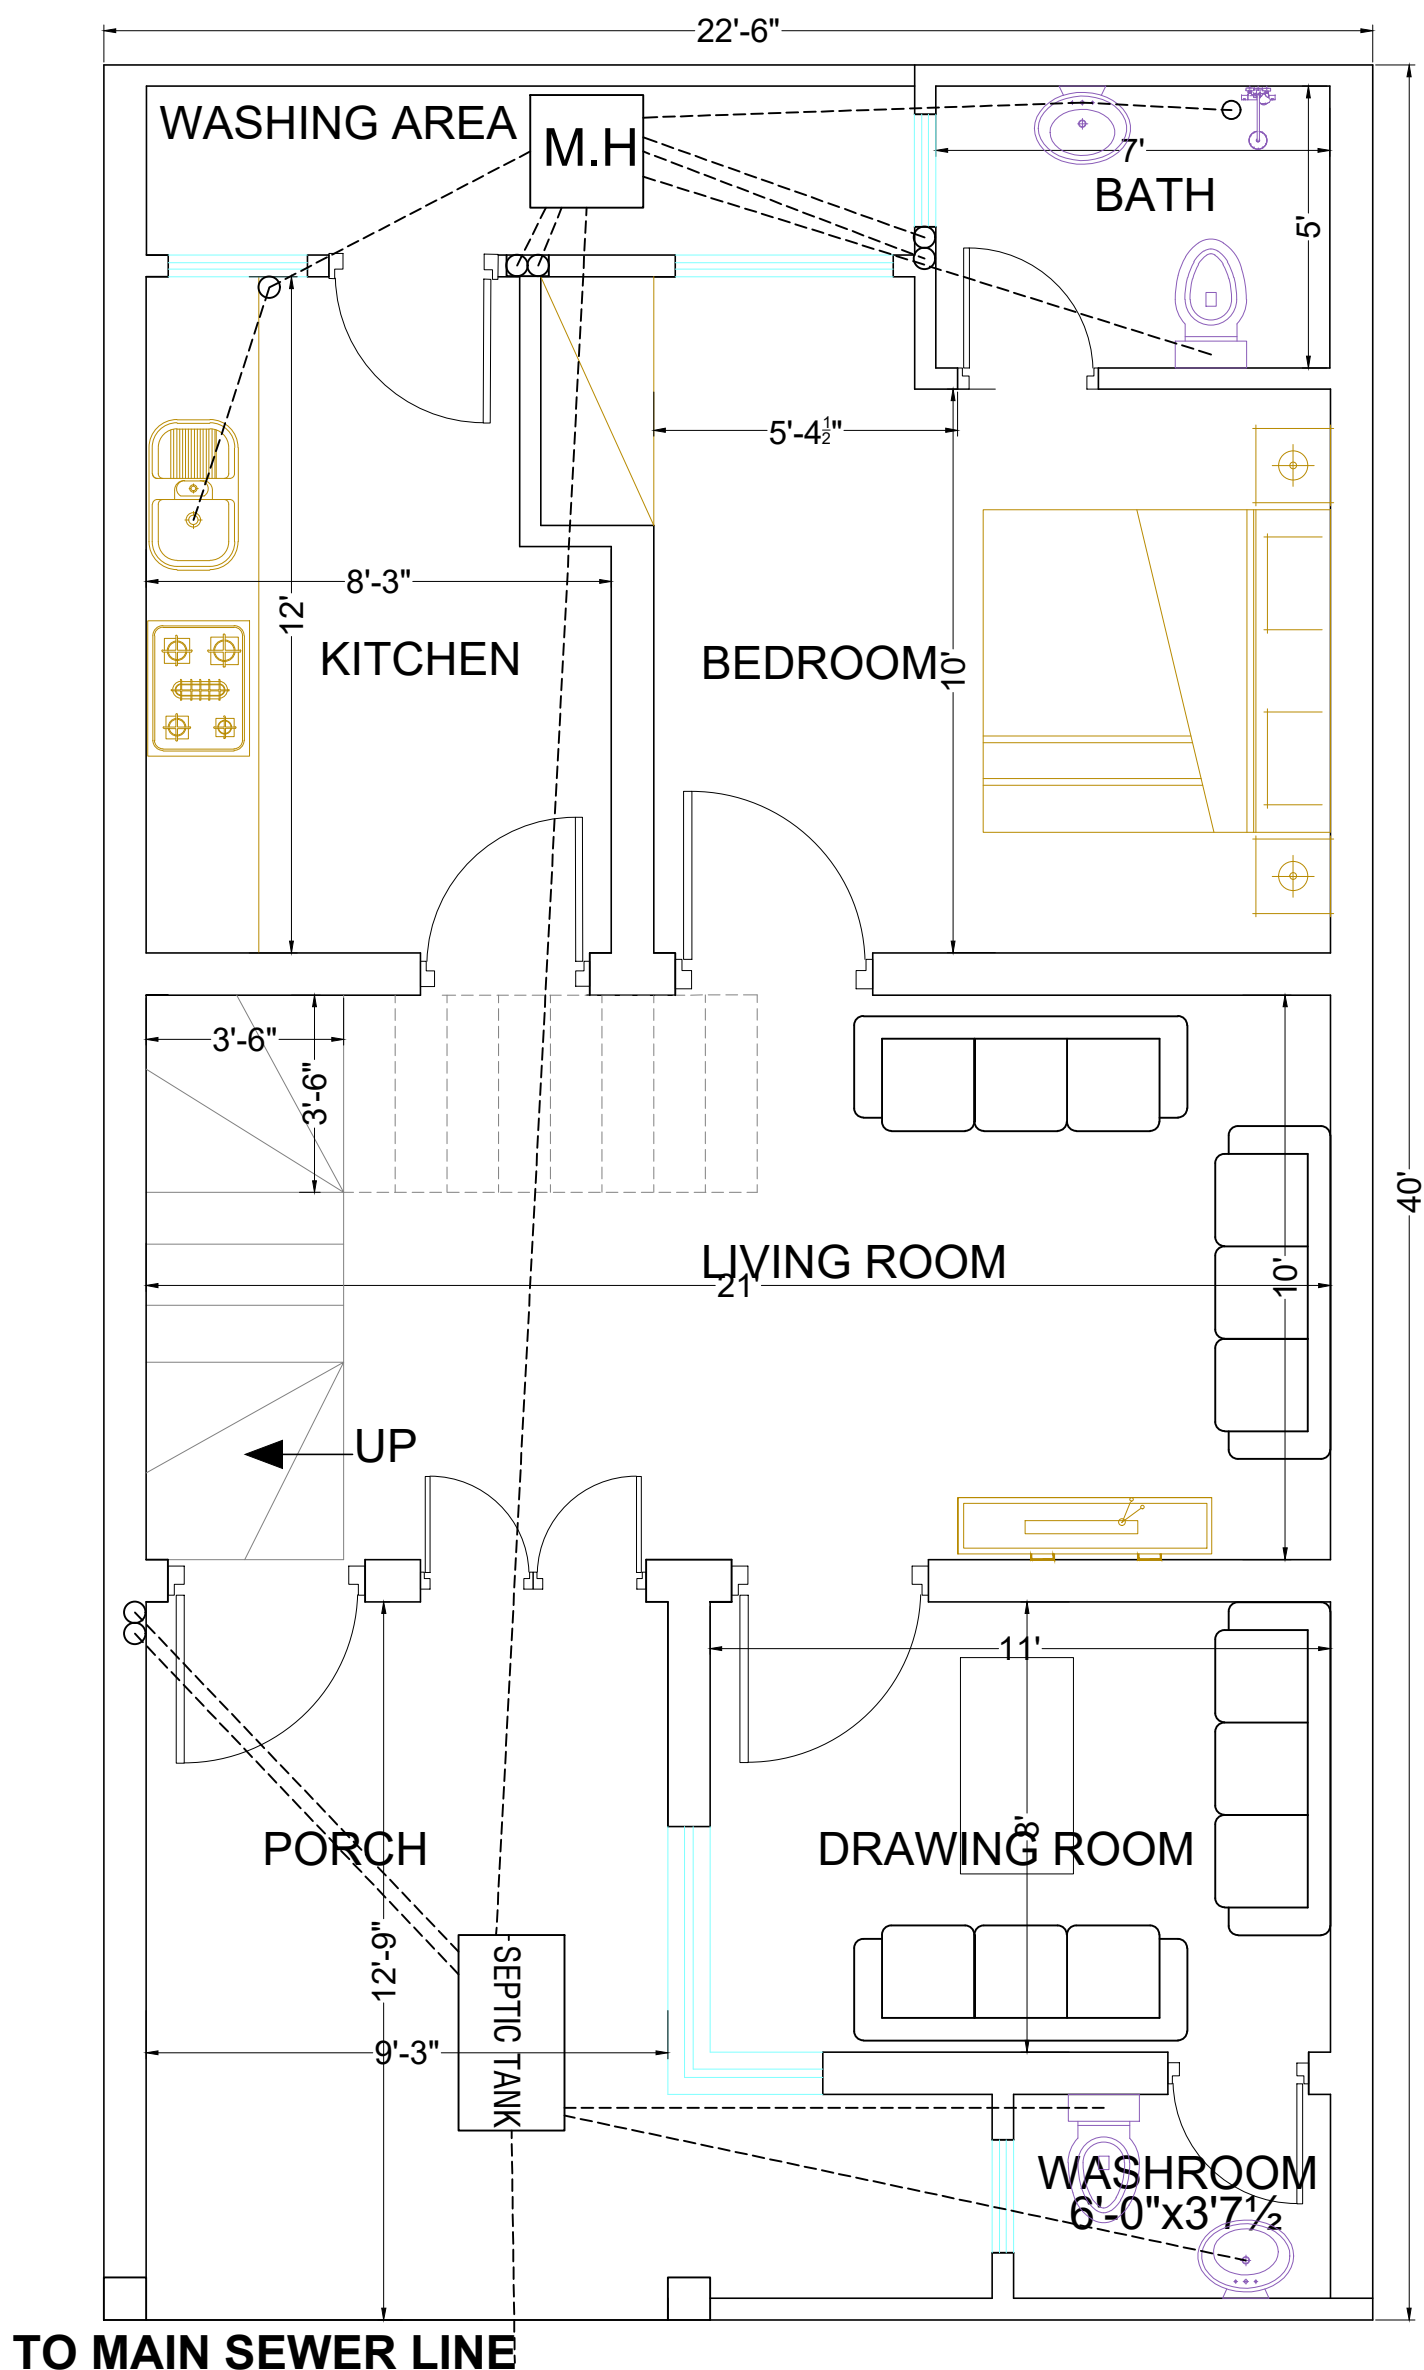

TO MAIN SEWER LINE

GROUND SEWER FLOOR

SOHAIL RASHID

HASSAN BLOCK


PLOT NO 12 22'-6"x40'

ALI HOUSING SCHEME, LAHORE



SALMAN AMJAD AND ASSOCIATES:

APPROVED AS CATEGORY-A ARCHITECT LDA.
REGISTERED PCATP-06011 AND LDA TPRA-298
OFFICE NO. FIRST FLOOR, MUSTAFA TOWN,
HIDAYATULLAH STREET, LAHORE
MOBILE NO → 0306-4706139

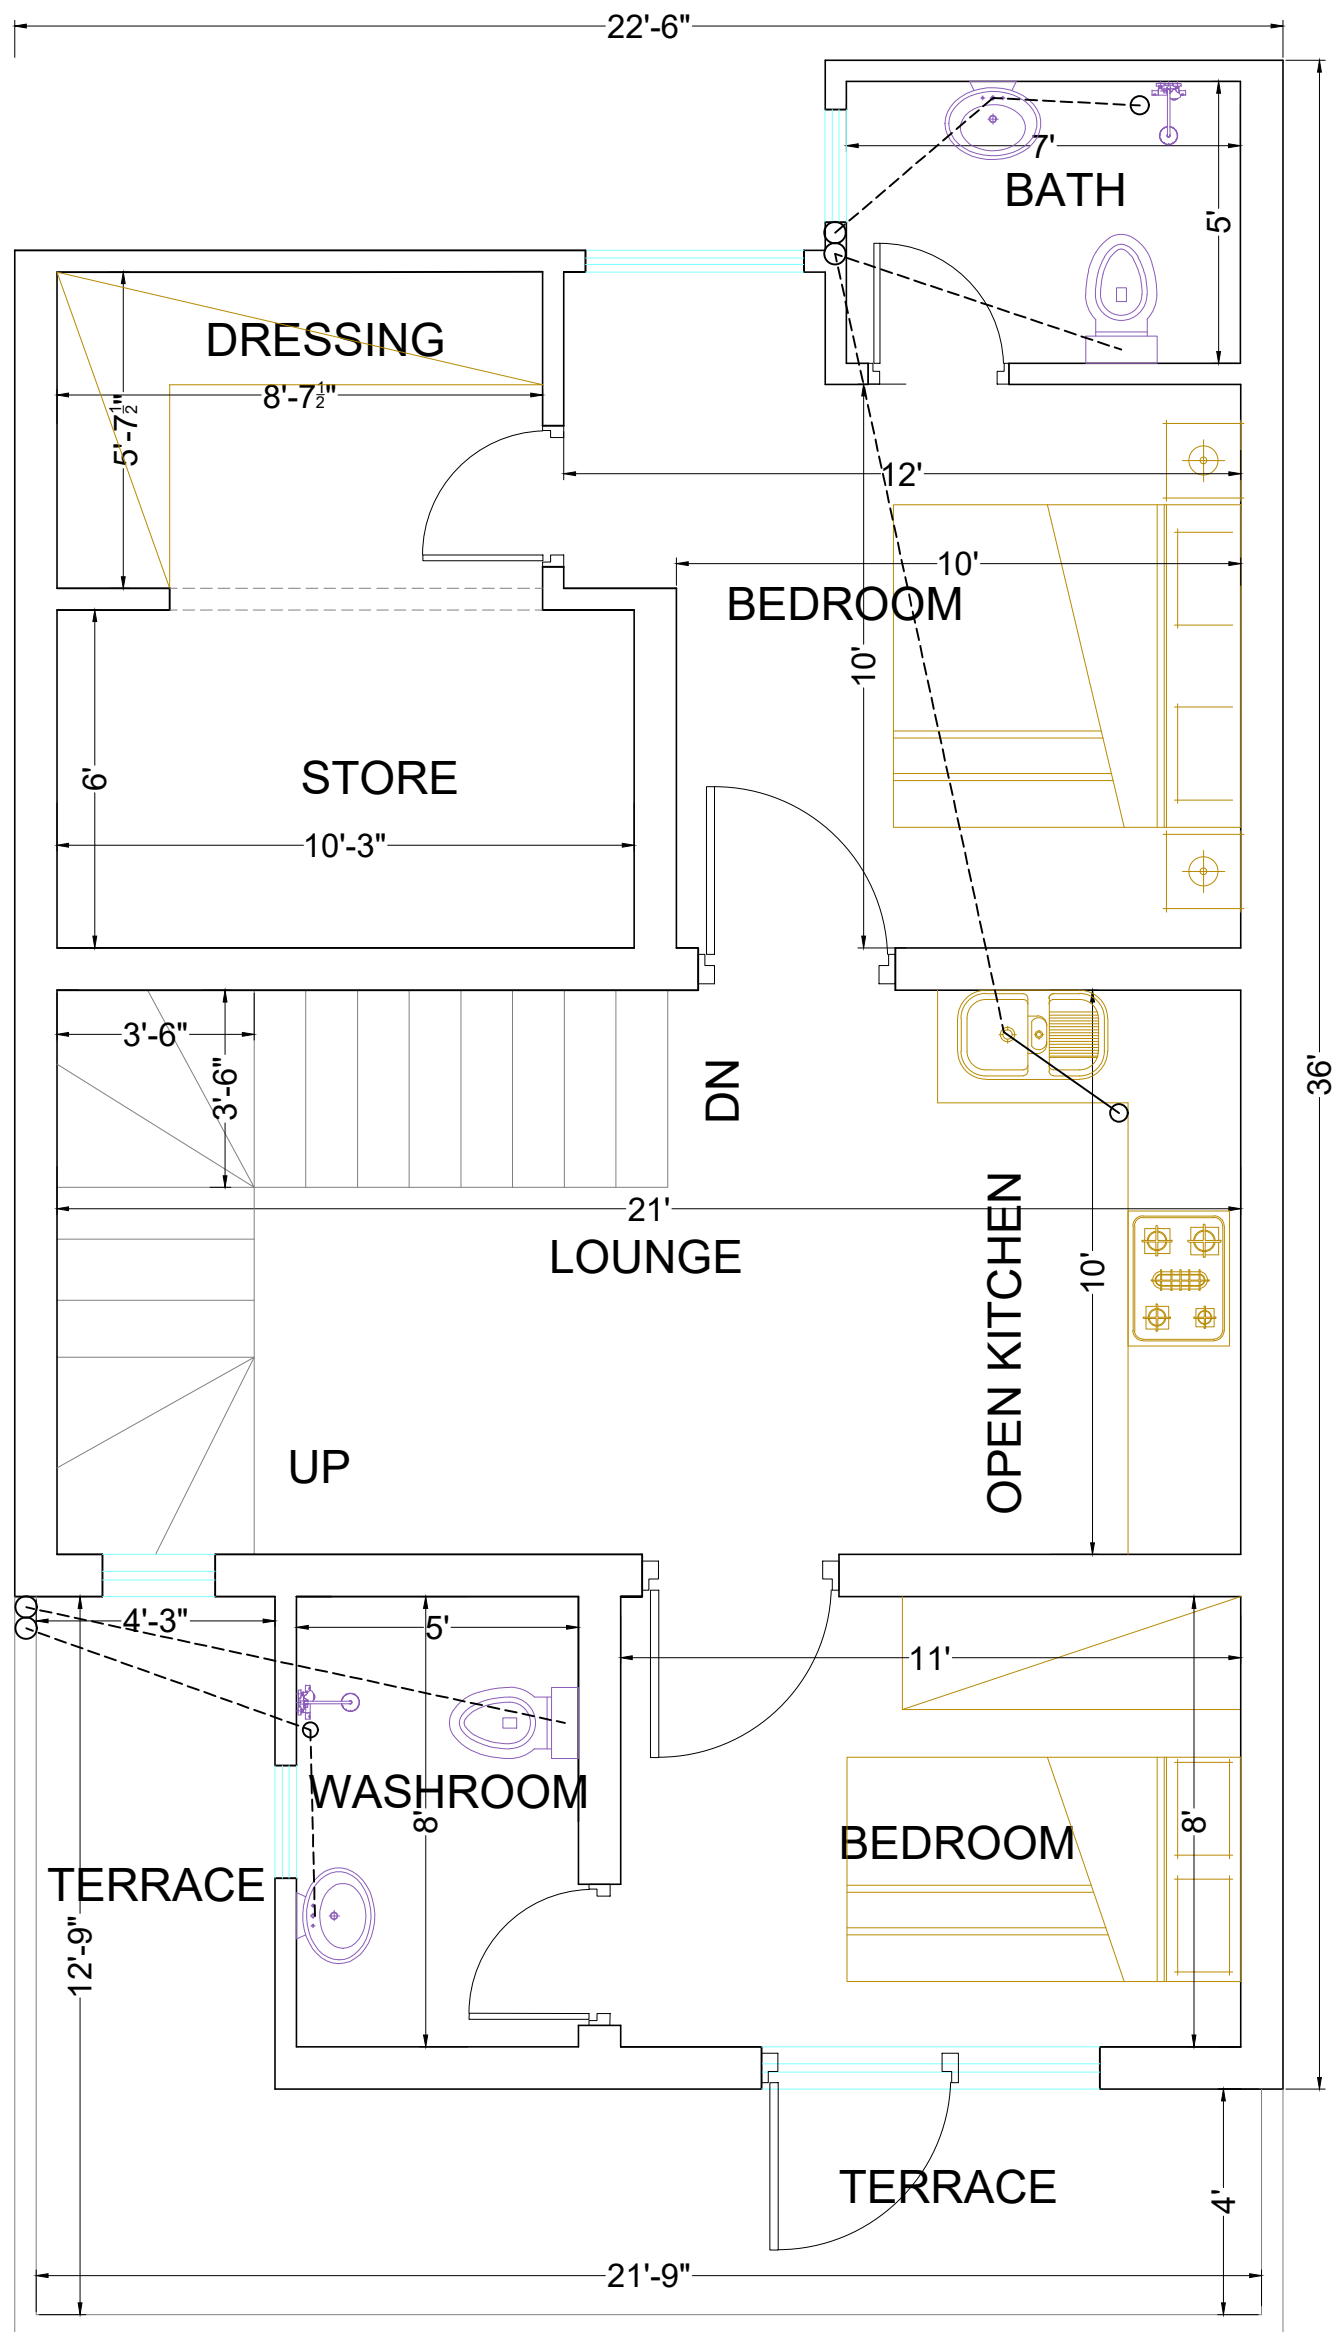


FIRST SEWER FLOOR
SOHAIL RASHID
HASSAN BLOCK
PLOT NO 12 22'-6"x40'
ALI HOUSING SCHEME, LAHORE



SALMAN AMJAD AND ASSOCIATES:

APPROVED AS CATEGORY-A ARCHITECT LDA.
 REGISTERED PCATP-06011 AND LDA TPRA-298
 OFFICE NO. FIRST FLOOR, MUSTAFA TOWN,
 HIDAYATULLAH STREET, LAHORE
 MOBILE NO → 0306-4706139

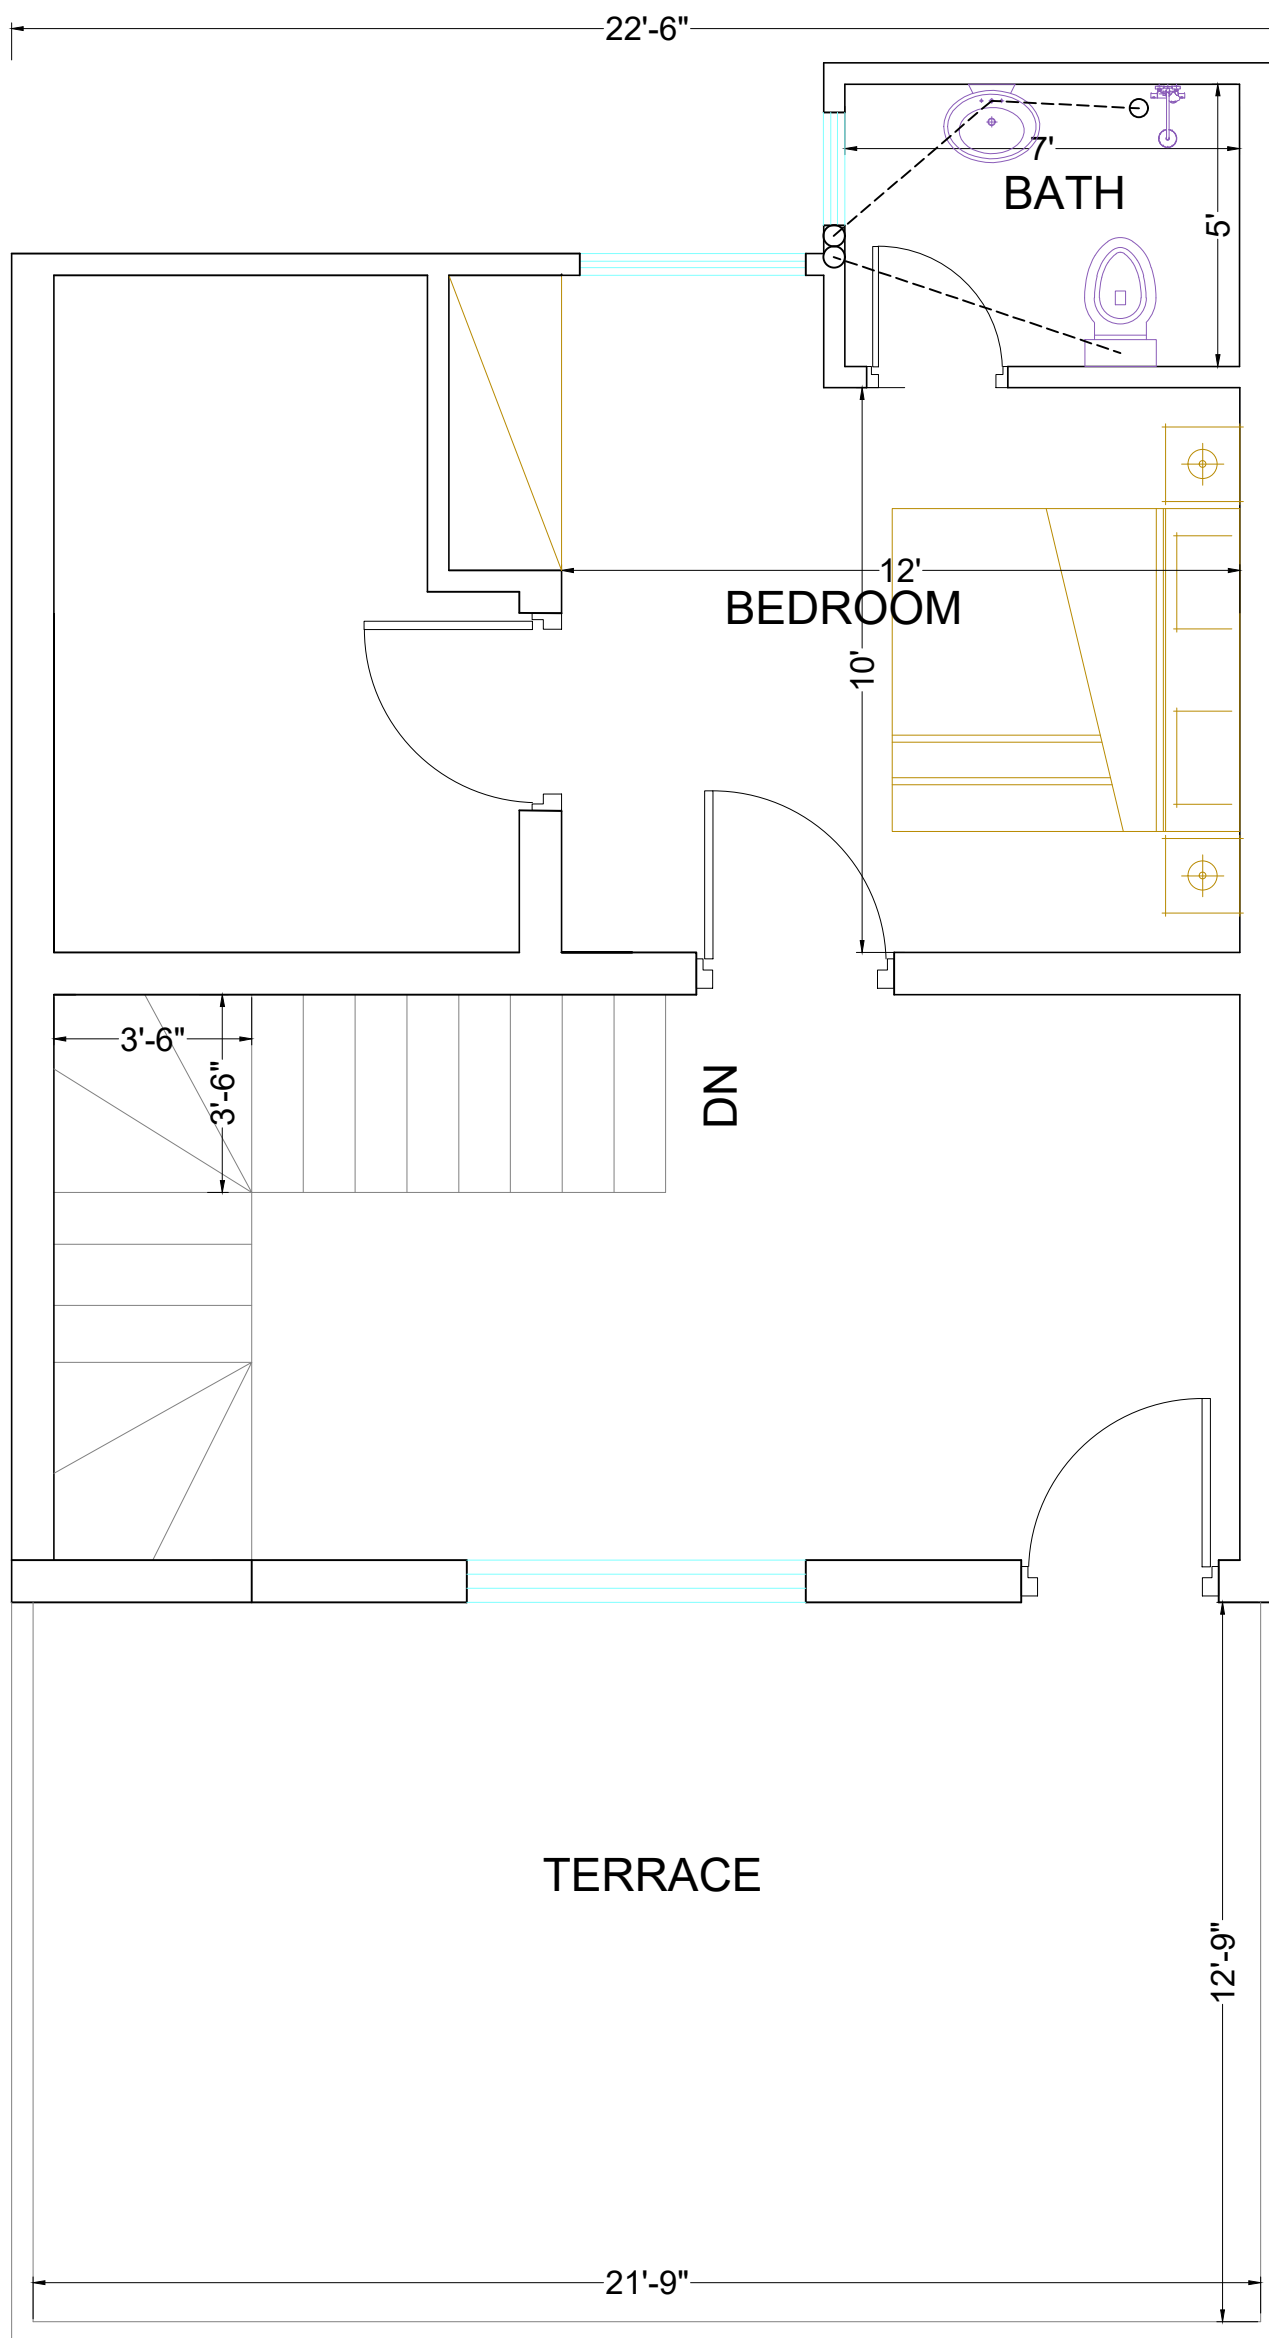


SECOND SEWER FLOOR
SOHAIL RASHID
HASSAN BLOCK
PLOT NO 12 22'-6"x40'
ALI HOUSING SCHEME, LAHORE



SALMAN AMJAD AND ASSOCIATES:

APPROVED AS CATEGORY-A ARCHITECT LDA.
REGISTERED PCATP-06011 AND LDA TPRA-298
OFFICE NO. FIRST FLOOR, MUSTAFA TOWN,
HIDAYATULLAH STREET, LAHORE
MOBILE NO → 0306-4706139

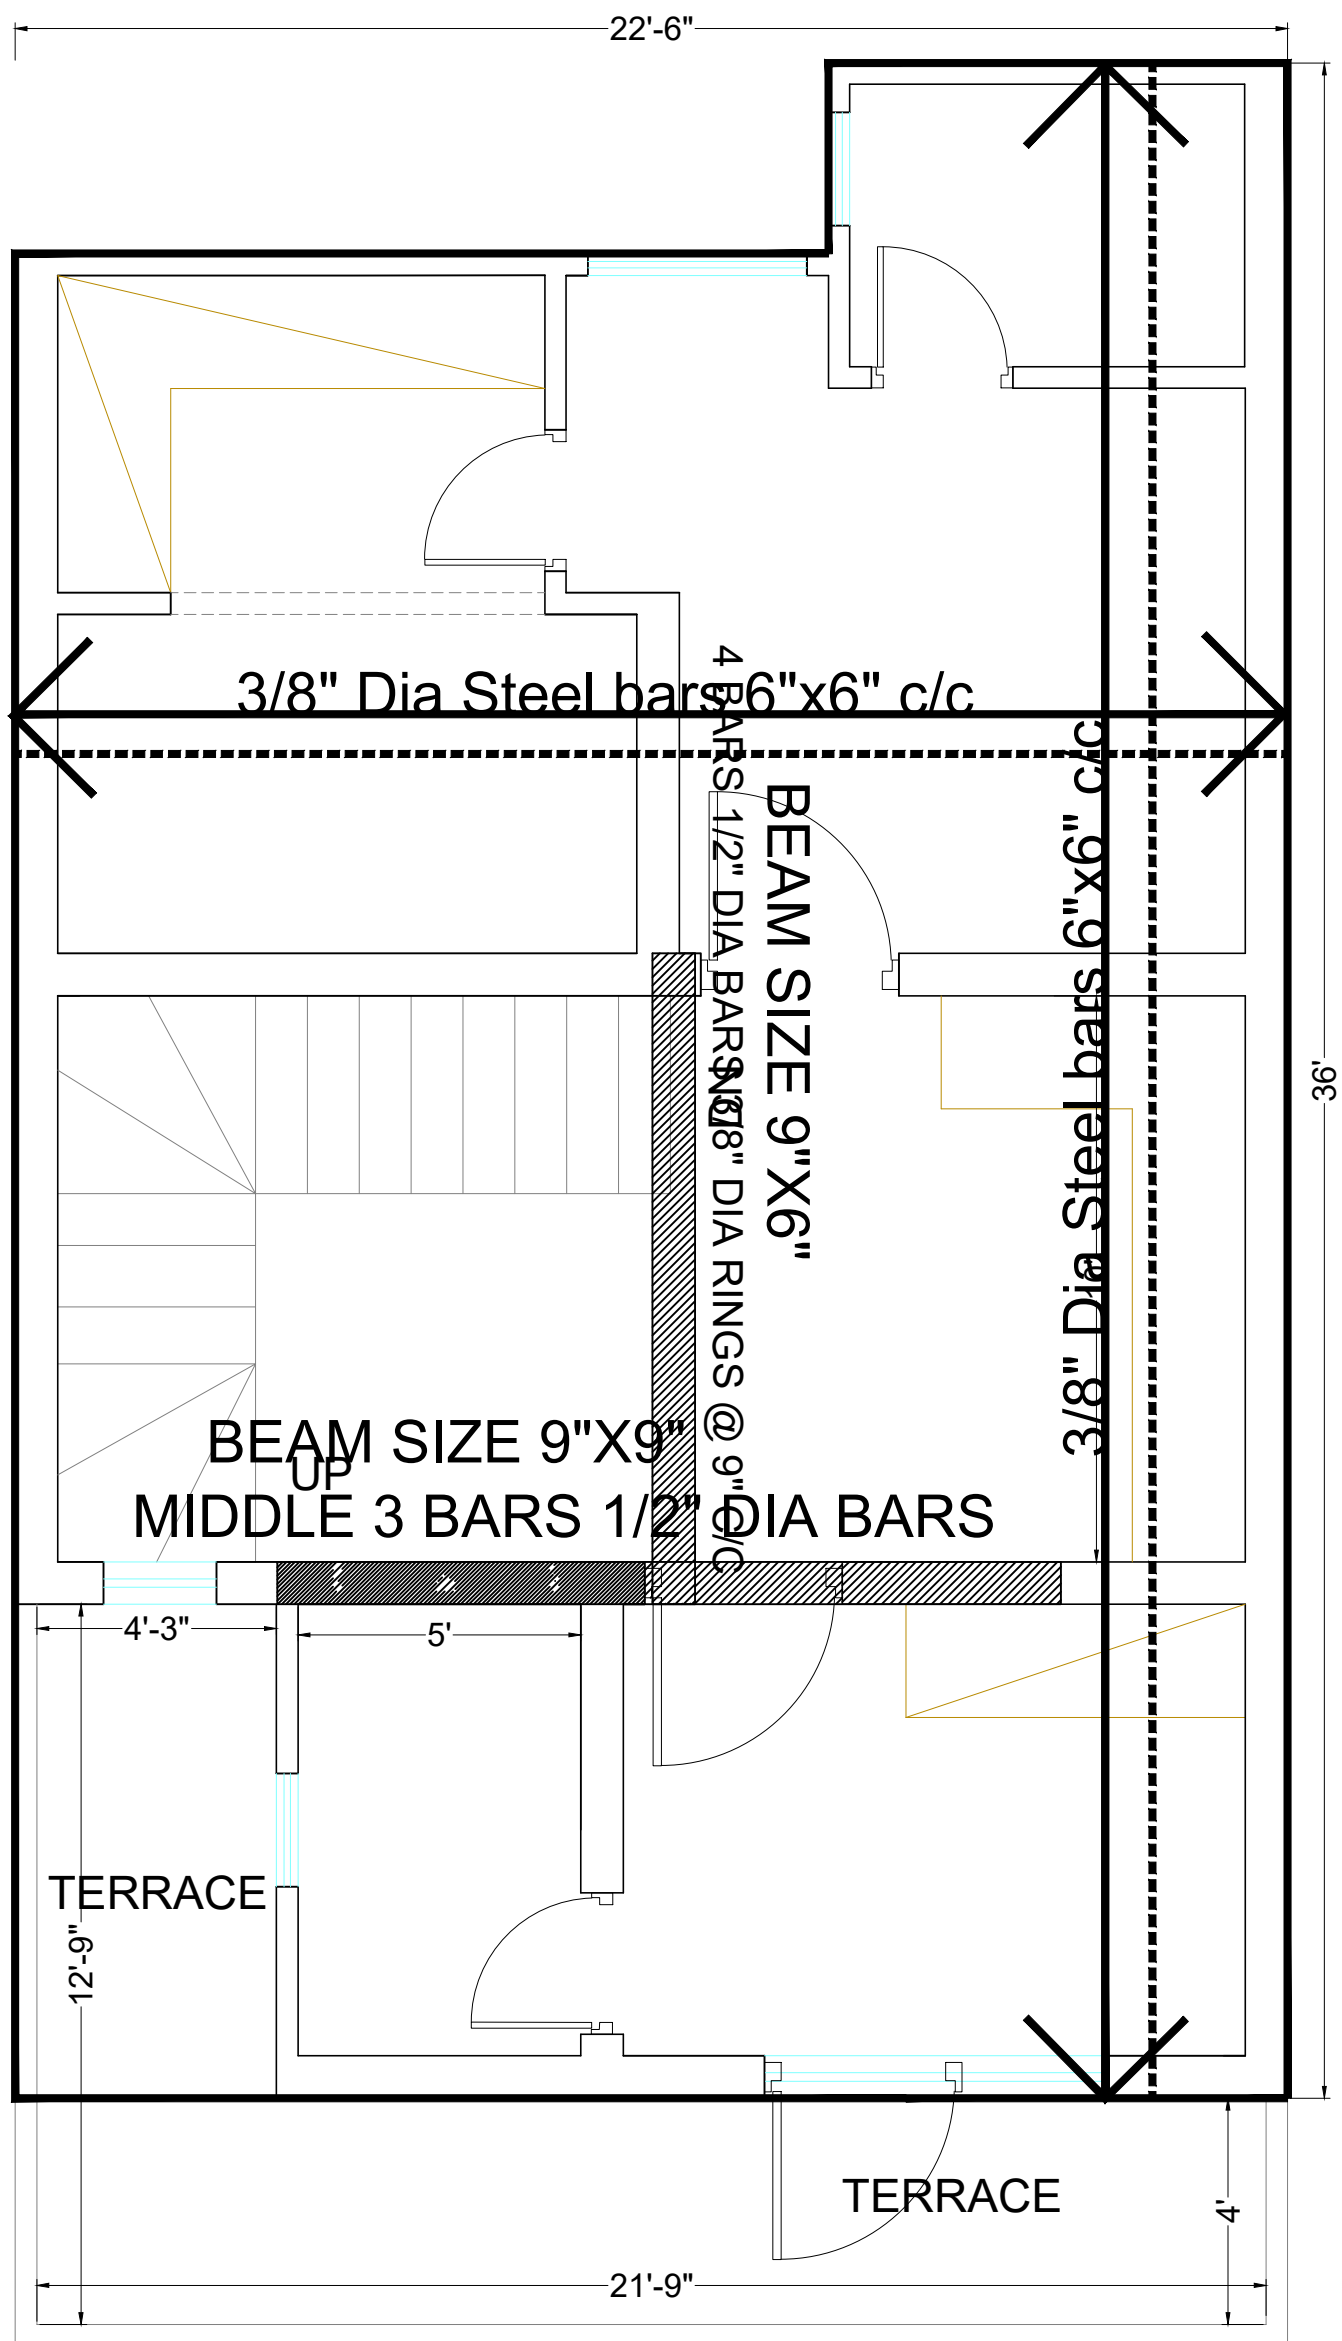


FIRST FLOOR STRUCTURE PLAN
SOHAIL RASHID
HASSAN BLOCK
PLOT NO 12 22'-6"x40'
ALI HOUSING SCHEME, LAHORE



SALMAN AMJAD AND ASSOCIATES:

APPROVED AS CATEGORY-A ARCHITECT LDA.
REGISTERED PCATP-06011 AND LDA TPRA-298
OFFICE NO. FIRST FLOOR, MUSTAFA TOWN,
HIDAYATULLAH STREET, LAHORE
MOBILE NO → 0306-4706139

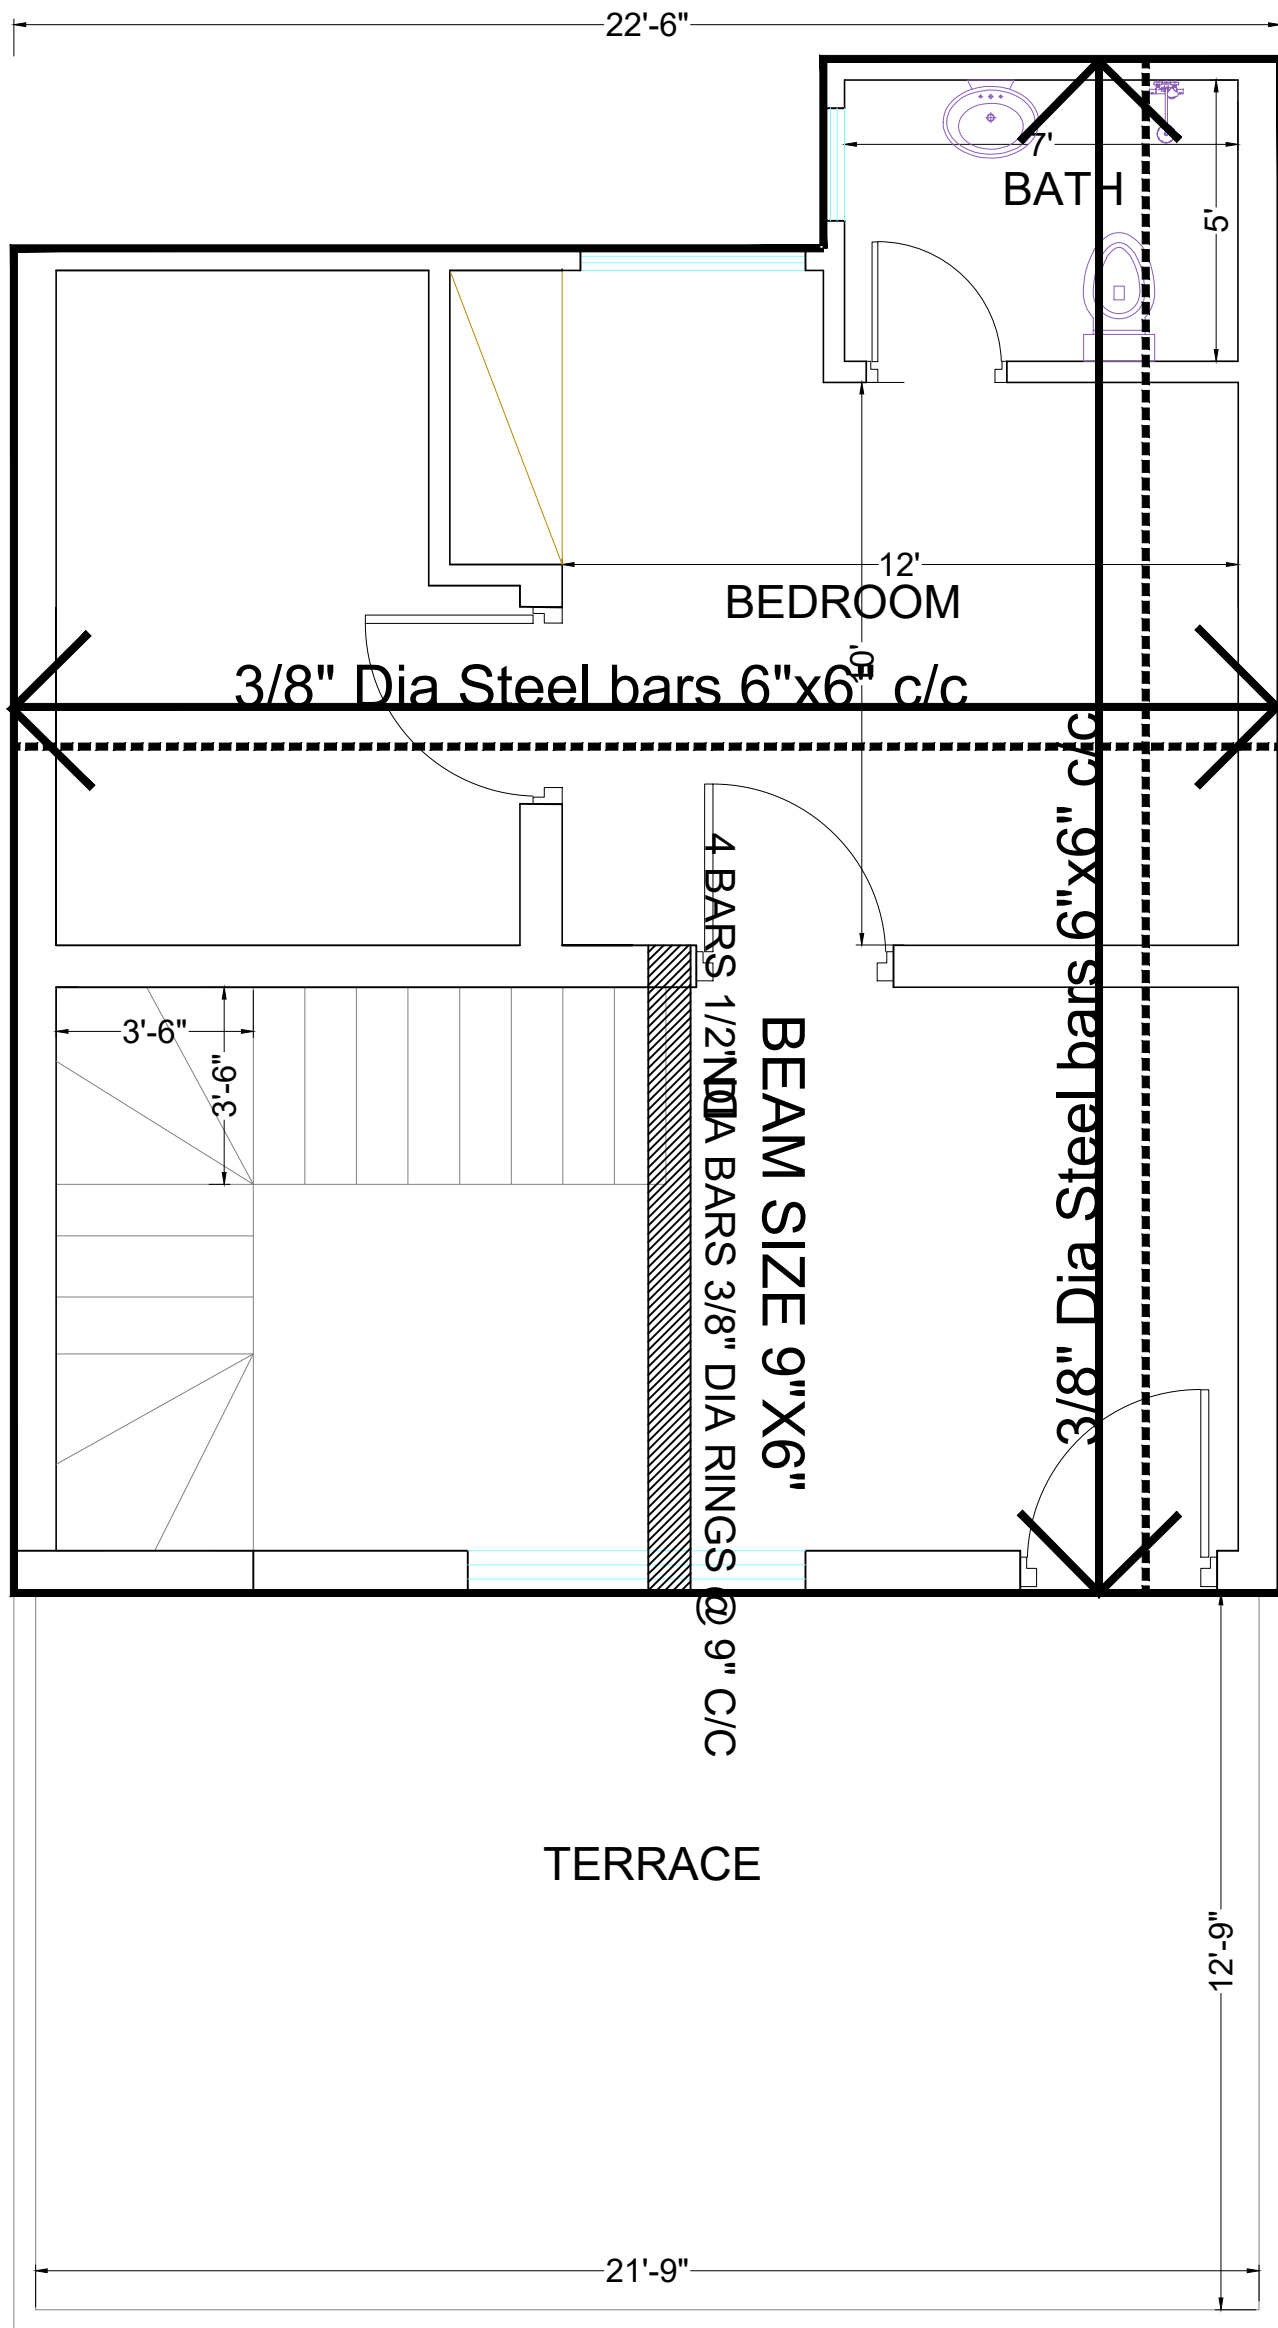

SECOND FLOOR STRUCTURE PLAN
SOHAIL RASHID
HASSAN BLOCK
PLOT NO 12 22'-6"x40'
ALI HOUSING SCHEME, LAHORE



SALMAN AMJAD AND ASSOCIATES:

APPROVED AS CATEGORY-A ARCHITECT LDA.
REGISTERED PCATP-06011 AND LDA TPRA-298
OFFICE NO. FIRST FLOOR, MUSTAFA TOWN,
HIDAYATULLAH STREET, LAHORE
MOBILE NO → 0306-4706139