


MR.IJAZ
10 MARLA
GROUND FLOOR
SABZAR LAHORE

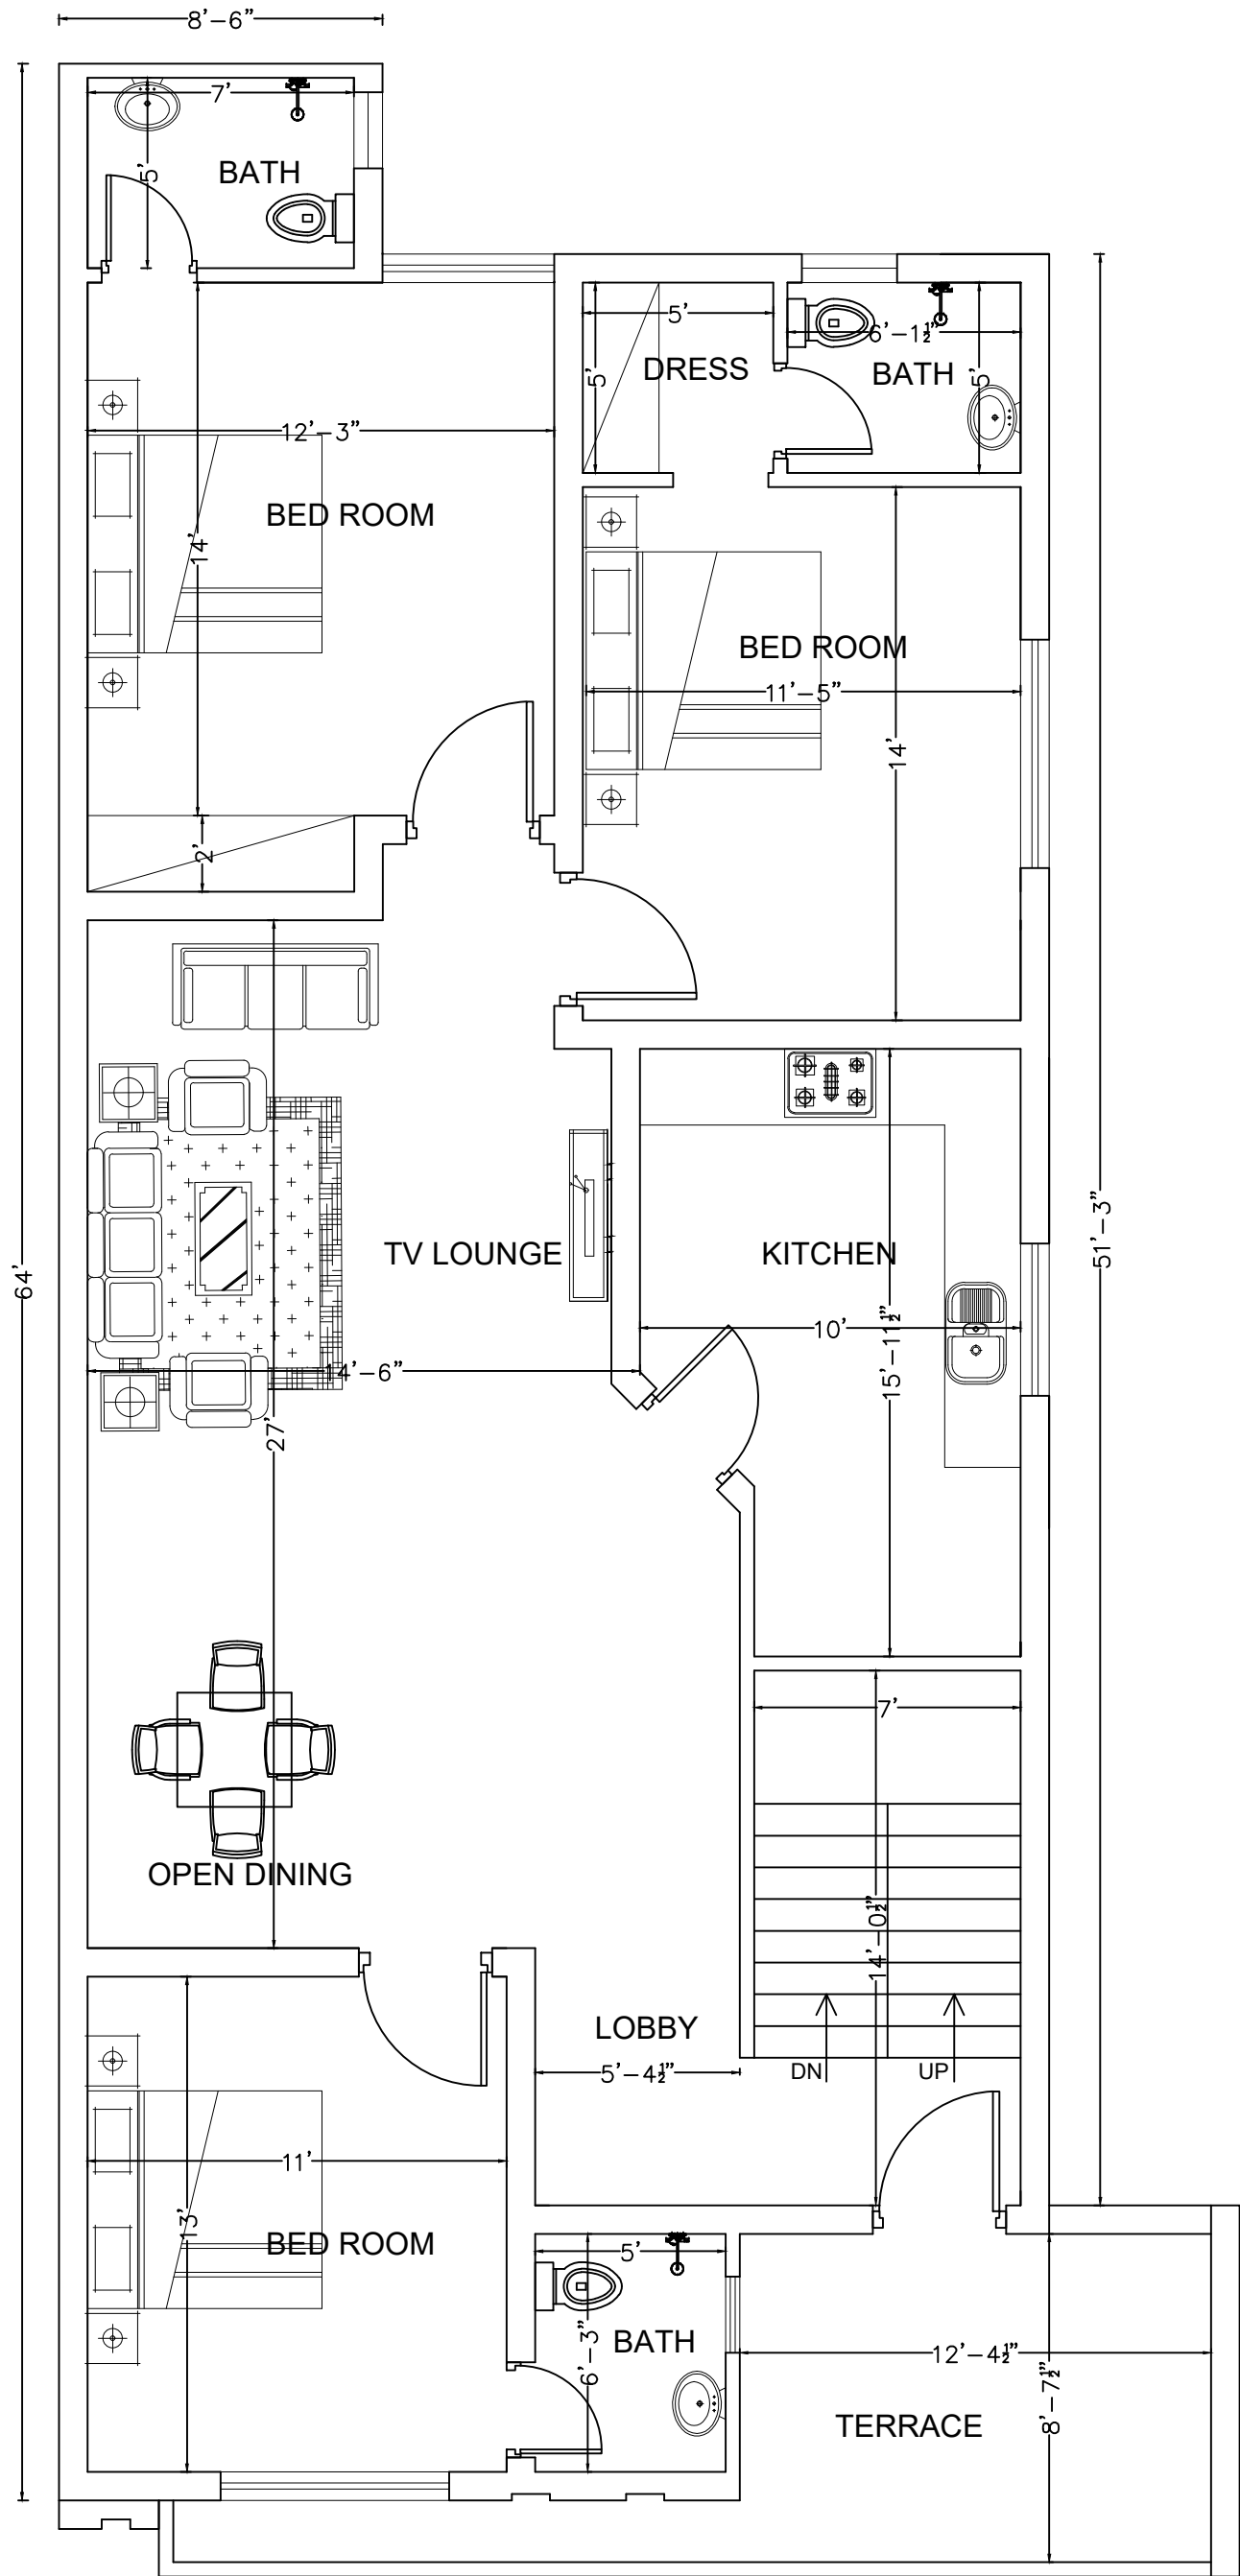

SALMAN AMJAD AND ASSOCIATES:

ARCHITECT, INTERIOR DESIGN, CONSTRUCTION.
APPROVED AS CATEGORY-A ARCHITECT LDA
REGISTERED PCATP-06011 AND LDA TPRA-298
OFFICE NO. 35 GROUND FLOOR, MIAN PLAZA,
JOHAR TOWN, LAHORE Mobile no. : 0306-4706139




MR.IJAZ
10 MARLA
FIRST FLOOR
SABZAR LAHORE



SALMAN AMJAD AND ASSOCIATES:

ARCHITECT, INTERIOR DESIGN, CONSTRUCTION.
APPROVED AS CATEGORY-A ARCHITECT LDA.
REGISTERED PCATP-06011 AND LDA TPRA-298
OFFICE NO. 35 GROUND FLOOR, MIAN PLAZA,
JOHAR TOWN, LAHORE Mobile no. : 0306-4706139

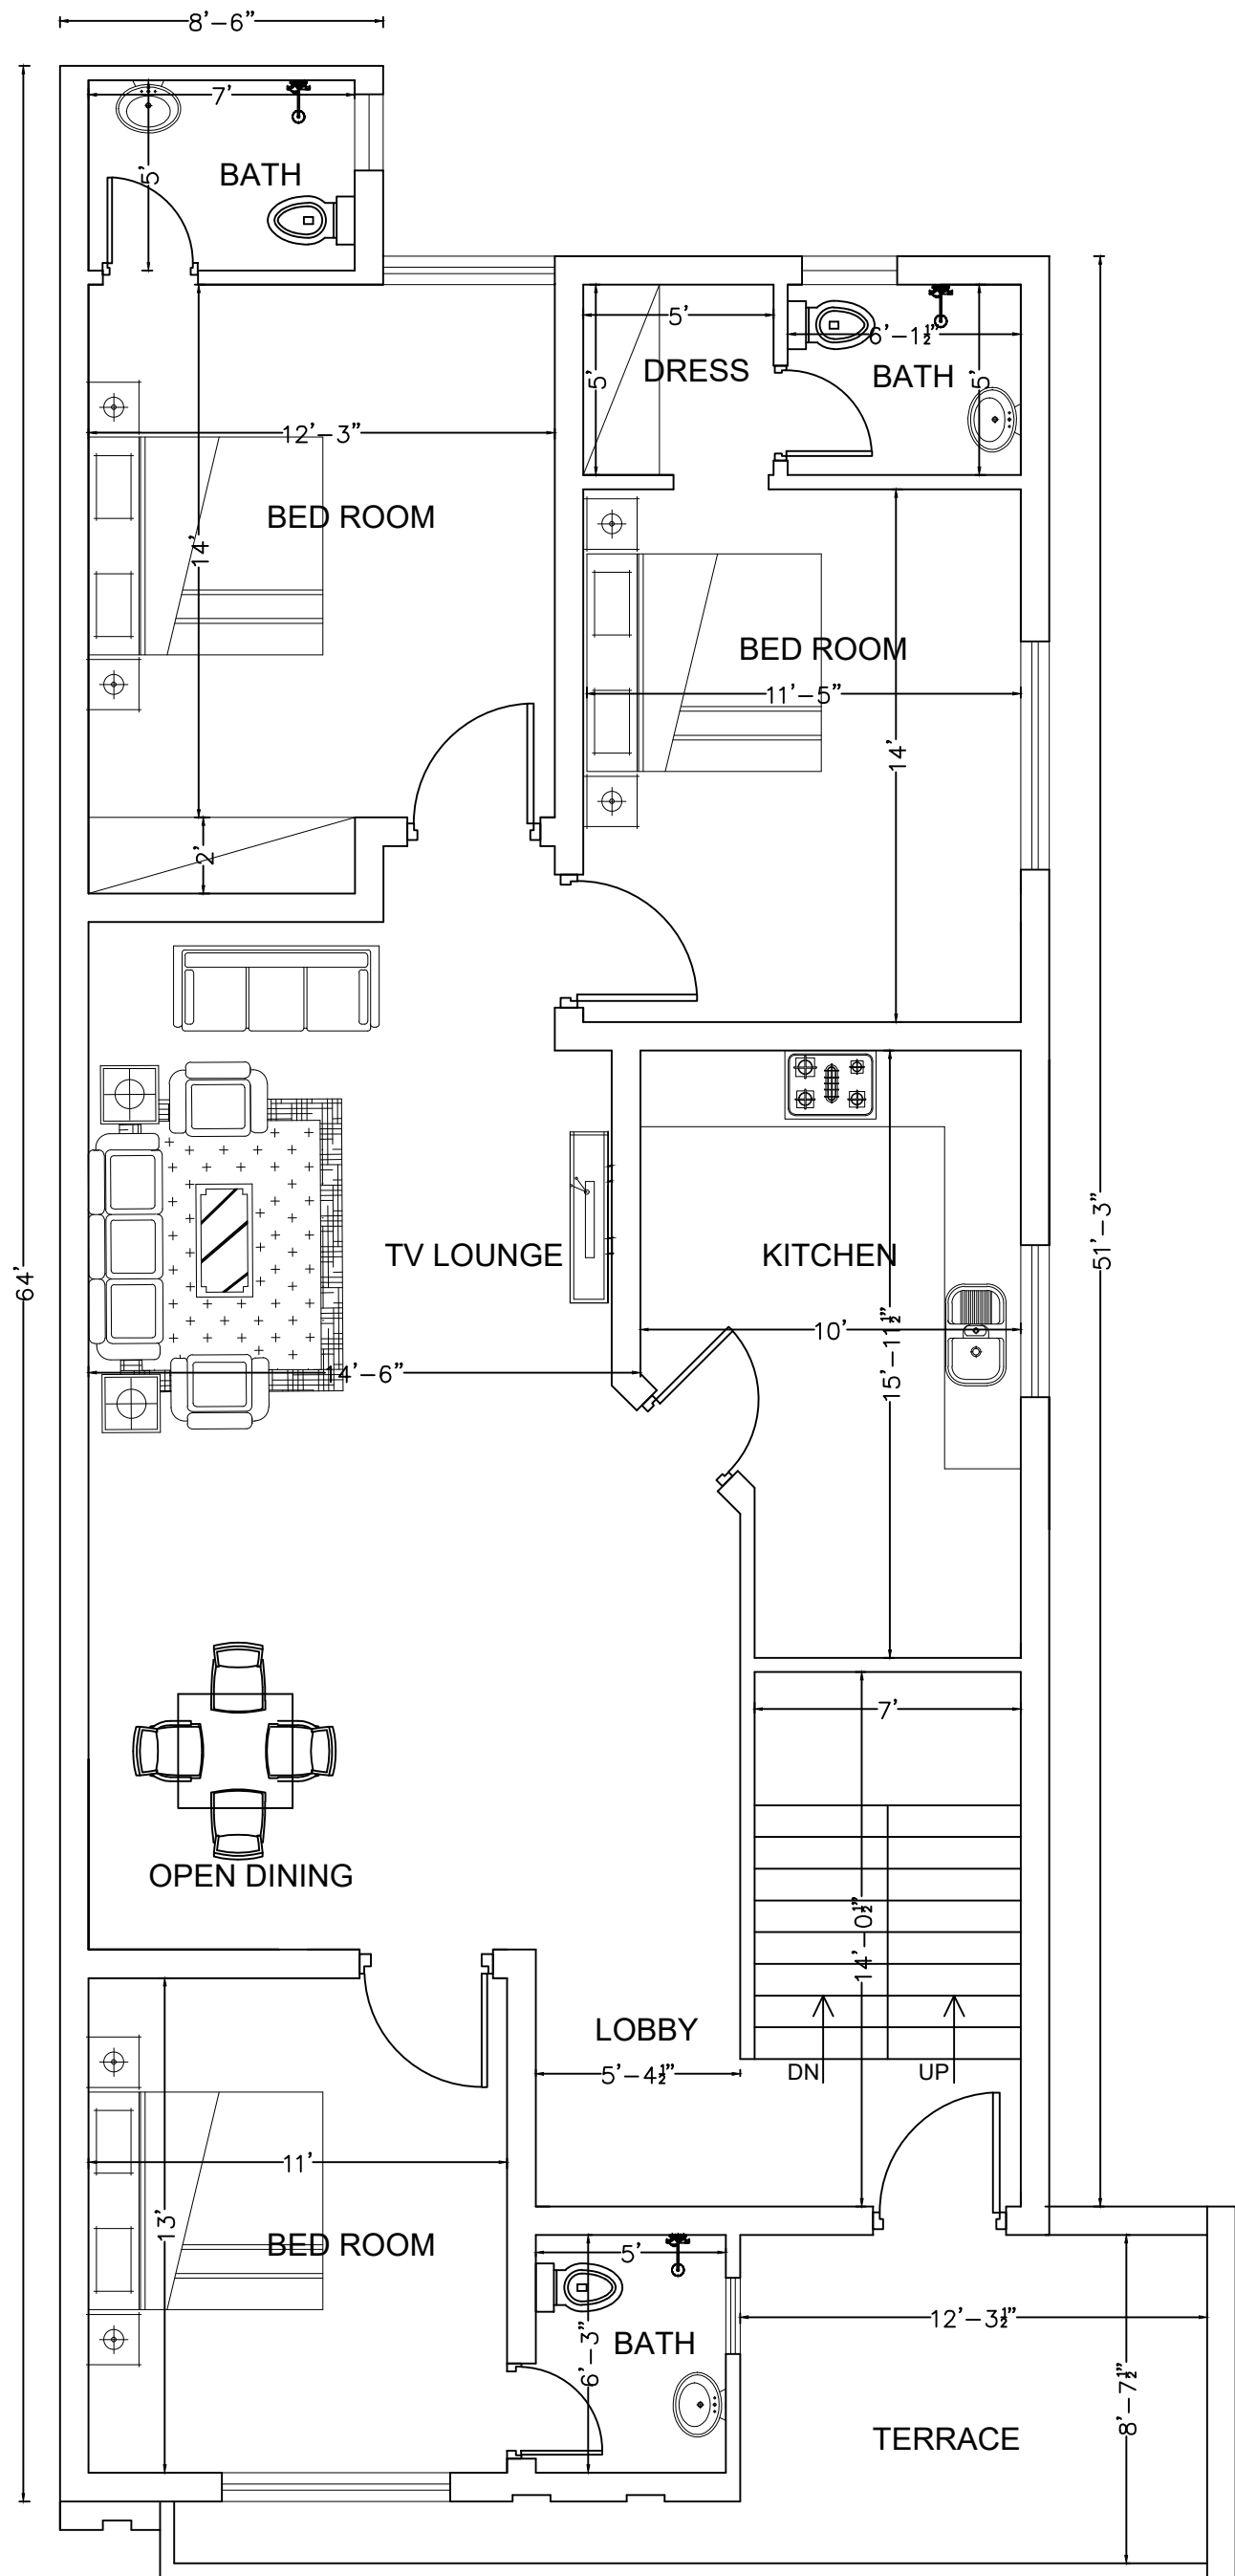


MR.IJAZ
10 MARLA
SECOND FLOOR
SABZAR LAHORE



SALMAN AMJAD AND ASSOCIATES:

ARCHITECT, INTERIOR DESIGN, CONSTRUCTION.
APPROVED AS CATEGORY-A ARCHITECT LDA.
REGISTERED PCATP-06011 AND LDA TPRA-298
OFFICE NO. 35 GROUND FLOOR, MIAN PLAZA,
JOHAR TOWN, LAHORE Mobile no. : 0306-4706139

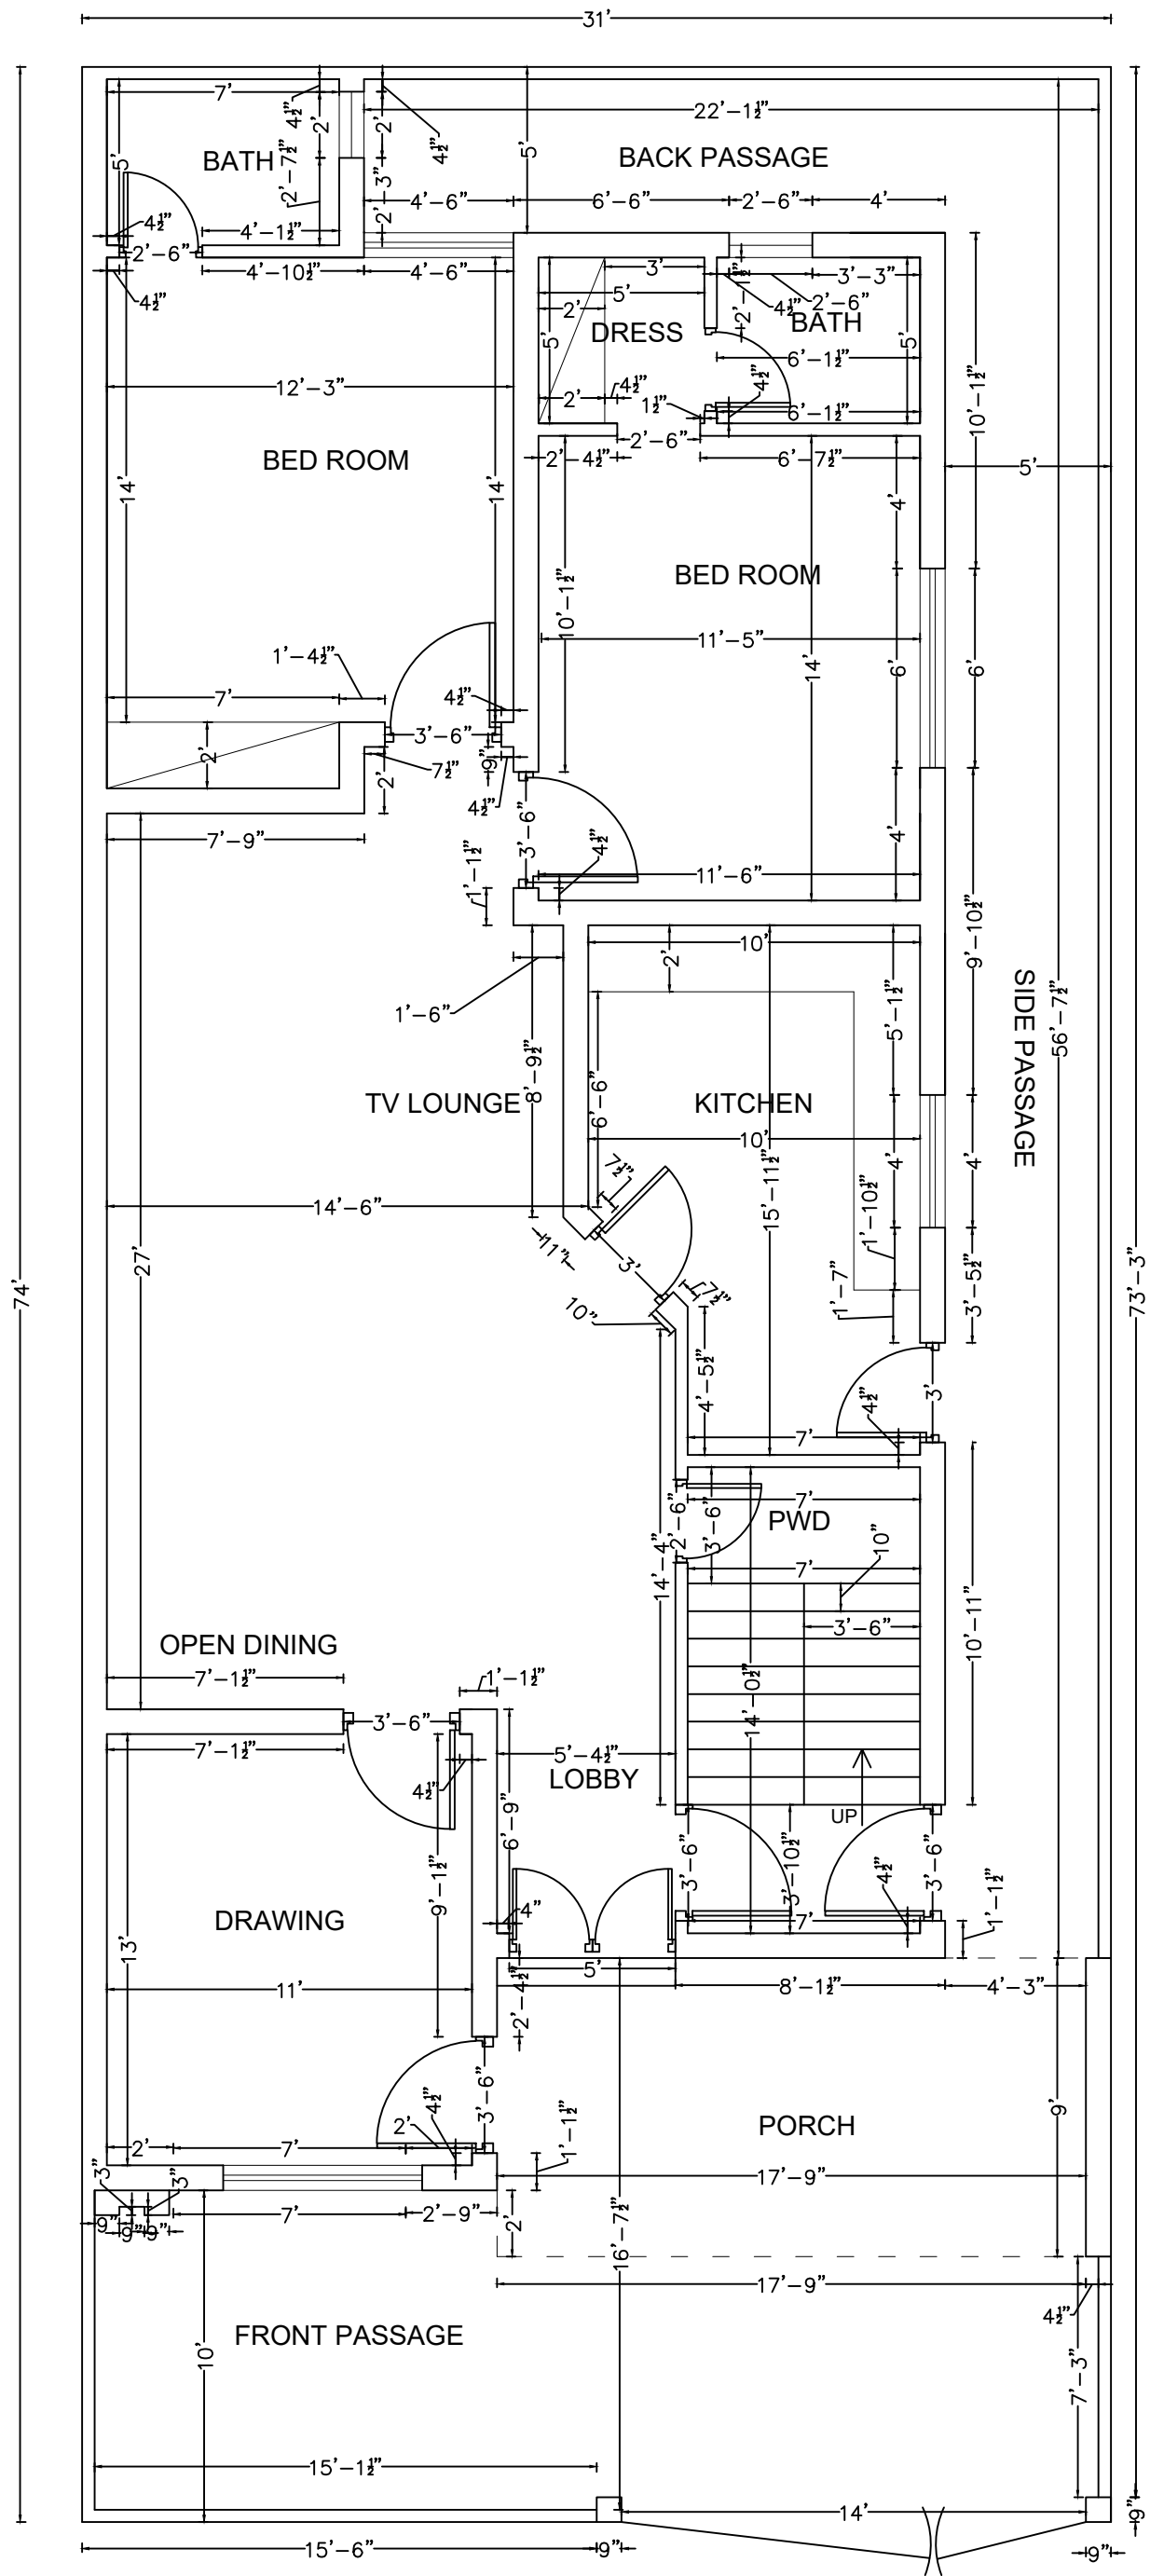


MR.IJAZ
10 MARLA
WORKING GROUND FLOOR
SABZAR LAHORE



SALMAN AMJAD AND ASSOCIATES:

ARCHITECT, INTERIOR DESIGN, CONSTRUCTION.
APPROVED AS CATEGORY-A ARCHITECT LDA.
REGISTERED PCATP-06011 AND LDA TPRA-298
OFFICE NO. 35 GROUND FLOOR, MIAN PLAZA,
JOHAR TOWN, LAHORE Mobile no. : 0306-4706139

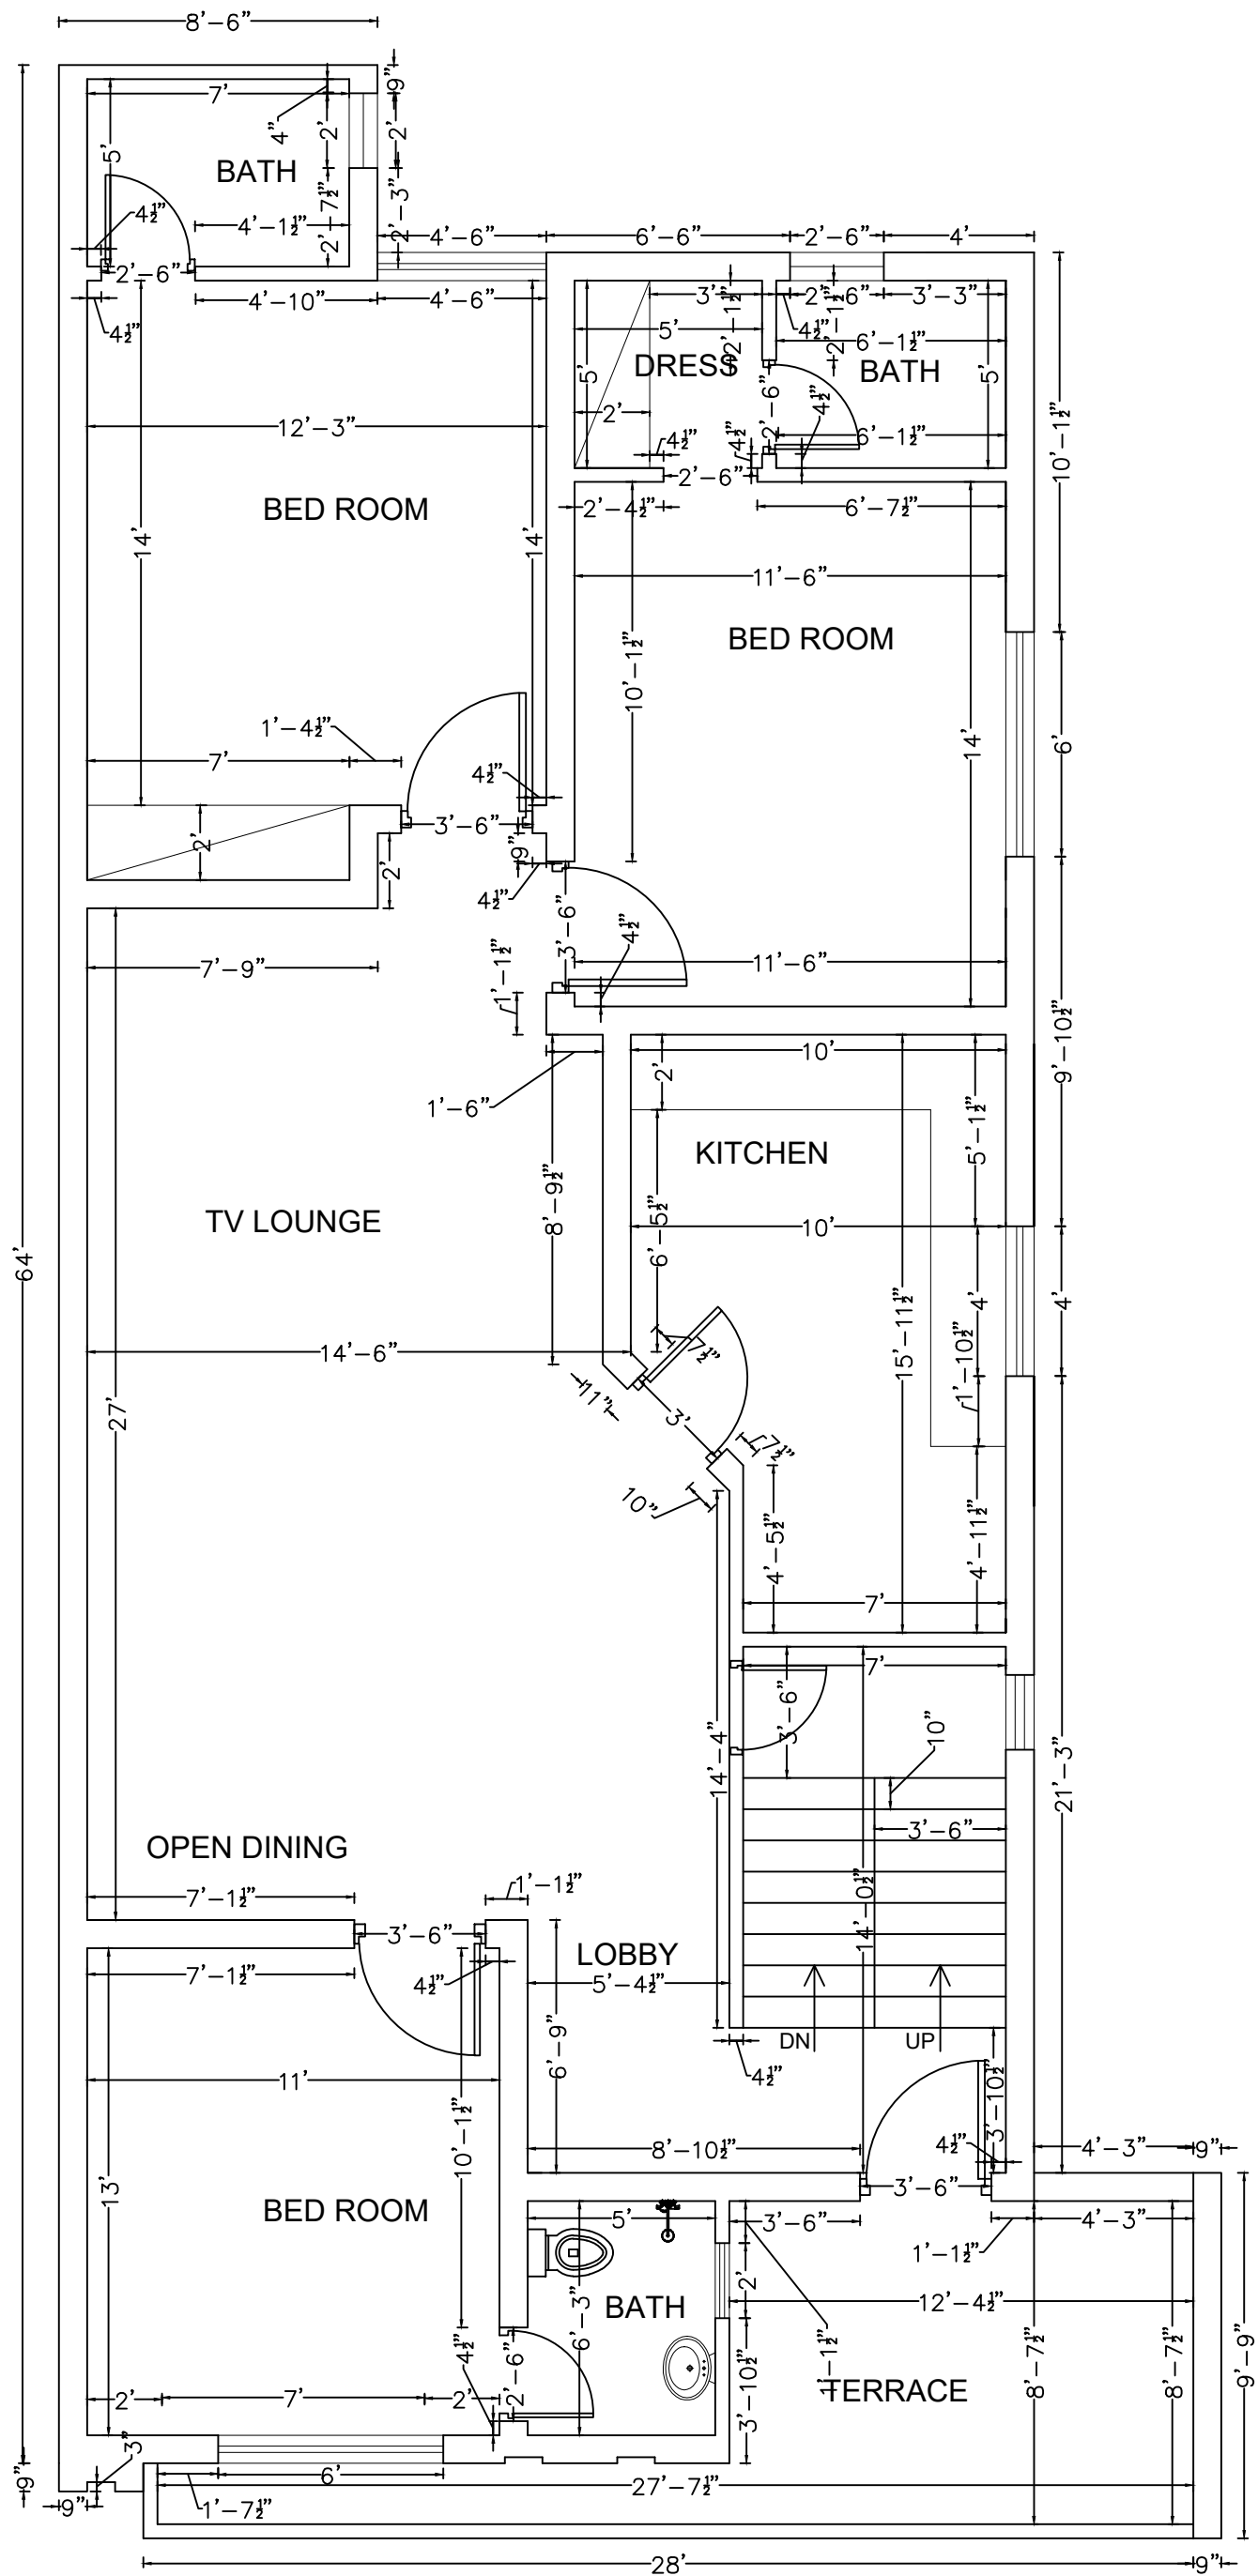


MR.IJAZ
10 MARLA
WORKING FIRST FLOOR
SABZAR LAHORE



SALMAN AMJAD AND ASSOCIATES:

ARCHITECT, INTERIOR DESIGN, CONSTRUCTION.
APPROVED AS CATEGORY-A ARCHITECT LDA.
REGISTERED PCATP-06011 AND LDA TPRA-298
OFFICE NO. 35 GROUND FLOOR, MIAN PLAZA,
JOHAR TOWN, LAHORE Mobile no. : 0306-4706139



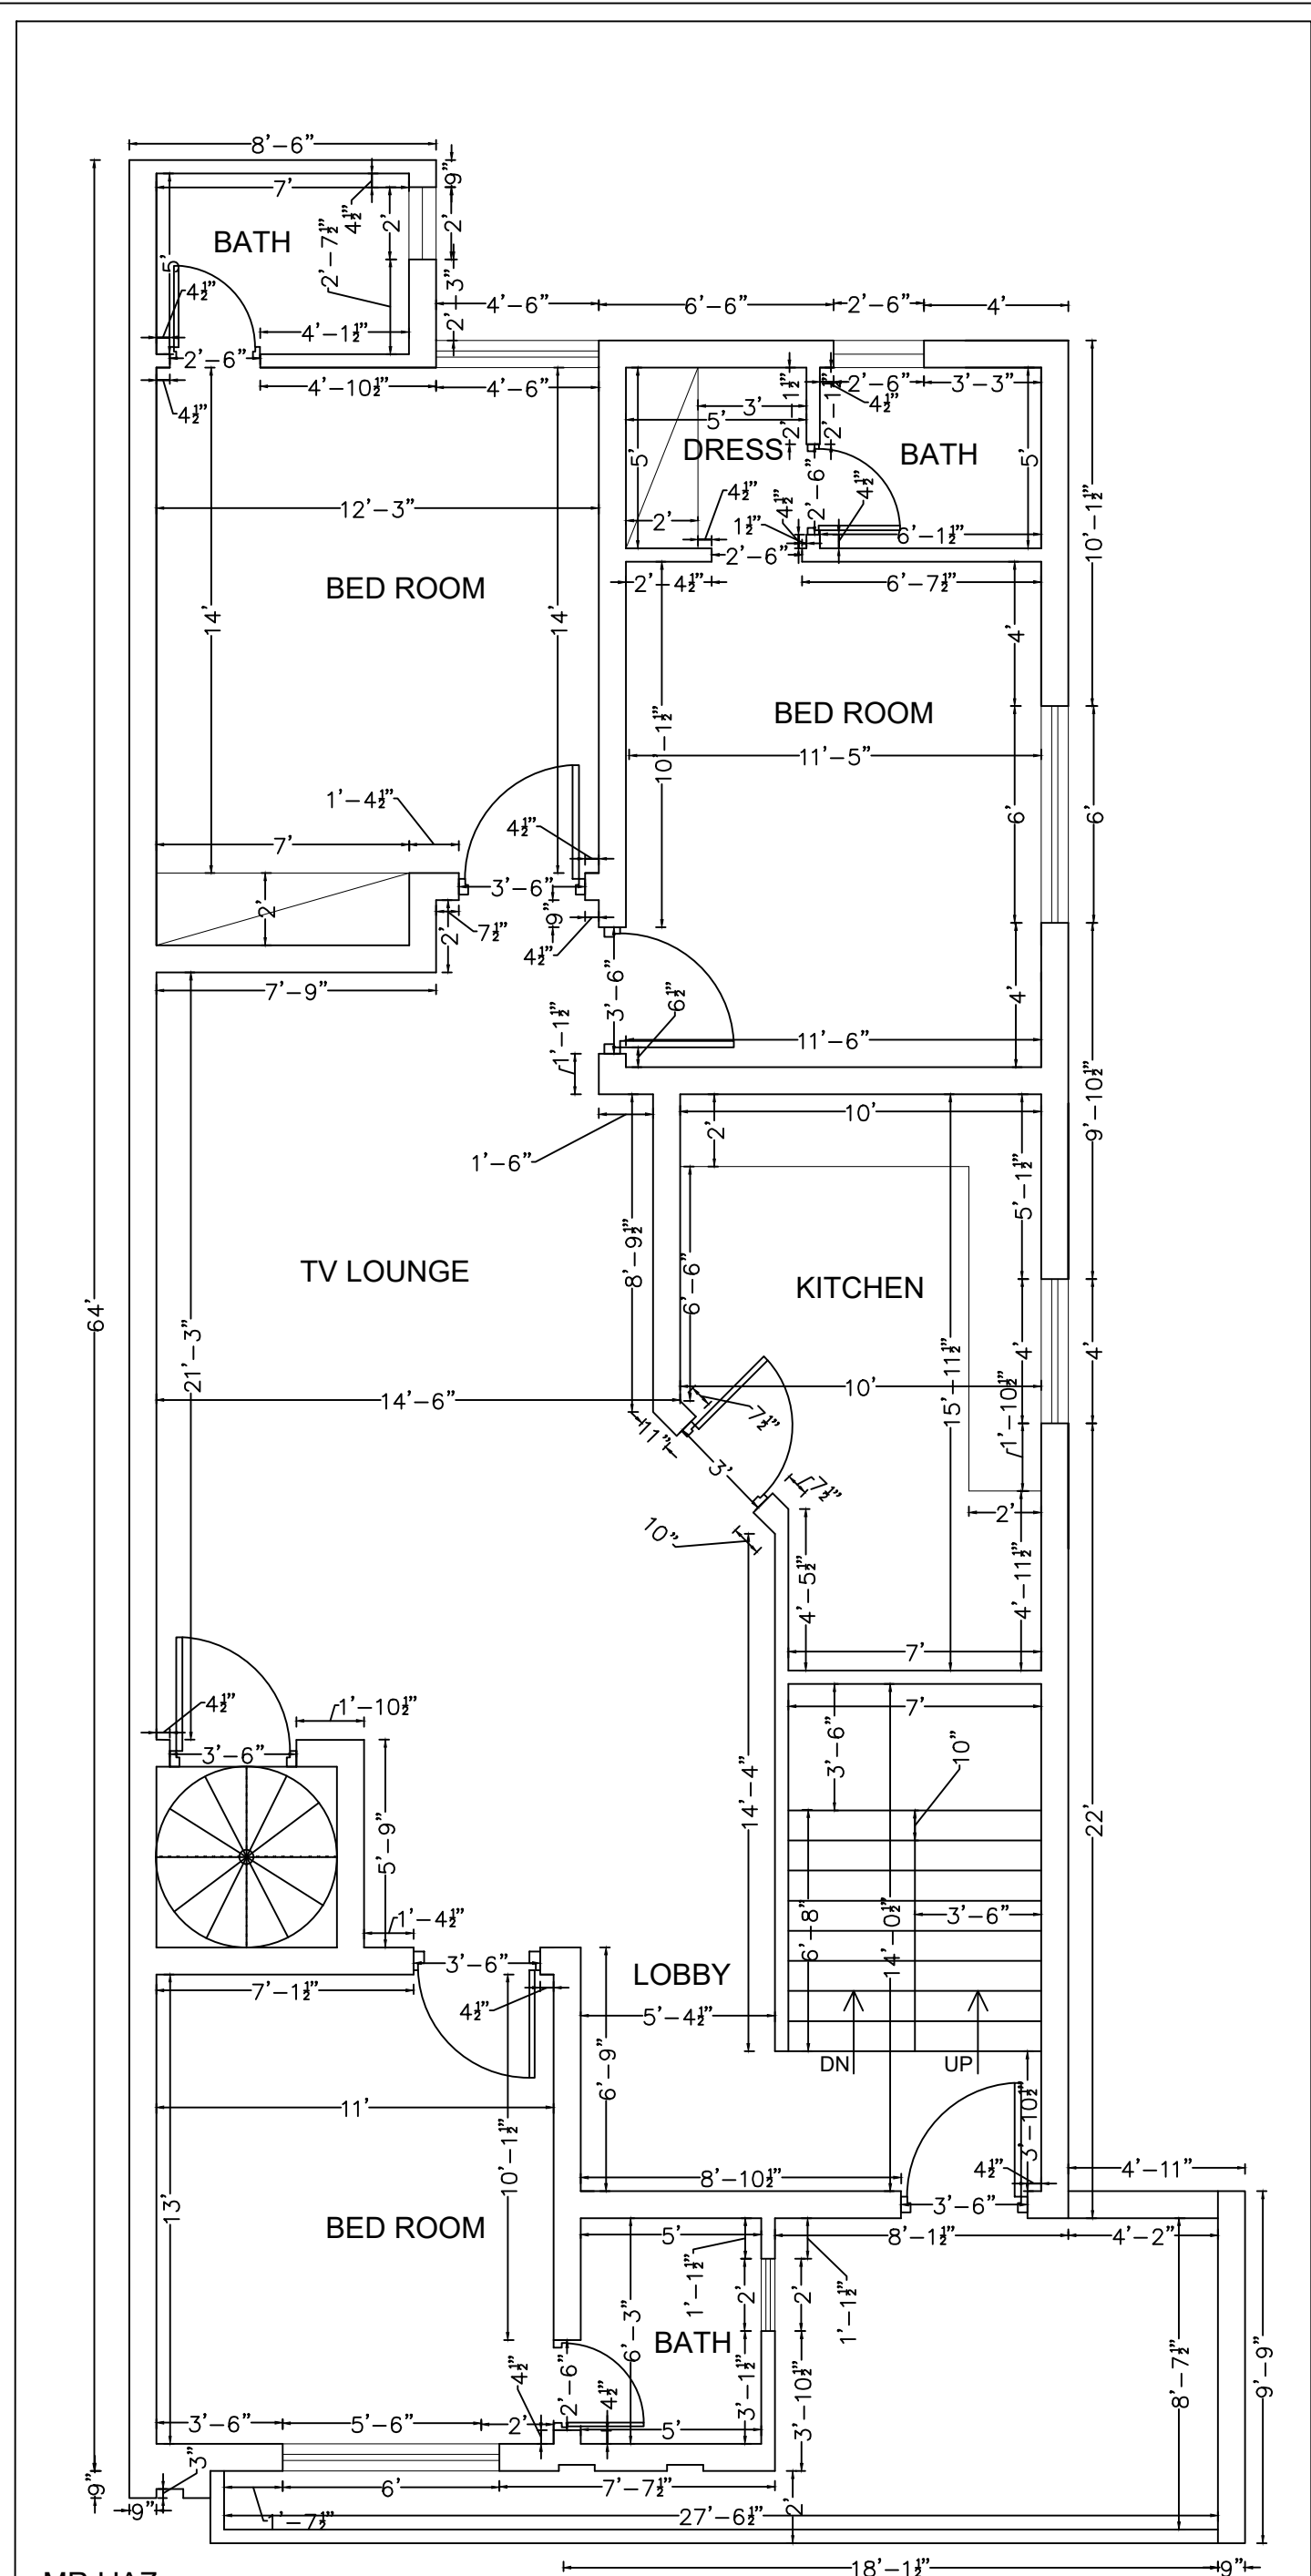















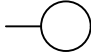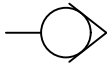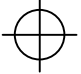


MR.IJAZ
10 MARLA
WORKING SECOND FLOOR
SABZAR LAHORE

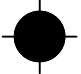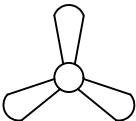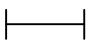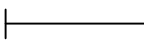


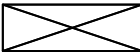SALMAN AMJAD AND ASSOCIATES:

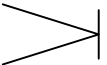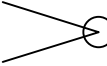ARCHITECT, INTERIOR DESIGN, CONSTRUCTION.
APPROVED AS CATEGORY-A ARCHITECT LDA.
REGISTERED PCATP-06011 AND LDA TPRA-298
OFFICE NO. 35 GROUND FLOOR, MIAN PLAZA,
JOHAR TOWN, LAHORE Mobile no. : 0306-4706139

LEGEND FOR SYMBOLS-ELECTRICAL WORKS		
SIGN.	DESCRIPTION	SILL LEVEL
	WALL LIGHT	8'-0"
	WATER PROOF LIGHT	AS SITE
	CEILING LIGHT	9'-6" OR A.S.
	CHANDILIER LIGHT	9'-6" OR A.S.
	CONCEALED LIGHT	AS SITE
	SPOT LIGHT	9'-6" OR A.S.
	CEILING FAN	9'-6" OR A.S.
	20W SINGLE TUBE LIGHT	AS SITE
	40W SINGLE TUBE LIGHT	8'-0"
	WALL SOCKET	4'-0"
	3 PIN SWITCH	1'-0" OR A.S.
	SPLIT A.C.	8'-0"
	EXHAUST FAN	AS SITE
	DISTRIBUTION BOARD	5'-0"
	T.V. POINT	4'-0"
	TELEPHONE POINT	1'-0"
	GATE INTERCOM	4'-0"
	INTERCOM RECEIVER	4'-0"
	BELL PUSH	4'-0"

ELECTRICAL SCHEDULE

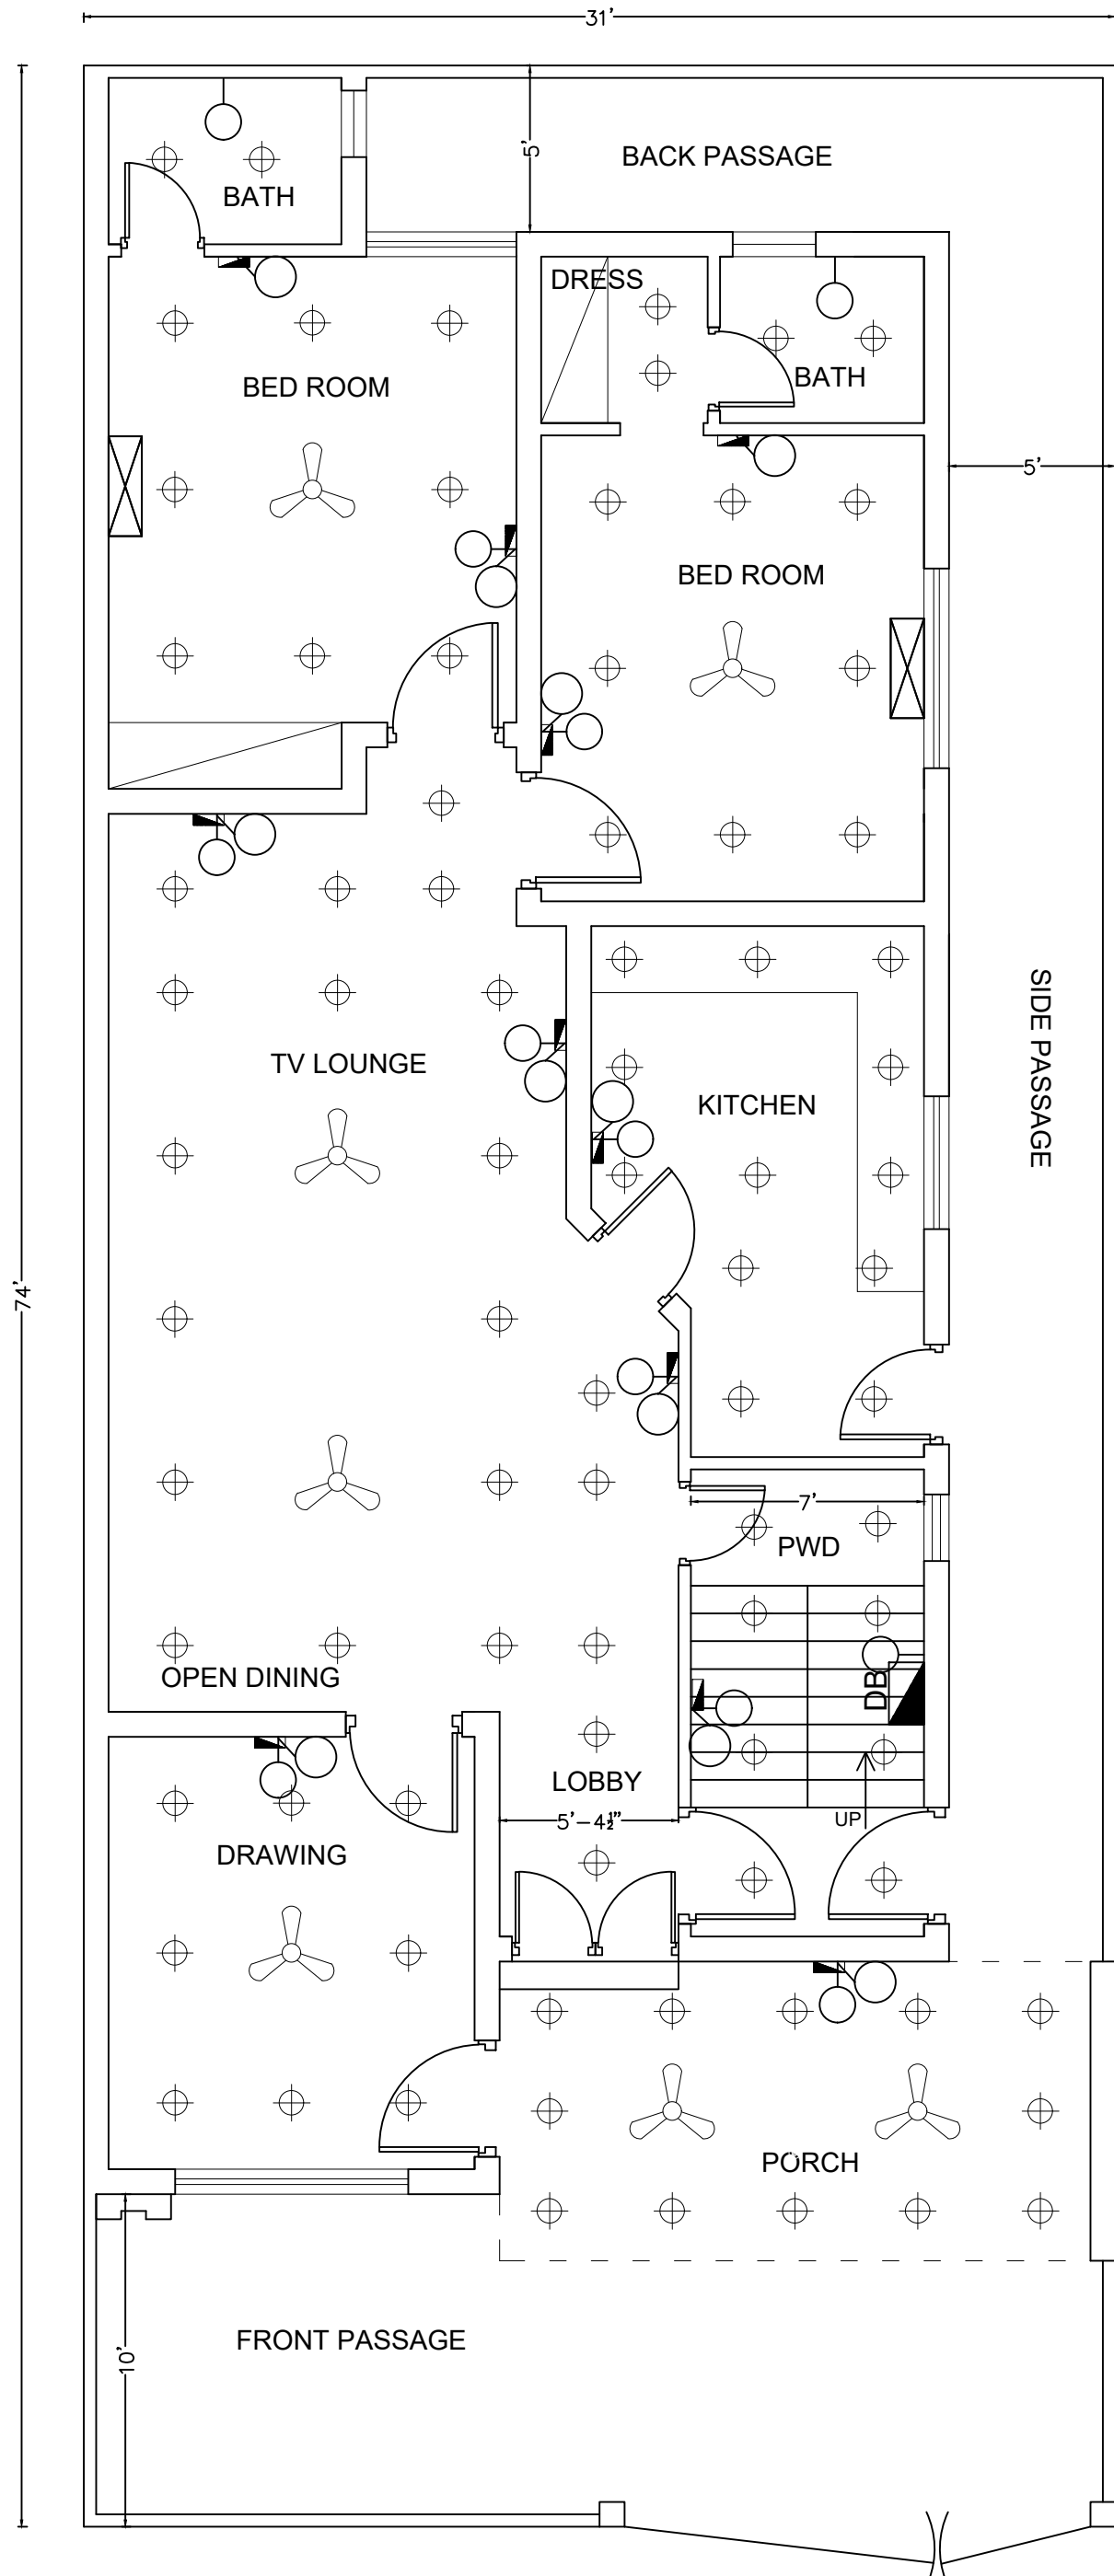


MR.IJAZ
10 MARLA
GROUND FLOOR ELECTRICAL PLAN
SABZAR LAHORE



SALMAN AMJAD AND ASSOCIATES:


ARCHITECT, INTERIOR DESIGN, CONSTRUCTION.
APPROVED AS CATEGORY-A ARCHITECT LDA.
REGISTERED PCATP-060111 AND LDA TPRA-298
OFFICE NO. 35 GROUND FLOOR, MIAN PLAZA,
JOHAR TOWN, LAHORE Mobile no. : 0306-4706139

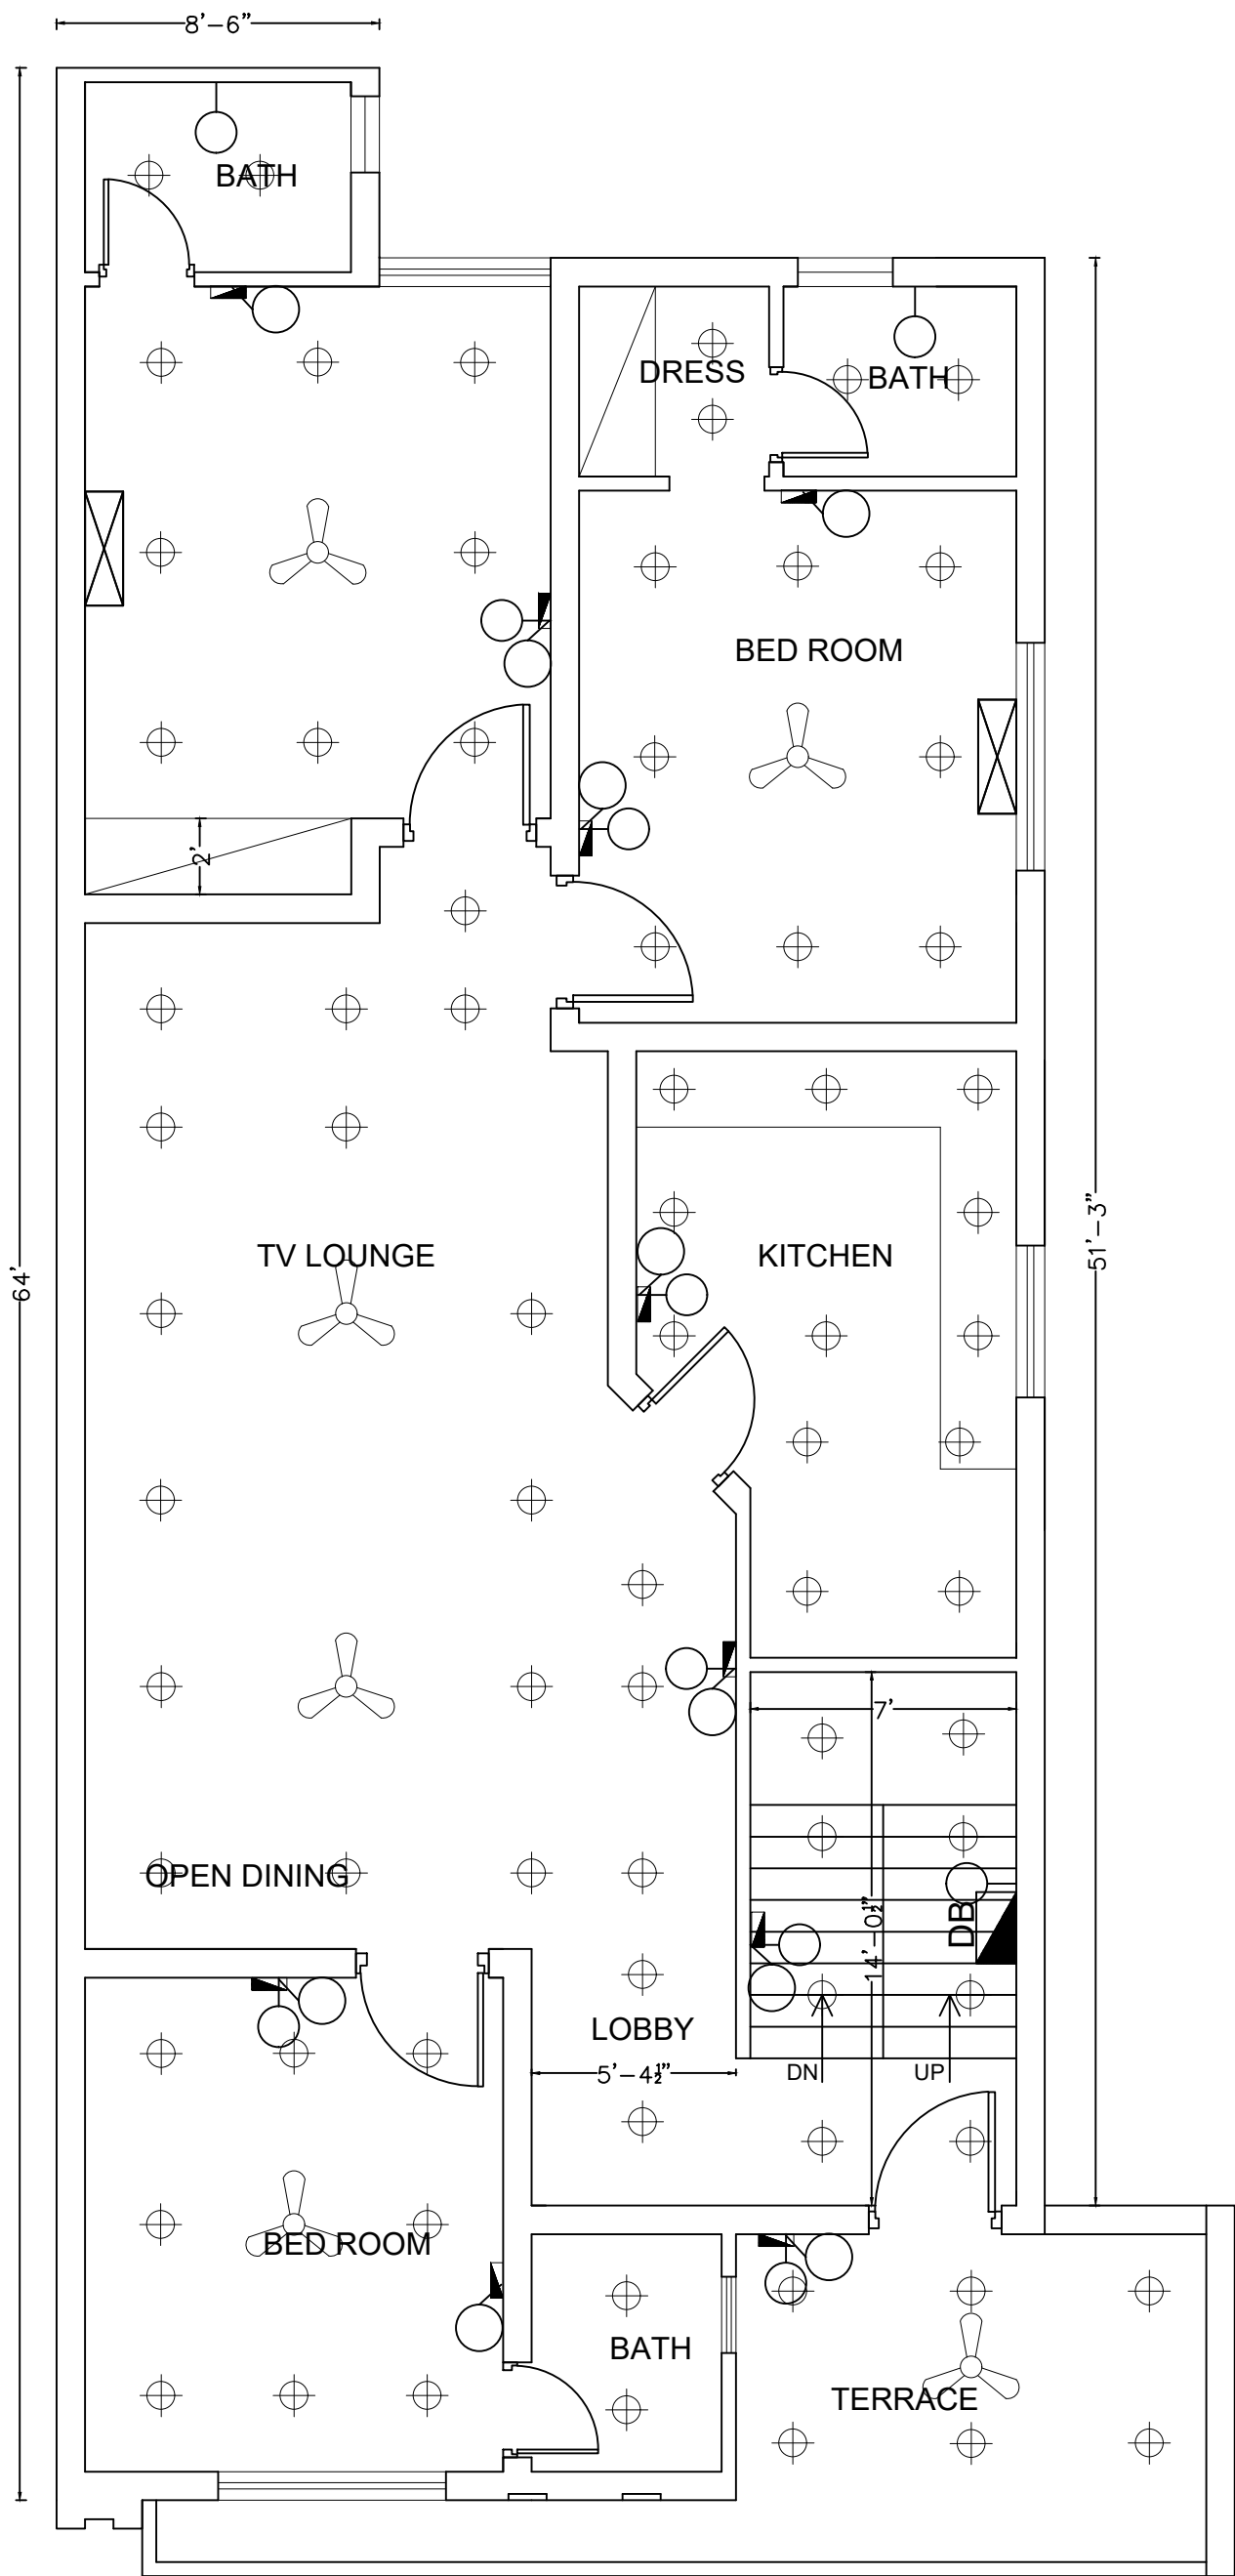

MR.IJAZ
10 MARLA
FIRST FLOOR ELECTRICAL PLAN
SABZAR LAHORE

SALMAN AMJAD AND ASSOCIATES:

ARCHITECT, INTERIOR DESIGN, CONSTRUCTION.
APPROVED AS CATEGORY-A ARCHITECT LDA.
REGISTERED PCATP-06011 AND LDA TPRA-298
OFFICE NO. 35 GROUND FLOOR, MIAN PLAZA,
JOHAR TOWN, LAHORE Mobile no. : 0306-4706139

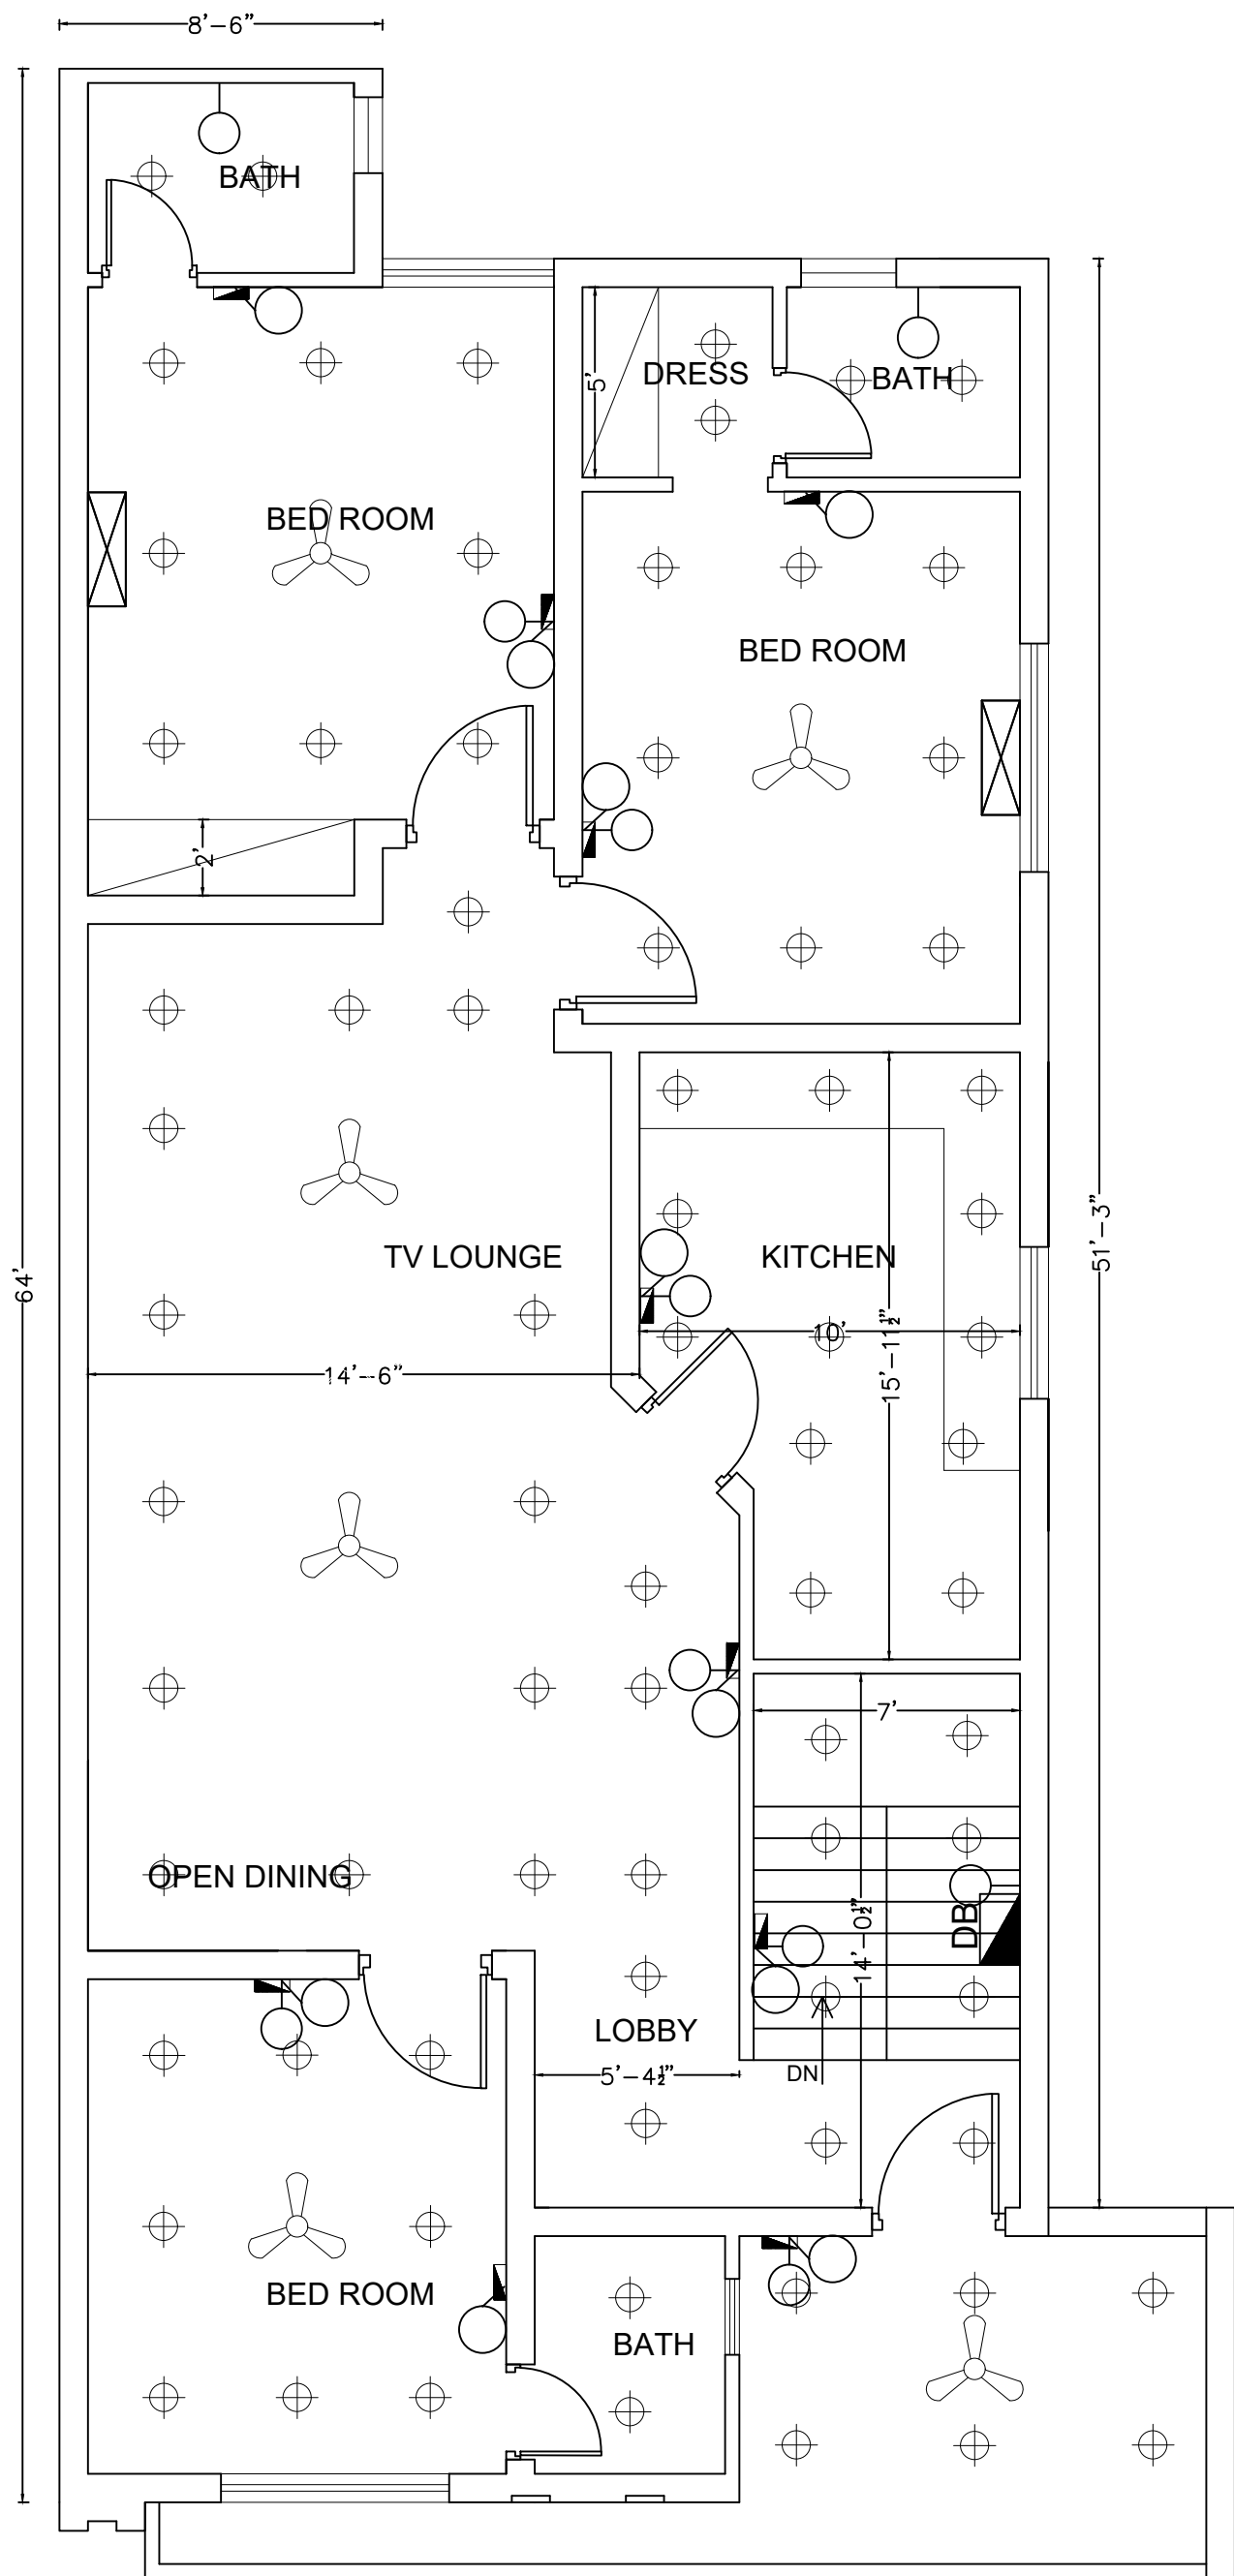


MR.IJAZ
10 MARLA
SECOND FLOOR ELECTRICAL PLAN
SABZAR LAHORE



SALMAN AMJAD AND ASSOCIATES:

ARCHITECT, INTERIOR DESIGN, CONSTRUCTION.
APPROVED AS CATEGORY-A ARCHITECT LDA.
REGISTERED PCATP-06011 AND LDA TPRA-298
OFFICE NO. 35 GROUND FLOOR, MIAN PLAZA,
JOHAR TOWN, LAHORE Mobile no. : 0306-4706139

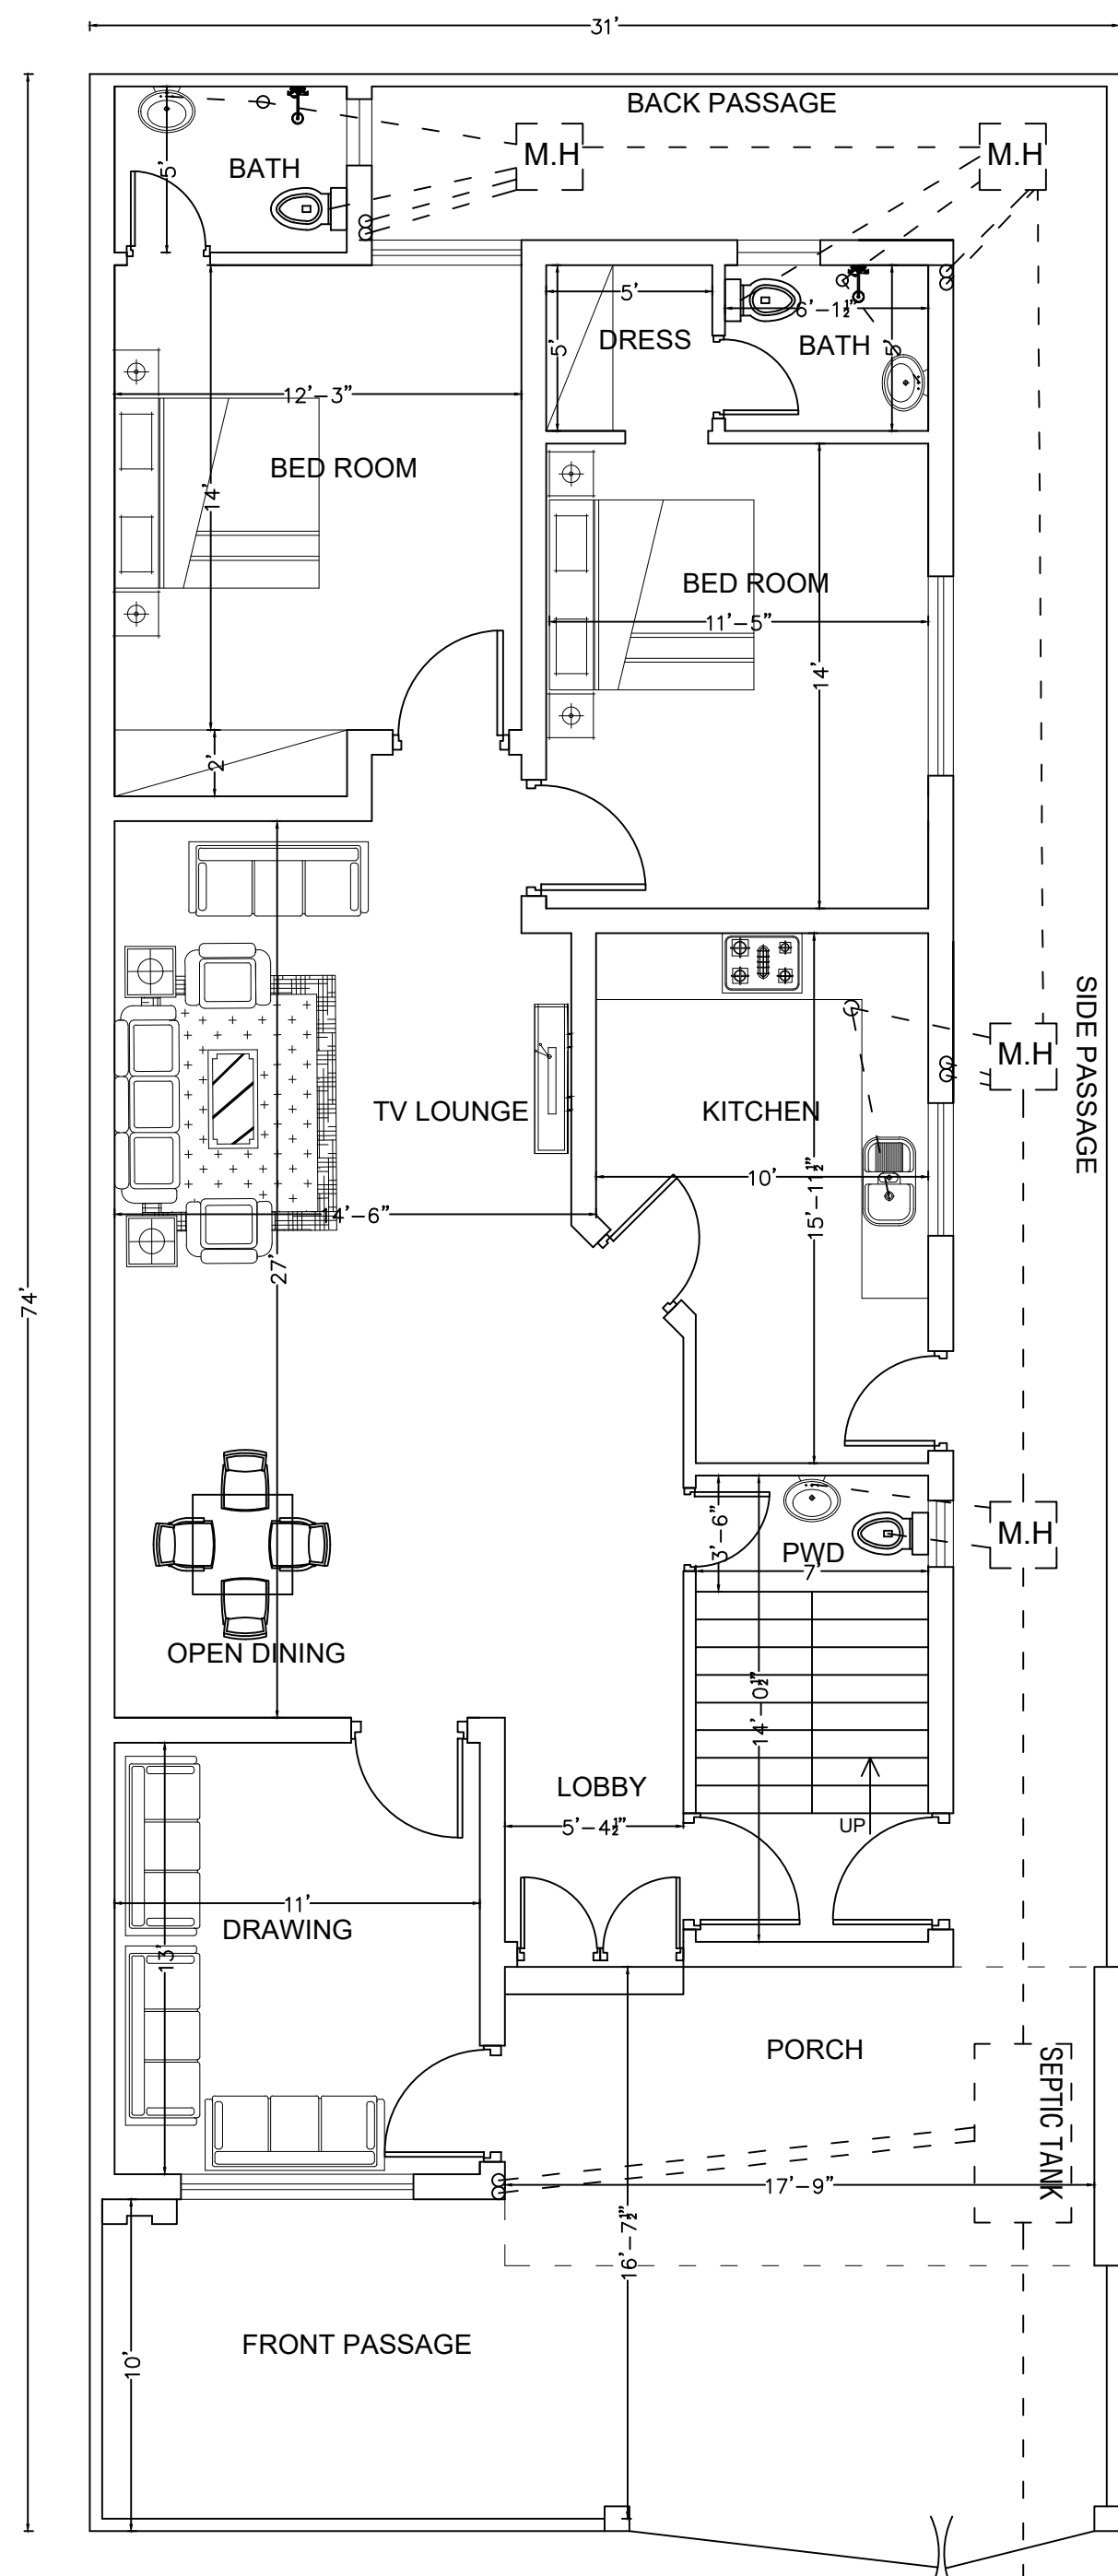


MR.IJAZ
10 MARLA
GROUND SEWER FLOOR
SABZAR LAHORE

TO MAIN SEWER LINE



SALMAN AMJAD AND ASSOCIATES:

ARCHITECT, INTERIOR DESIGN, CONSTRUCTION.
APPROVED AS CATEGORY-A ARCHITECT LDA
REGISTERED PCATP-06011 AND LDA TPRA-298
OFFICE NO. 35 GROUND FLOOR, MIAN PLAZA,
JOHAR TOWN, LAHORE Mobile no. : 0306-4706139

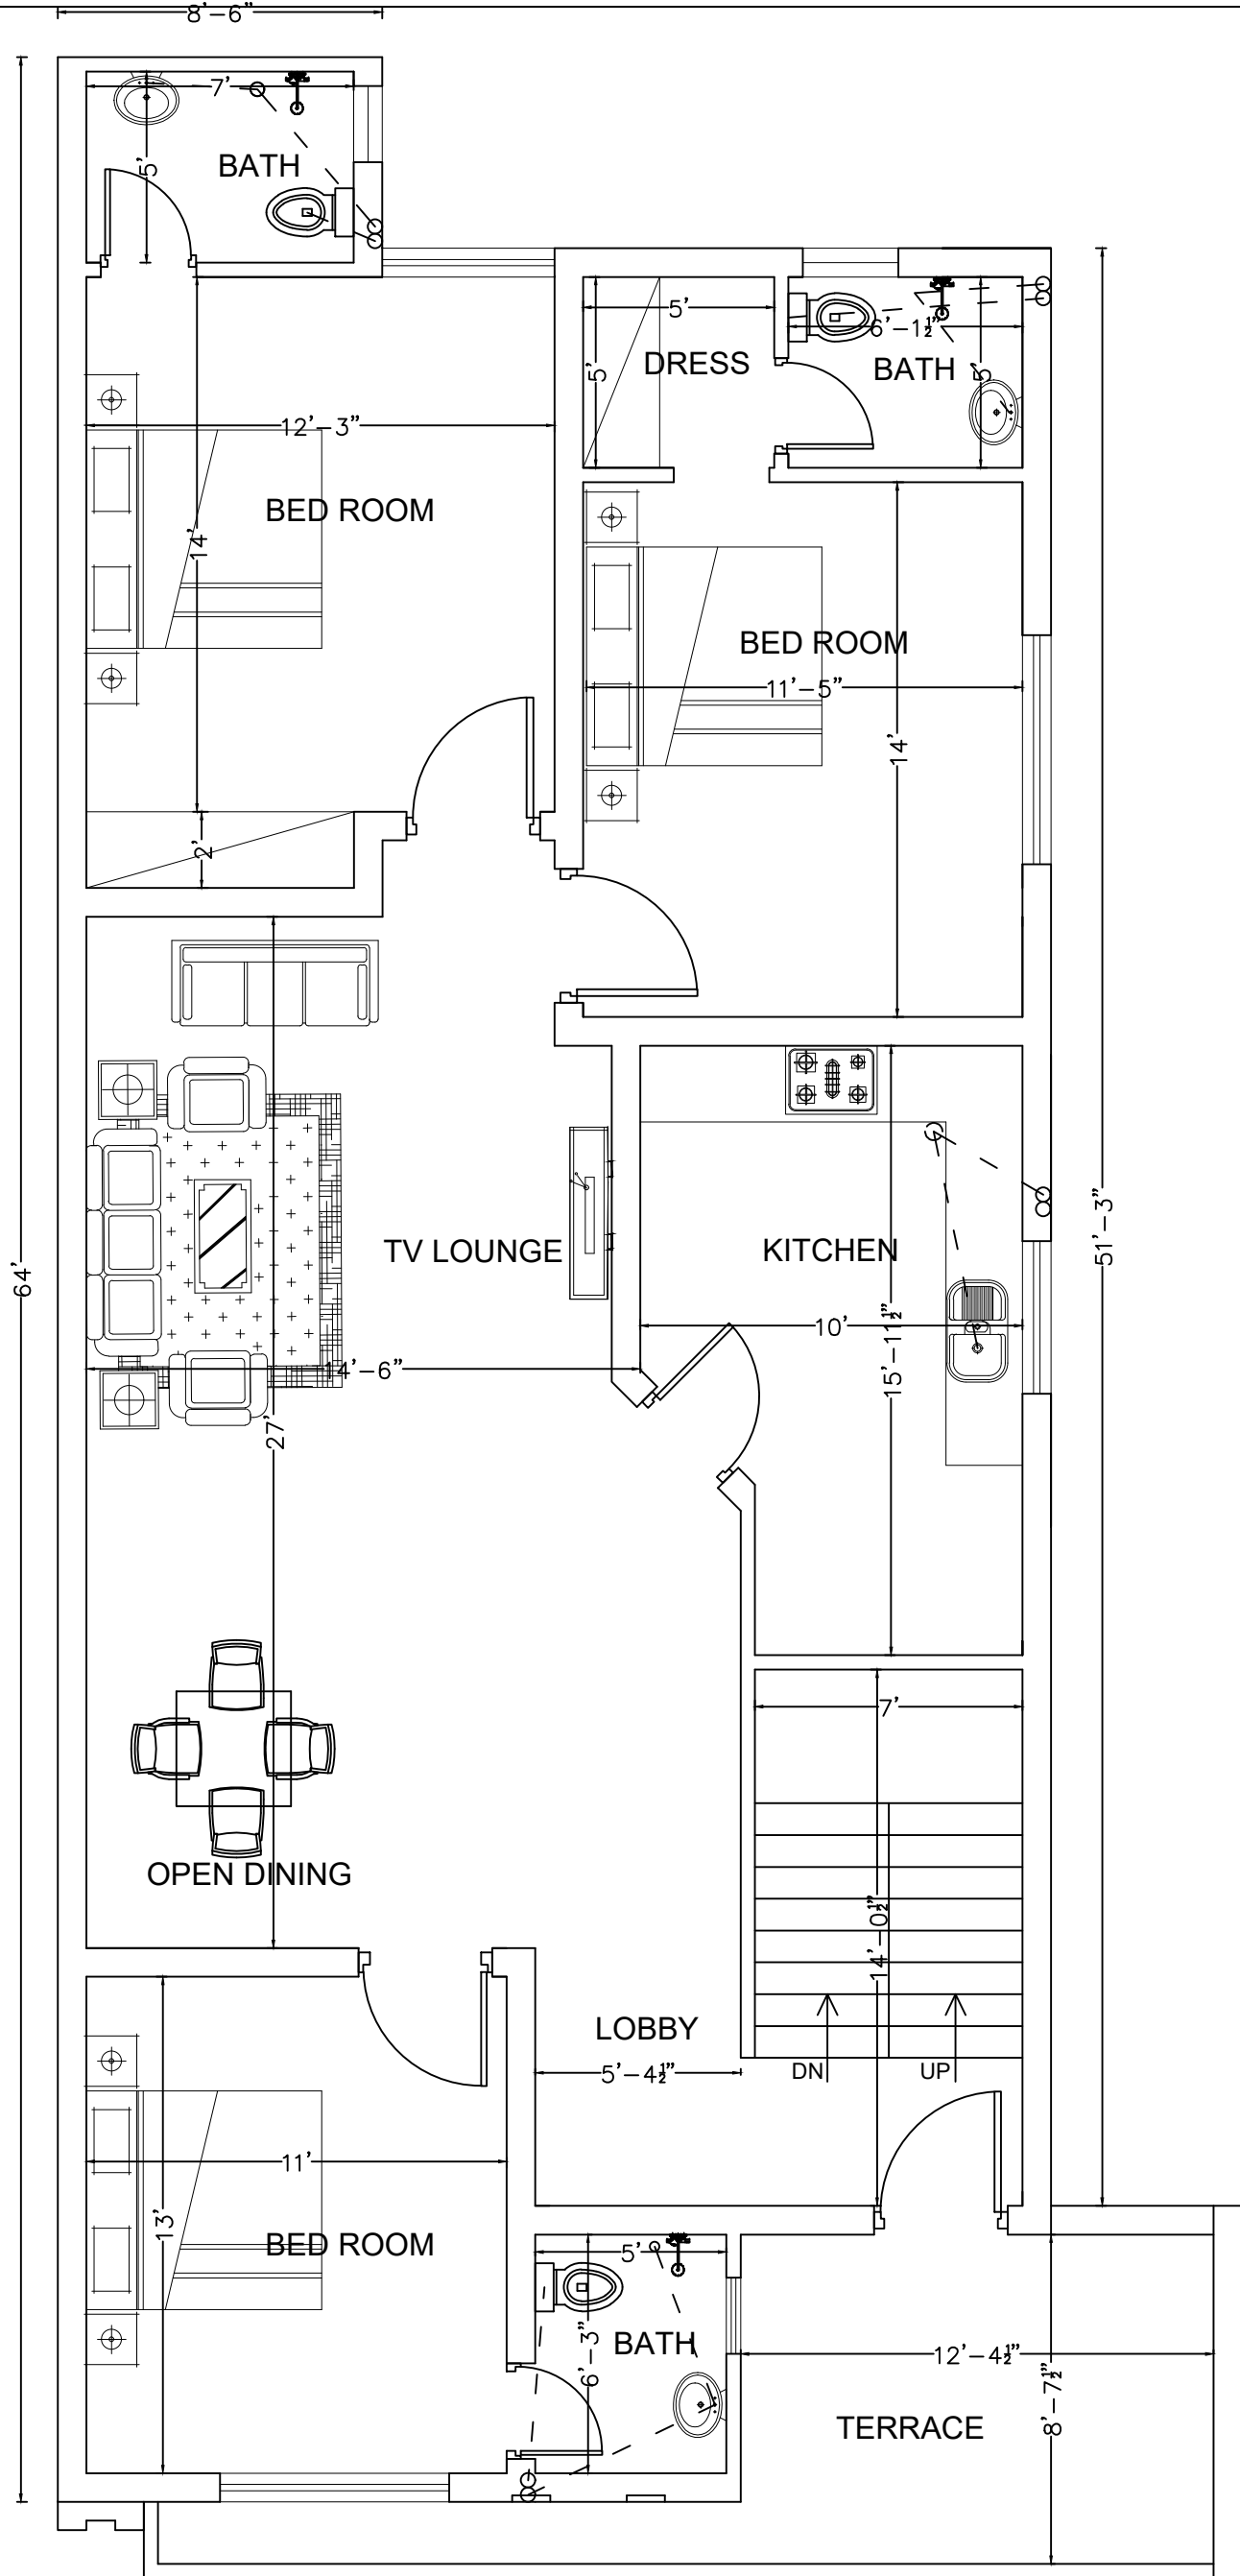


MR.IJAZ
10 MARLA
FIRST SEWER FLOOR
SABZAR LAHORE



SALMAN AMJAD AND ASSOCIATES:

ARCHITECT, INTERIOR DESIGN, CONSTRUCTION.
APPROVED AS CATEGORY-A ARCHITECT LDA.
REGISTERED PCATP-06011 AND LDA TPRA-298
OFFICE NO. 35 GROUND FLOOR, MIAN PLAZA,
JOHAR TOWN, LAHORE Mobile no. : 0306-4706139

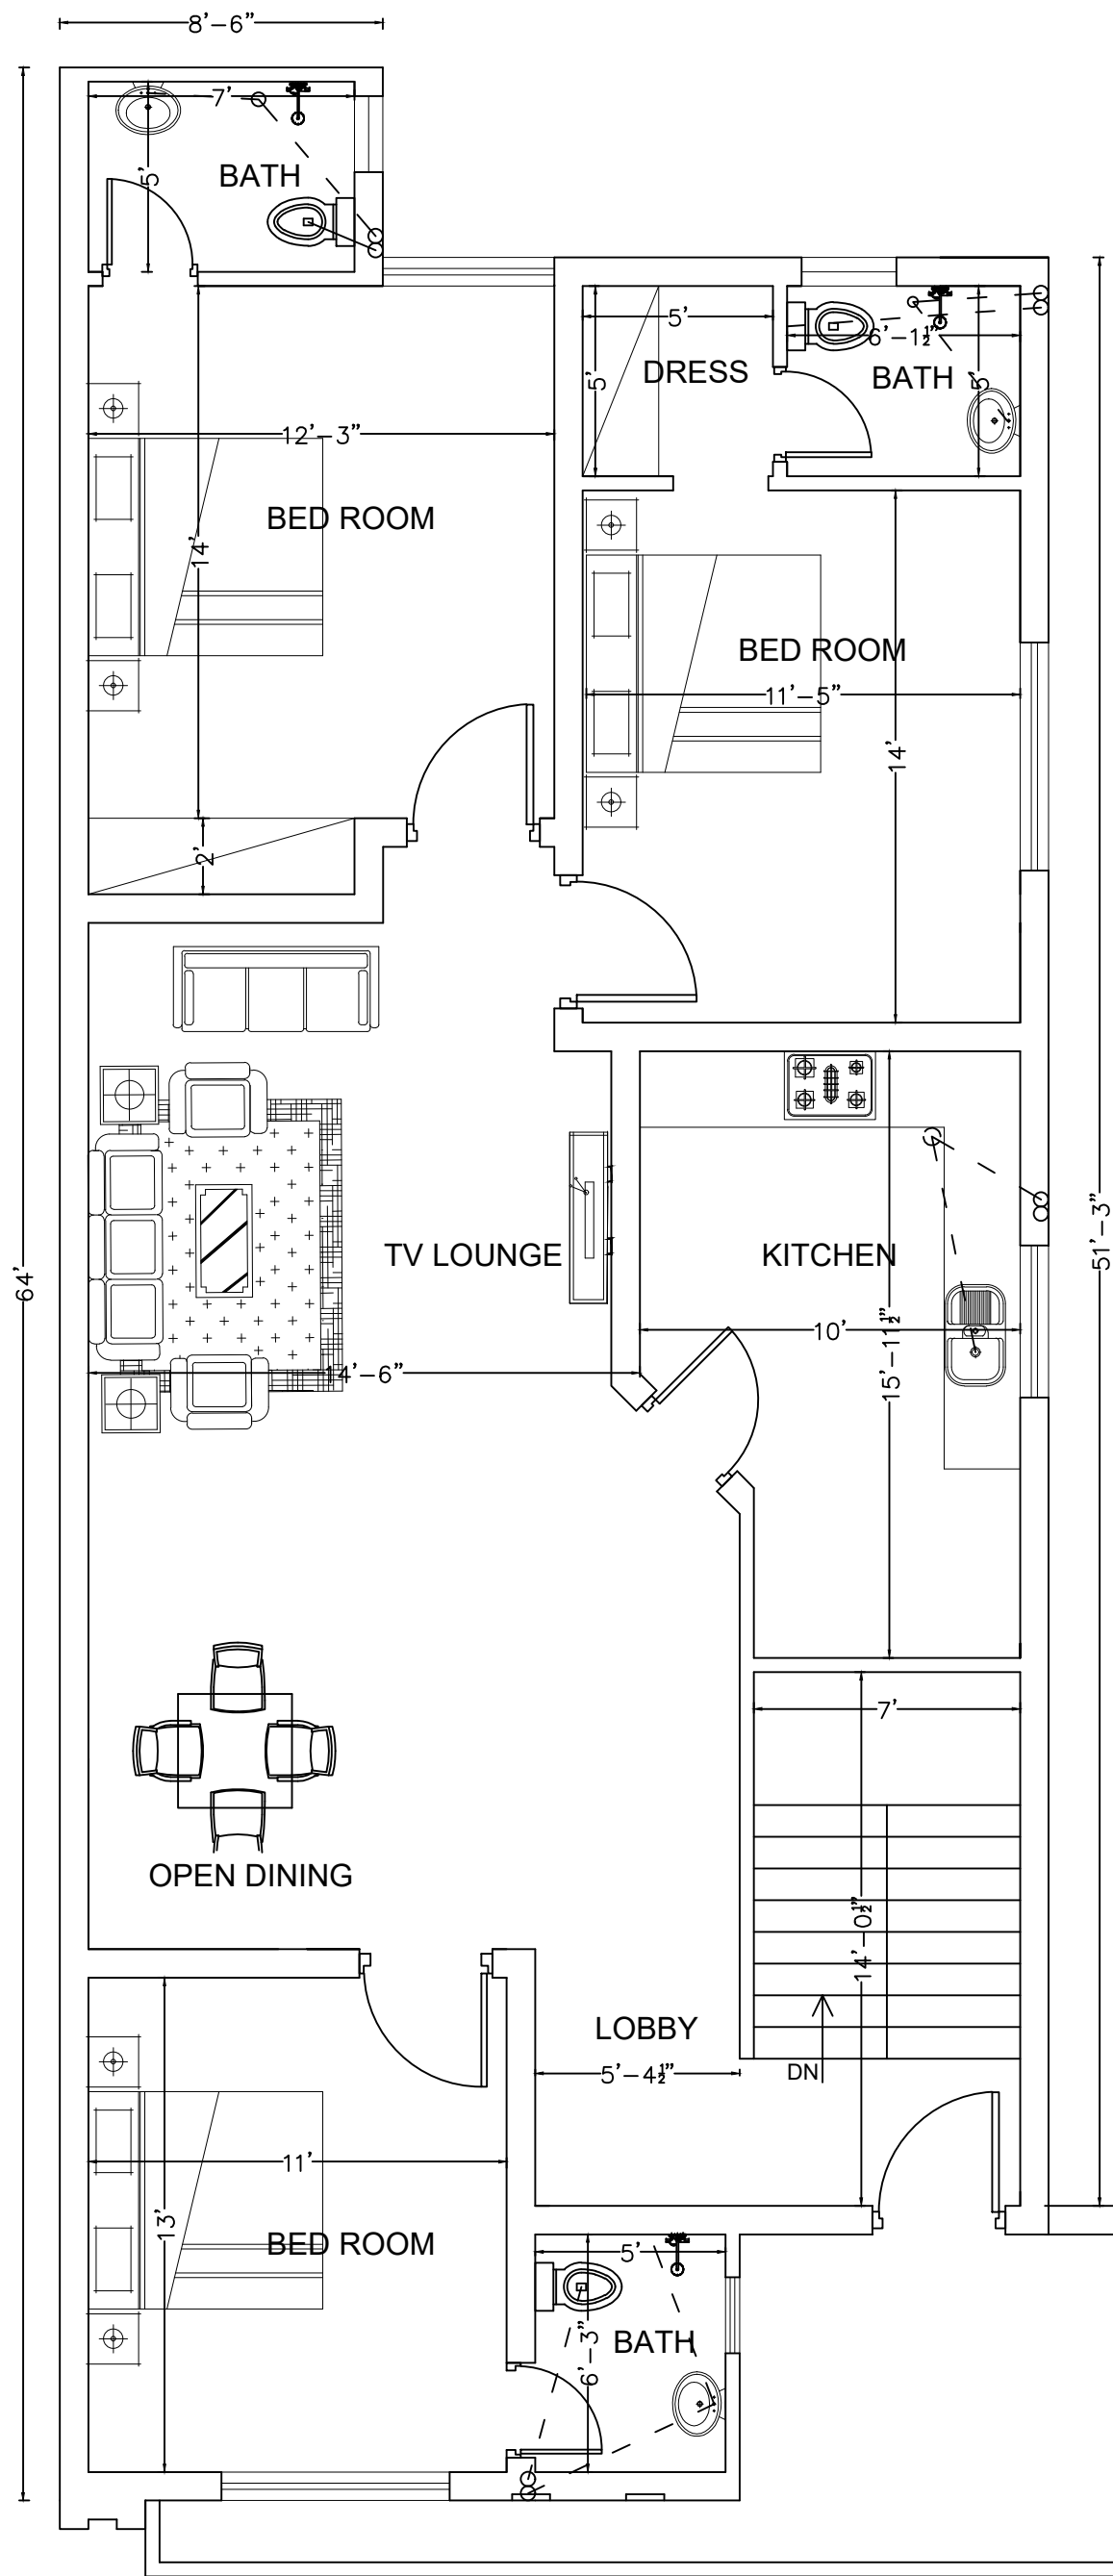


MR.IJAZ
10 MARLA
SECOND SEWER FLOOR
SABZAR LAHORE



SALMAN AMJAD AND ASSOCIATES:

ARCHITECT, INTERIOR DESIGN, CONSTRUCTION.
APPROVED AS CATEGORY-A ARCHITECT LDA.
REGISTERED PCATP-06011 AND LDA TPRA-298
OFFICE NO. 35 GROUND FLOOR, MIAN PLAZA,
JOHAR TOWN, LAHORE Mobile no. : 0306-4706139

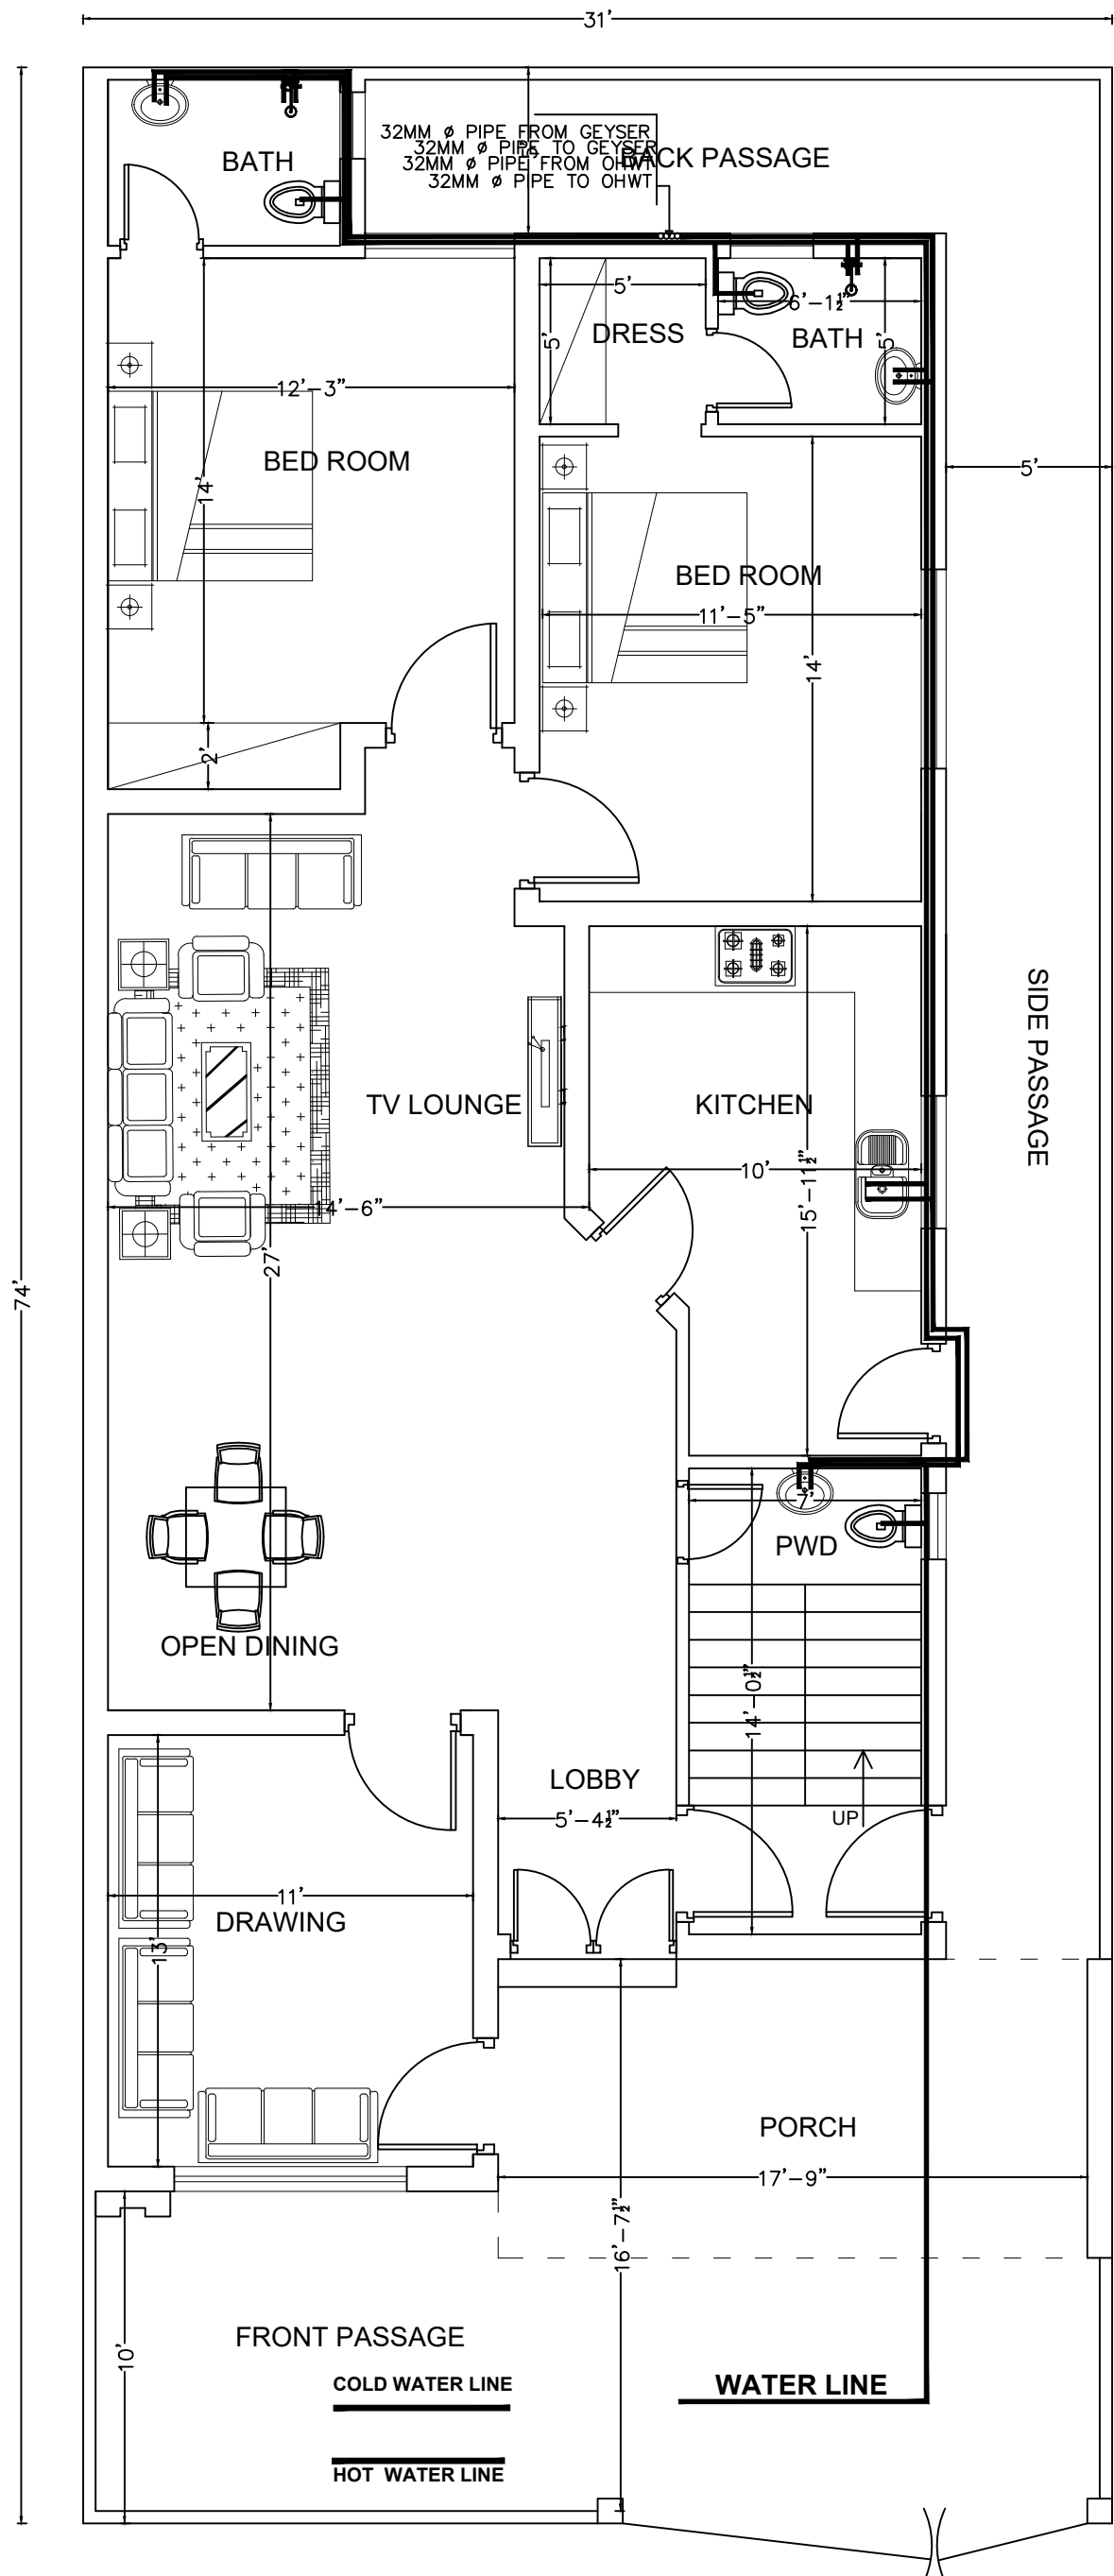


MR.IJAZ
10 MARLA
GROUND PLUMBING FLOOR PLAN
SABZAR LAHORE



SALMAN AMJAD AND ASSOCIATES:

ARCHITECT, INTERIOR DESIGN, CONSTRUCTION,
APPROVED AS CATEGORY-A ARCHITECT LDA,
REGISTERED PCATP-06011 AND LDA TPRA-298
OFFICE NO. 35 GROUND FLOOR, MIAN PLAZA,
JOHAR TOWN, LAHORE Mobile no. : 0306-4706139

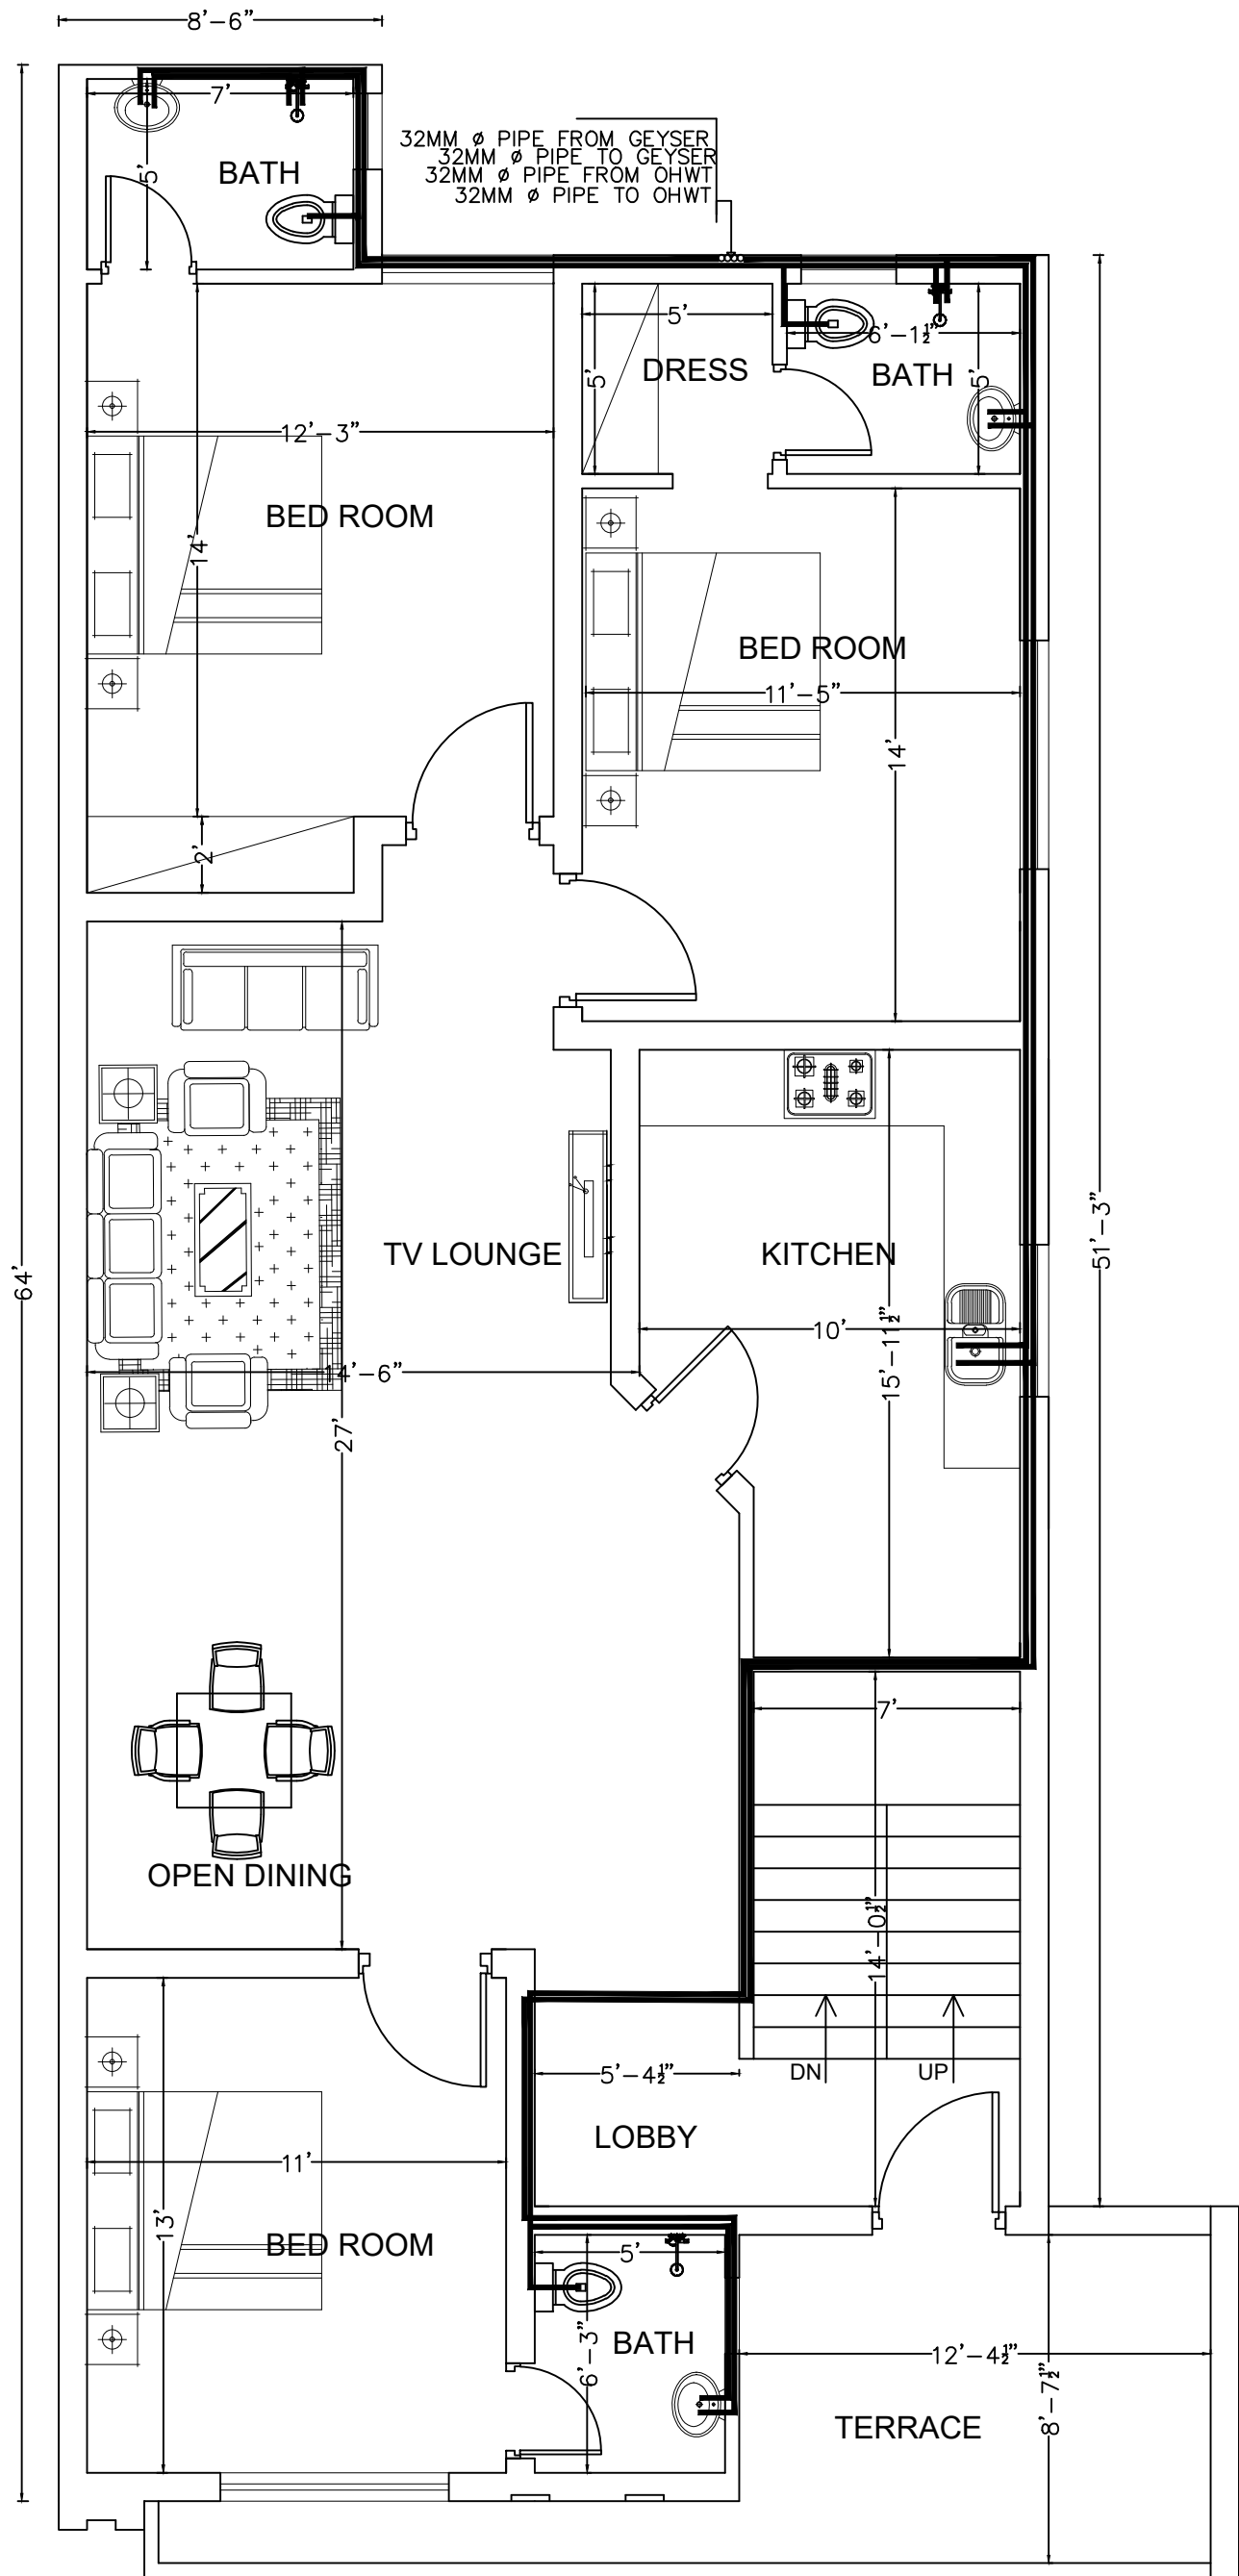


MR.IJAZ
10 MARLA
FIRST PLUMBING FLOOR PLAN
SABZAR LAHORE

COLD WATER LINE
HOT WATER LINE



SALMAN AMJAD AND ASSOCIATES:

ARCHITECT, INTERIOR DESIGN, CONSTRUCTION.
APPROVED AS CATEGORY-A ARCHITECT LDA.
REGISTERED PCATP-06011 AND LDA TPRA-298
OFFICE NO. 35 GROUND FLOOR, MIAN PLAZA,
JOHAR TOWN, LAHORE Mobile no. : 0306-4706139

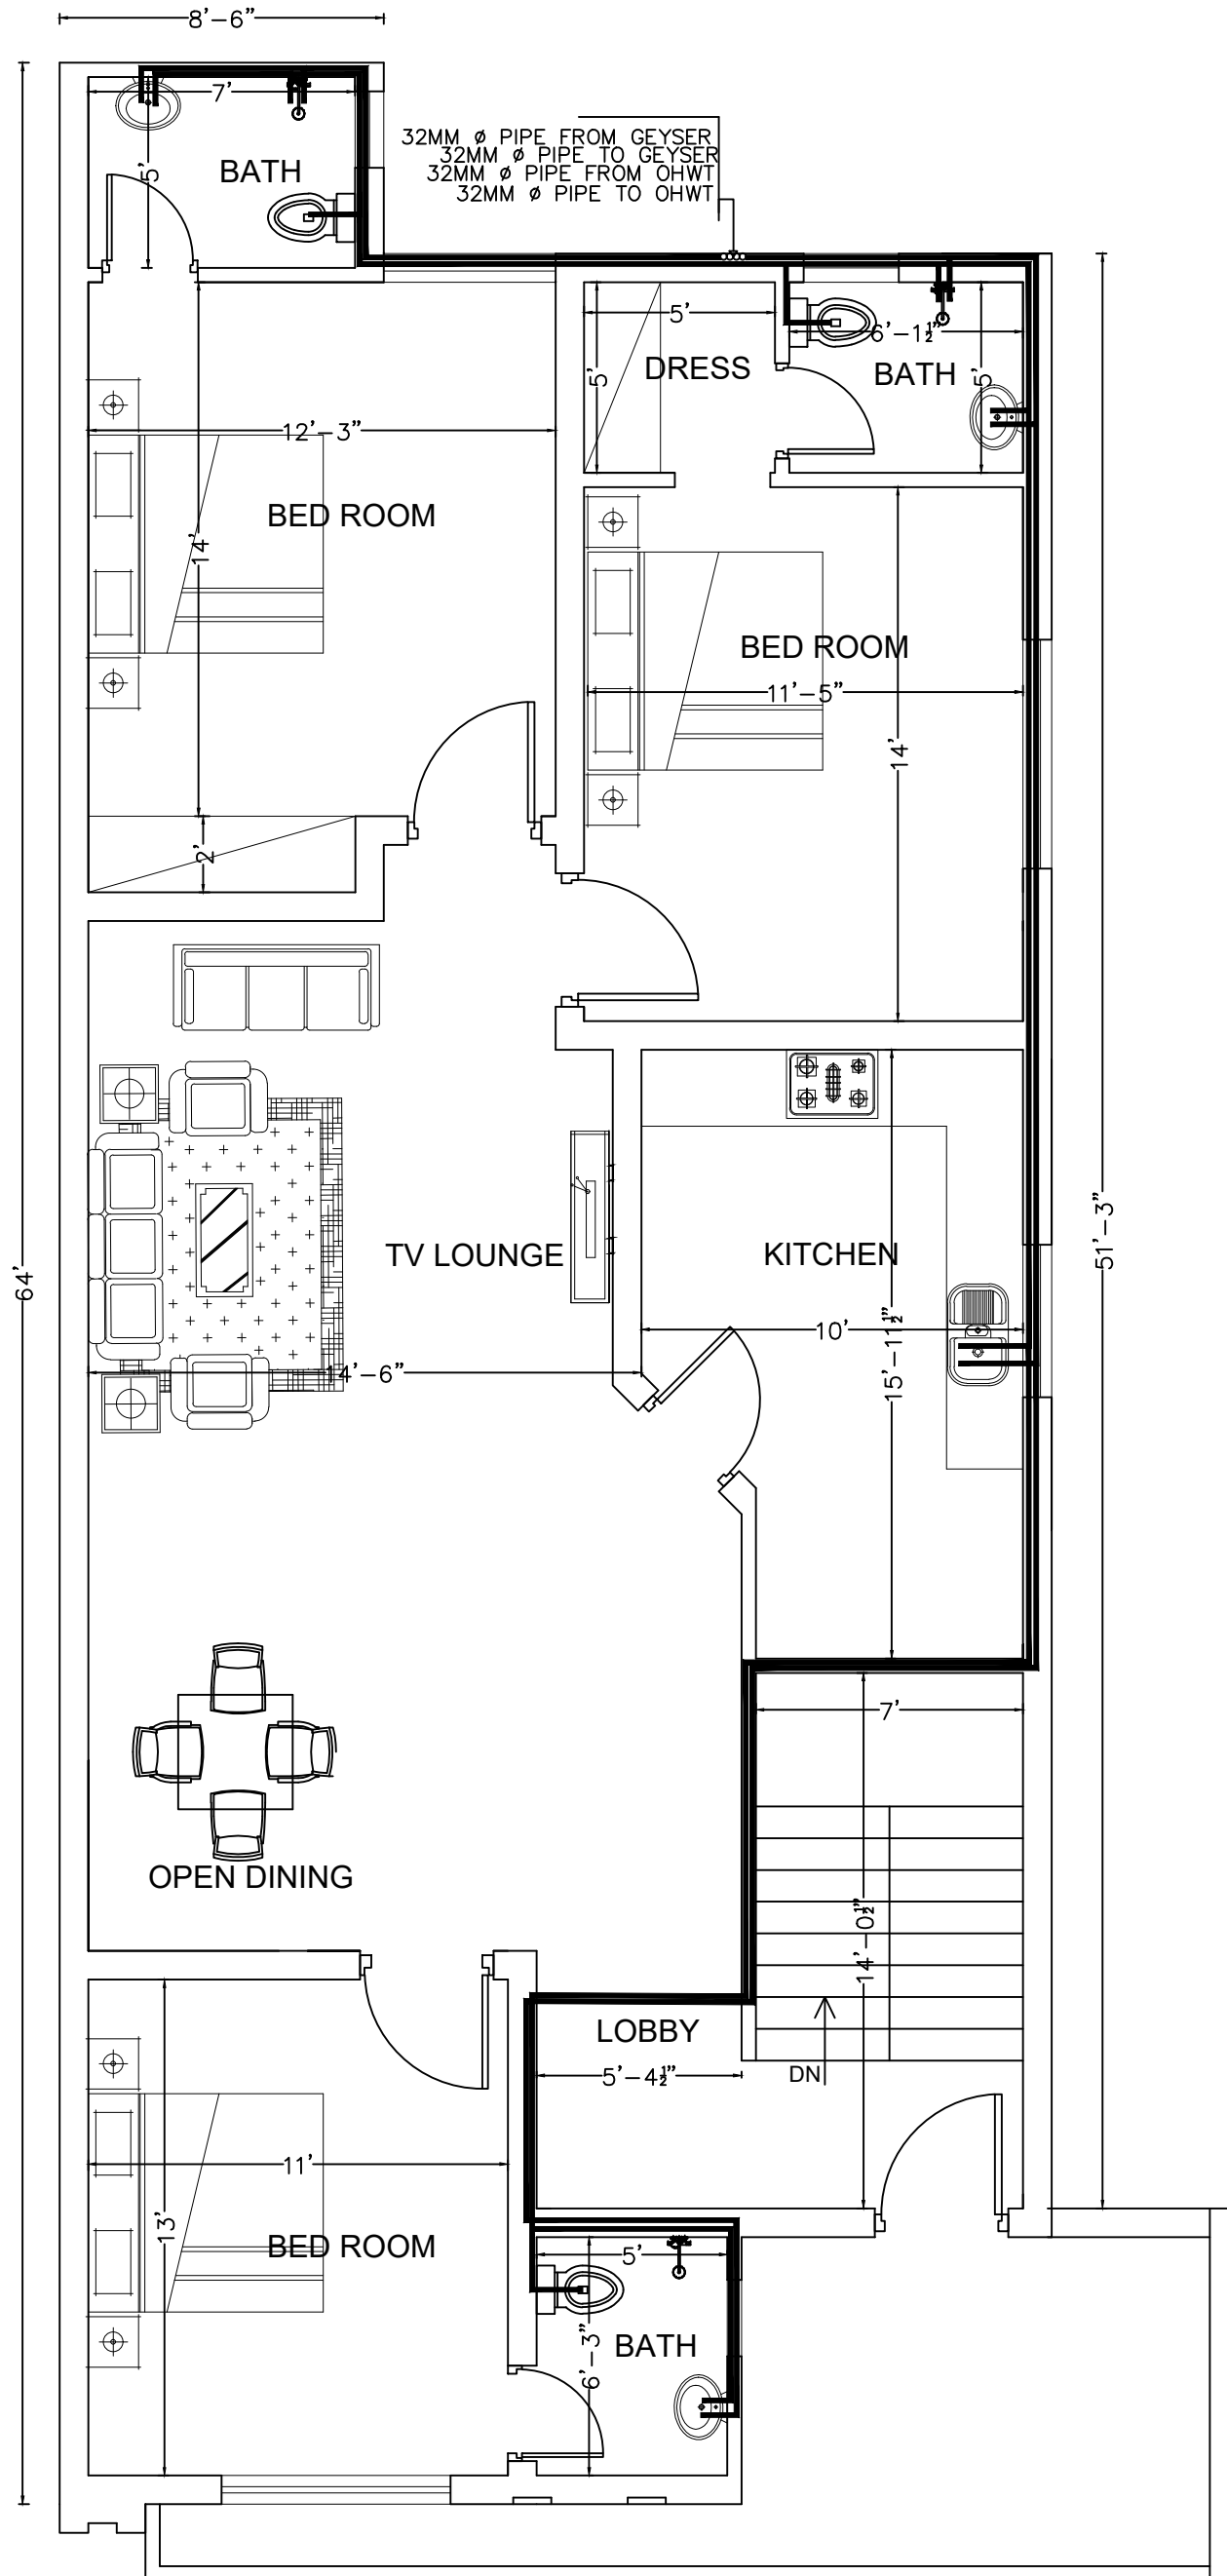


MR.IJAZ
10 MARLA
SECOND PLUMBING FLOOR PLAN
SABZAR LAHORE

COLD WATER LINE
HOT WATER LINE



SALMAN AMJAD AND ASSOCIATES:

ARCHITECT, INTERIOR DESIGN, CONSTRUCTION.
APPROVED AS CATEGORY-A ARCHITECT LDA.
REGISTERED PCATP-06011 AND LDA TPRA-298
OFFICE NO. 35 GROUND FLOOR, MIAN PLAZA,
JOHAR TOWN, LAHORE Mobile no. : 0306-4706139

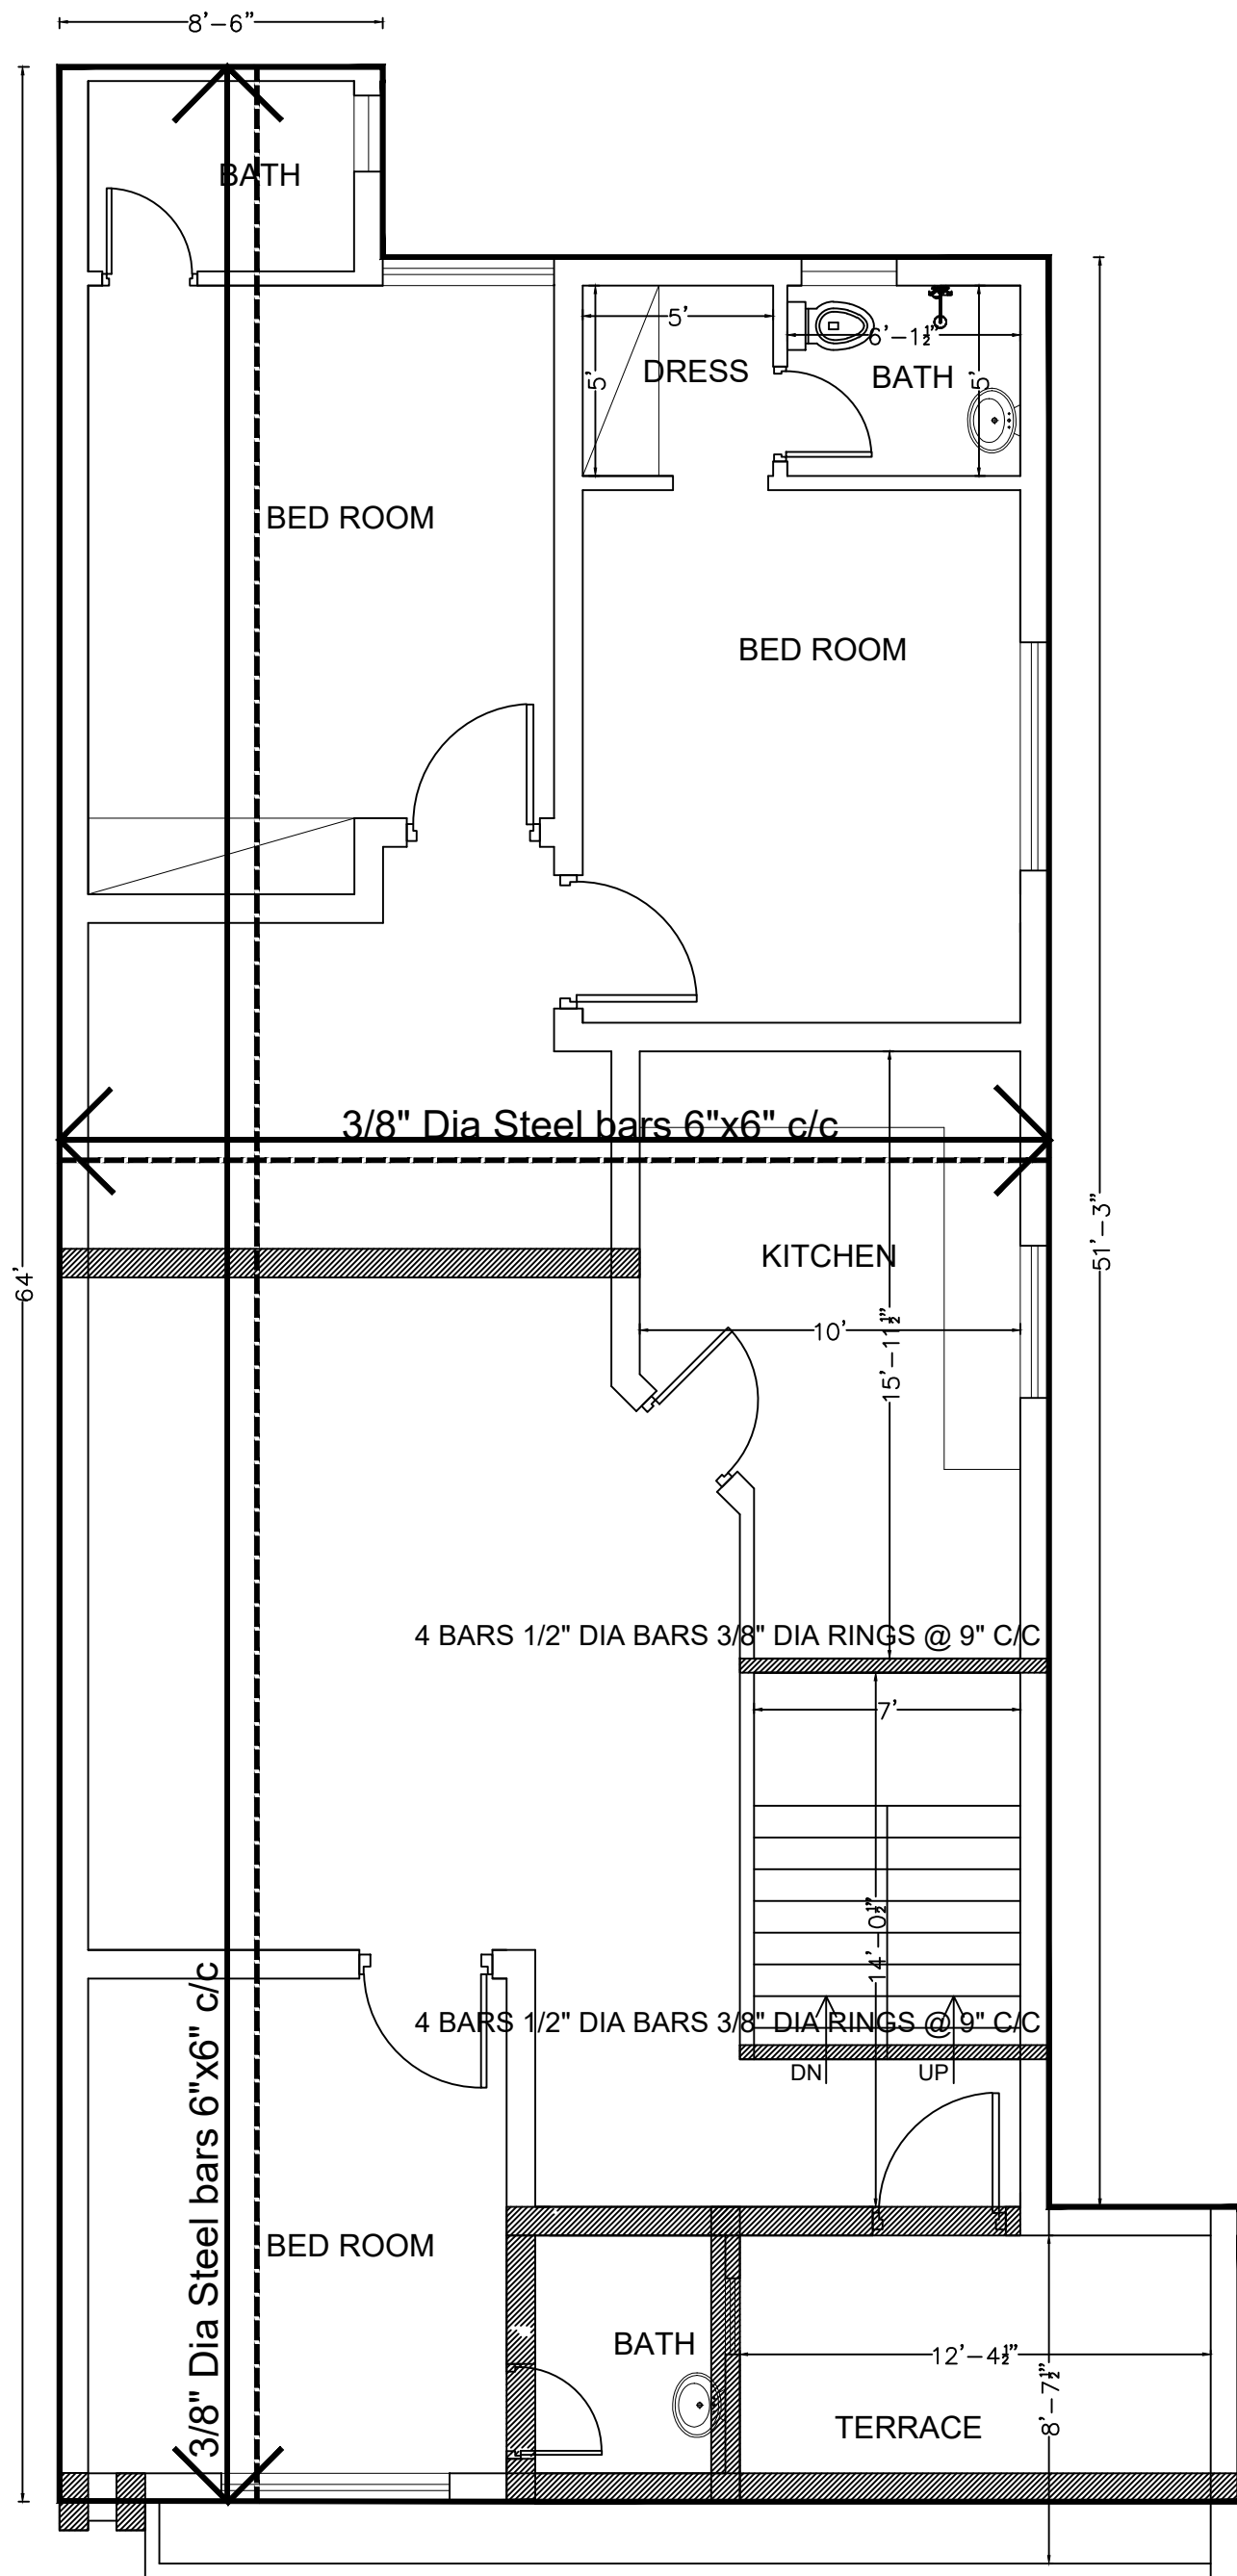


MR.IJAZ
10 MARLA
FIRST FLOOR STRUCTURE PLAN
SABZAR LAHORE



SALMAN AMJAD AND ASSOCIATES:

ARCHITECT, INTERIOR DESIGN, CONSTRUCTION.
APPROVED AS CATEGORY-A ARCHITECT LDA.
REGISTERED PCATP-06011 AND LDA TPRA-298
OFFICE NO. 35 GROUND FLOOR, MIAN PLAZA,
JOHAR TOWN, LAHORE Mobile no. : 0306-4706139

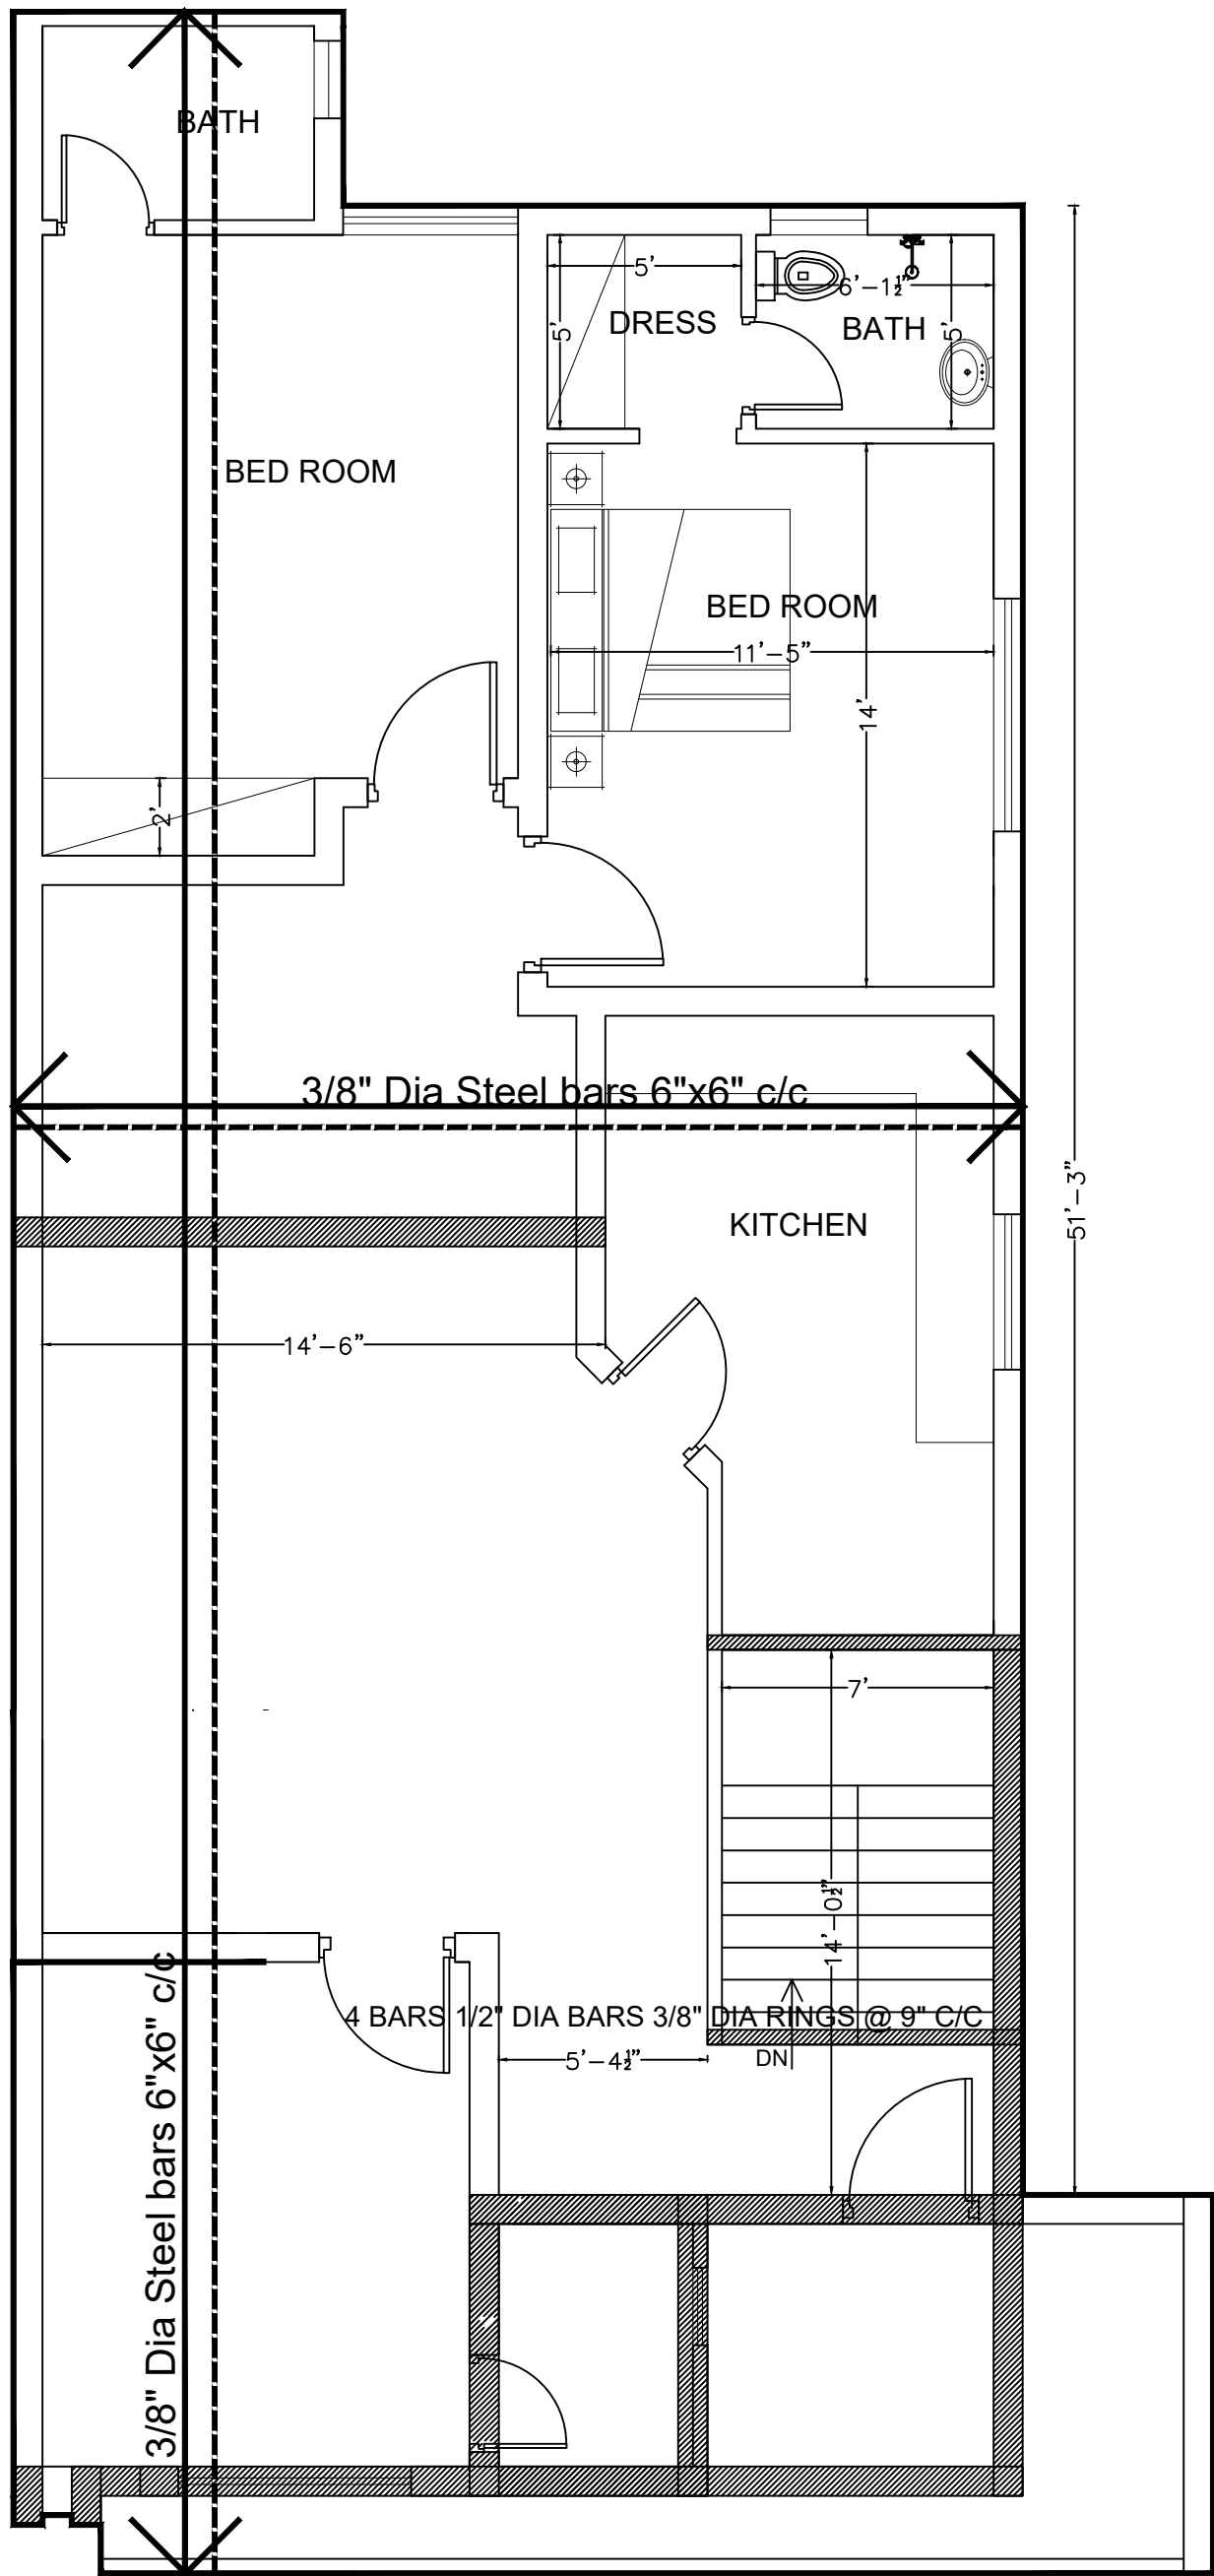

MR.IJAZ
10 MARLA
SECOND FLOOR STRUCTURE PLAN
SABZAR LAHORE



SALMAN AMJAD AND ASSOCIATES:

ARCHITECT, INTERIOR DESIGN, CONSTRUCTION.
APPROVED AS CATEGORY-A ARCHITECT LDA.
REGISTERED PCATP-06011 AND LDA TPRA-298
OFFICE NO. 35 GROUND FLOOR, MIAN PLAZA,
JOHAR TOWN, LAHORE Mobile no. : 0306-4706139